Lift 13,14

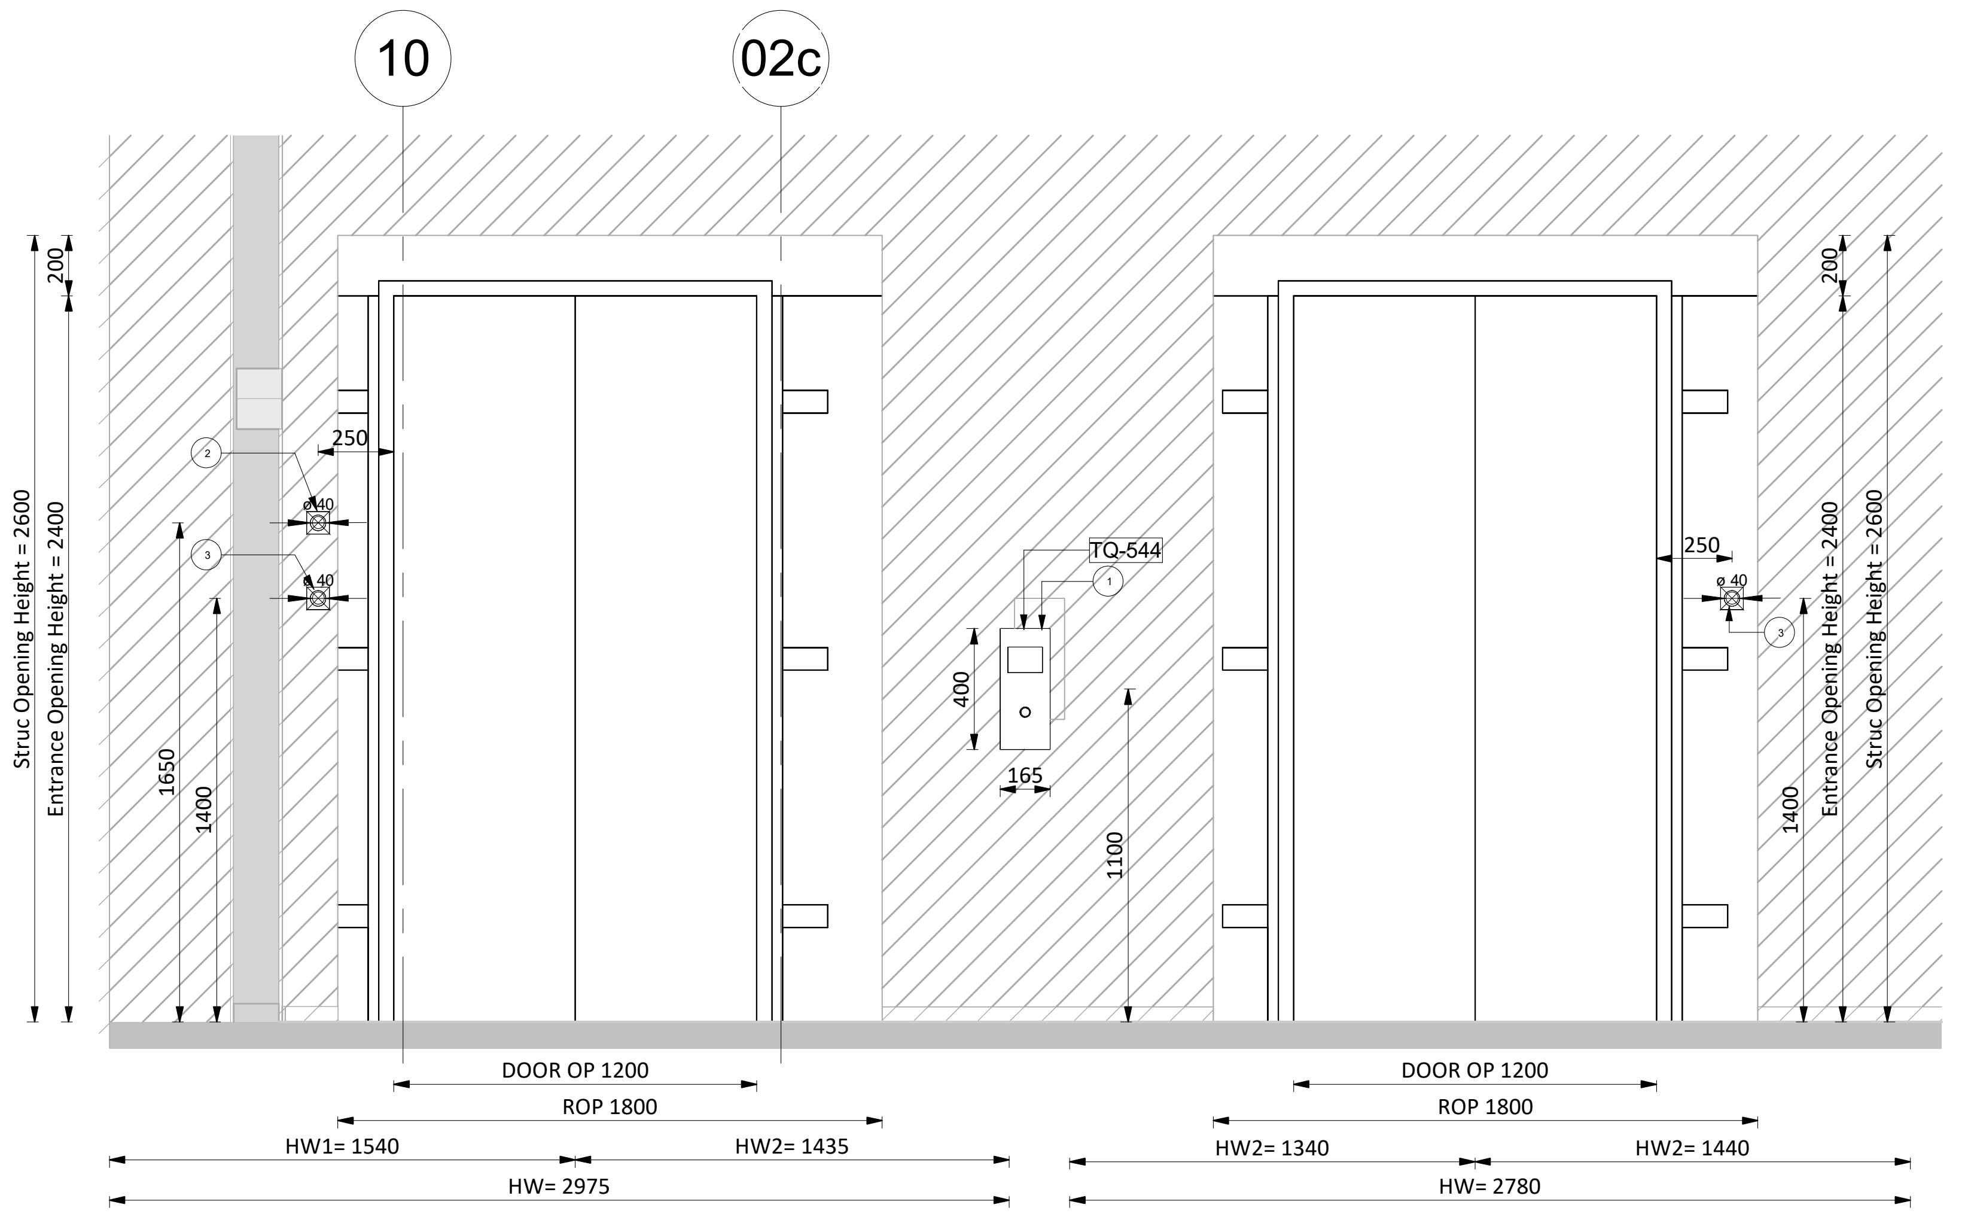
10
02c
200
Struc Opening Height = 2600
Entrance Opening Height = 2400
250
1650
1400
TQ-544
400
165
1100
250
ø 40
1400
Entrance Opening Height = 2400
Struc Opening Height = 2600
DOOR OP 1200
ROP 1800
HW1= 1540
HW2= 1435
HW= 2975
DOOR OP 1200
ROP 1800
HW2= 1340
HW2= 1440
HW= 2780

1.HALL BUTTON(HBP)
165X400 THROUGH HOLE ,IN THE DISCRETIONARY FLOOR
2.FIREMAN SERVICE (FSS)
Φ40mm THROUGH HOLE, IN THE MAIN FLOOR
3. PIT INSPECTION RESET SW
Φ40mm ONLY FOR PIT LANDING
4.E&I PANEL.

1 Door Elevation At "G" Floor (FRONT) - ELEV -L13 & L14

1 : 25

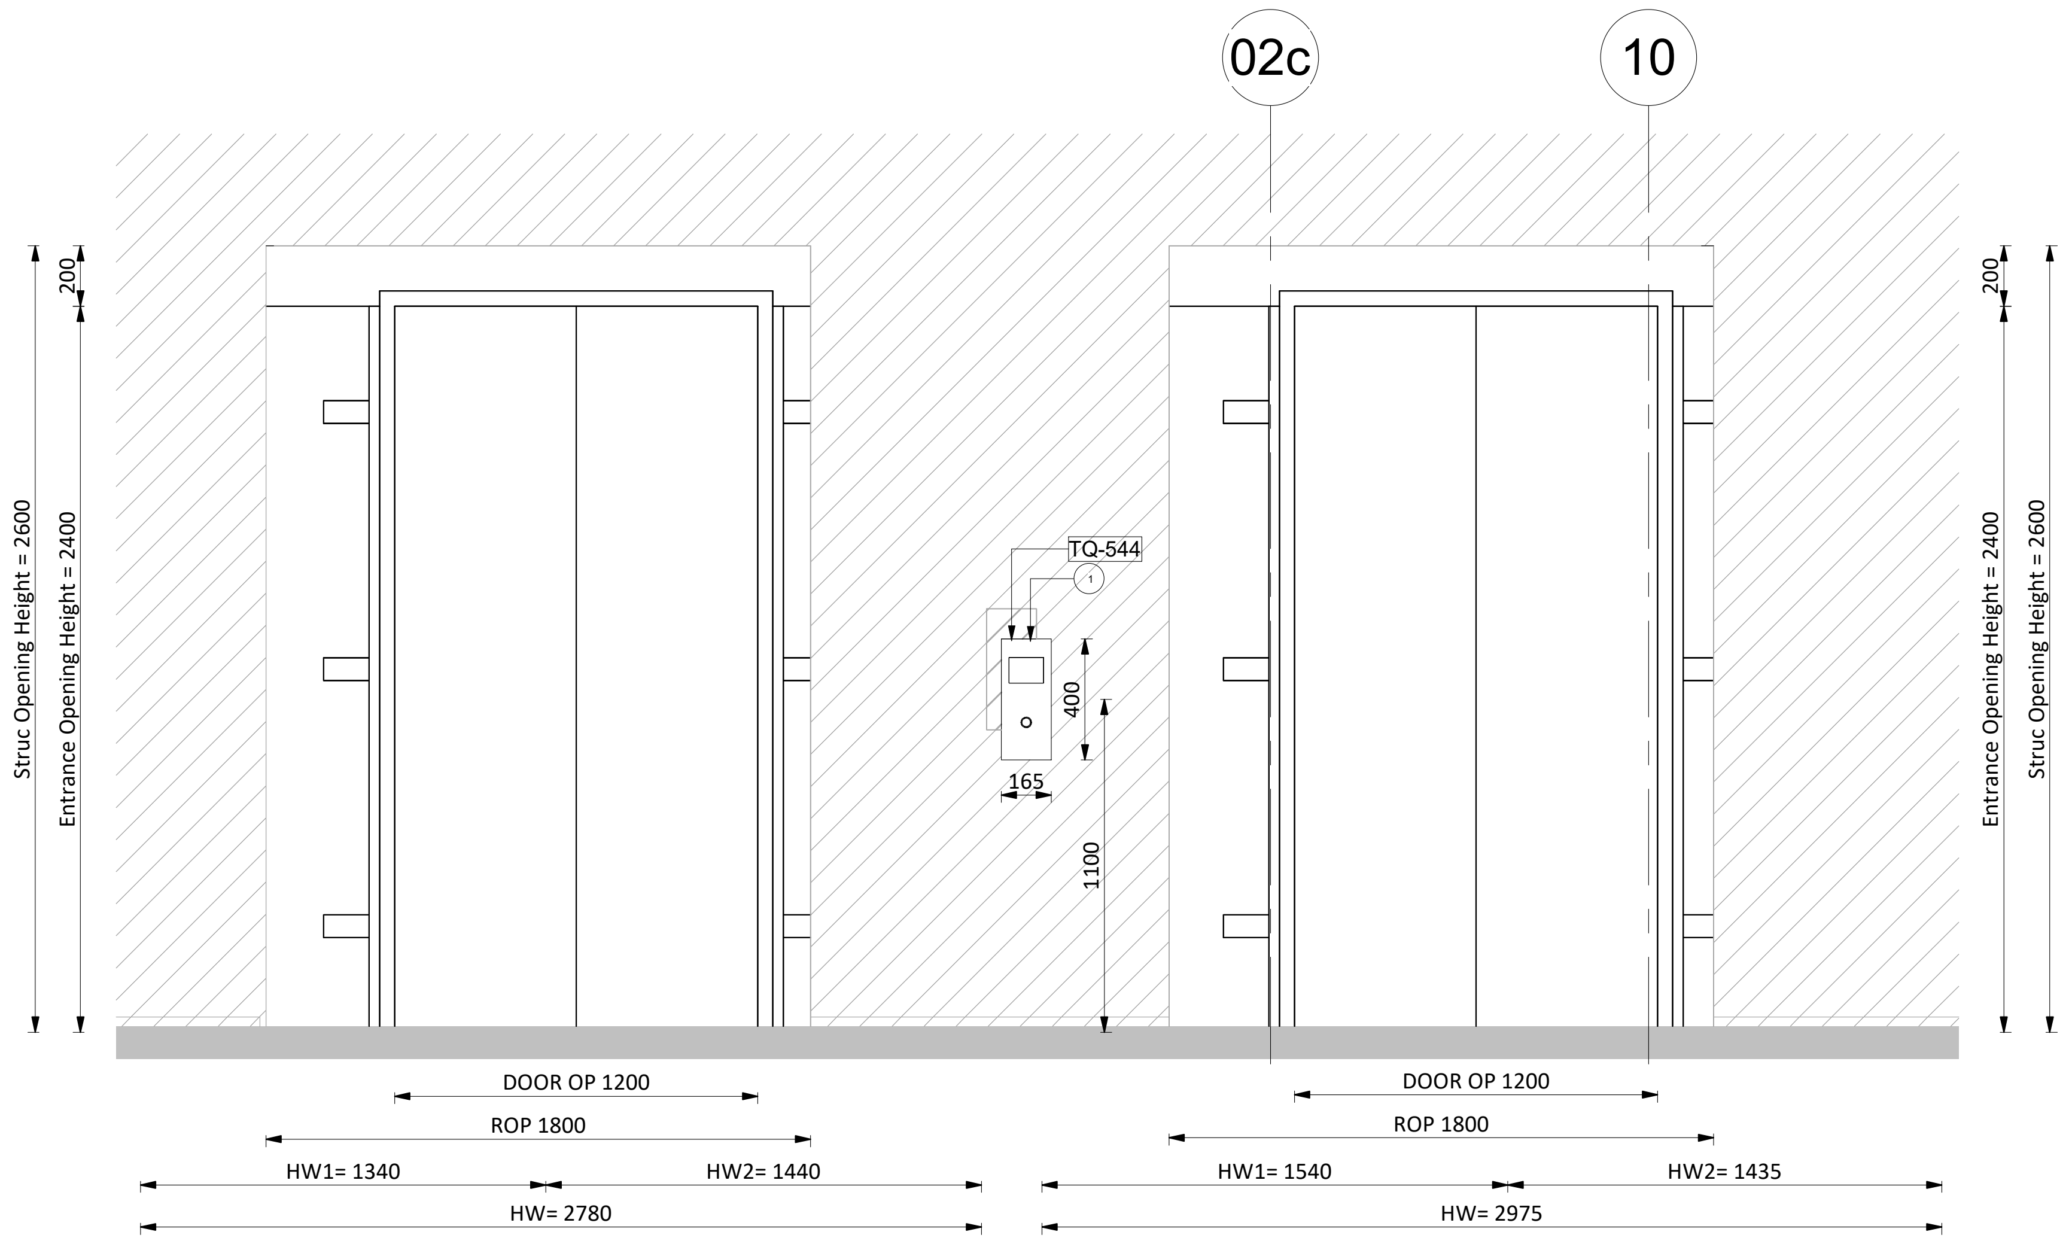
02c
10
200
Struc Opening Height = 2600
Entrance Opening Height = 2400
TQ-544
400
165
1100
Entrance Opening Height = 2400
Struc Opening Height = 2600
DOOR OP 1200
ROP 1800
HW1= 1340
HW2= 1440
HW= 2780
DOOR OP 1200
ROP 1800
HW1= 1540
HW2= 1435
HW= 2975

2 Door Elevation At "1" Floor (REAR) - ELEV -L13 & L14

1 : 25

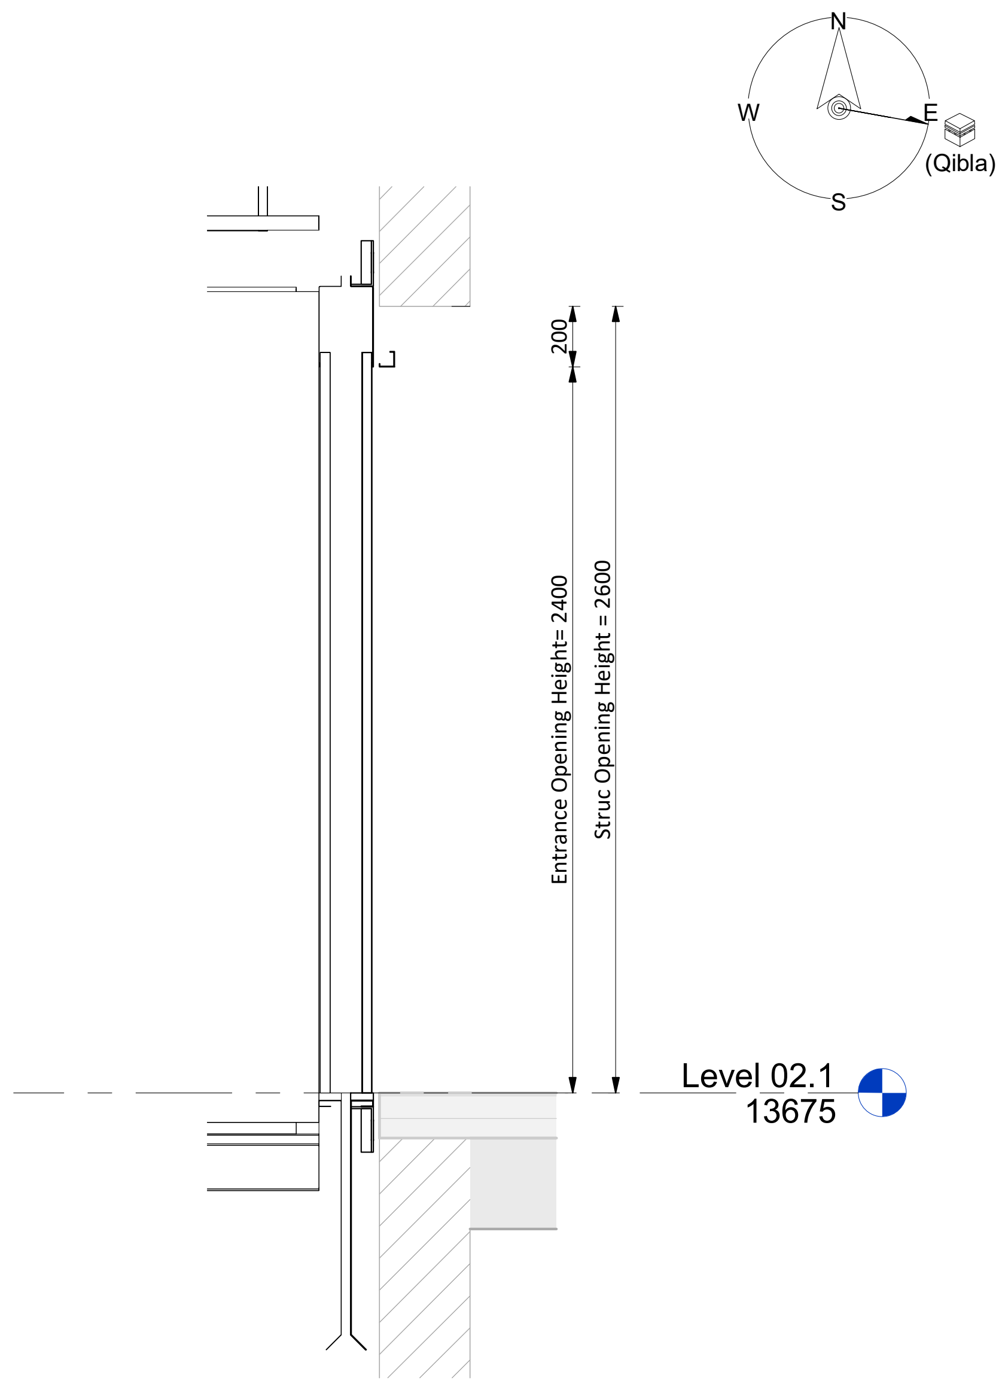
N
W
E
S
(Qibla)
200
Entrance Opening Height= 2400
Struc Opening Height = 2600
Level 02.1
13675

3 Cross-Section View A-A - ELEV -L13 & L14

1 : 25

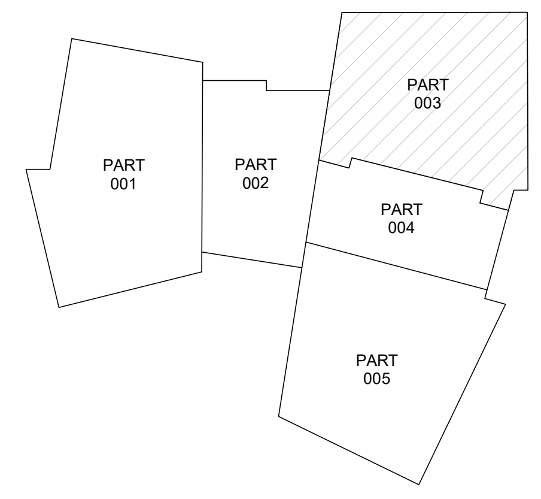
PART 001
PART 002
PART 003
PART 004
PART 005

KEY PLAN

GENERAL NOTES: ALL LEVELS SHOWN ON THE DRAWING ARE CHART DATUM LEVELS PROJECT LEVEL+0.000 = +3.700 CHART DATUM.

dar Dar Al-Handasah consultants (Shair and Partners)
Checked and Reviewed
Refer to CRS : SD-OPE-MBL-JCDC-01478

For ELE Panels distribution and Connection
Refer to (JOH-ICD-S5-01-056-003-02-SD-EL-011623)

DRAWING / DOCUMENT REFERENCE

NO.	NUMBER	TITLE	REV.
01	L-13 & L-14	JOH-HLA-S4-01-056-XXX-02-DR-AR-011120	F00
02		JOH-BHC-S4-01-056-XXX-XX-DR-VT-015001	
03		JOH-BHC-S4-01-056-XXX-XX-DR-VT-010001	
04		JOH-BHC-S4-01-056-005-ZZ-DR-VT-013001	
05		JOH-BHC-S4-01-056-005-ZZ-DR-VT-011001	
06		TQ-OPE-MBL-JCDC-00952	
07		TQ-OPE-MBL-JCDC-00544	
08		TQ-OPE-MBL-JCDC-00222	
09		TQ-OPE-MBL-JCDC-01052	
10		JCD-OPE-MBL-MR-003-NMR-601-03	
11		JCD-OPE-MBL-MR-003-NMR-602-01	

REVIEWED BY DISCIPLINE	SIGNATURE	DATE
ARCHITECTURAL	[illegible]	[illegible]-04-22
STRUCTURAL	[illegible]	[illegible]
MECHANICAL	ShA	2026-04-22
PLUMBING	ShA	2026-04-22
ELECTRICAL	[illegible]	[illegible]
ICT	[illegible]	[illegible]
ADDITIONAL DISCIPLINES TO BE ADDED AS REQUIRED		

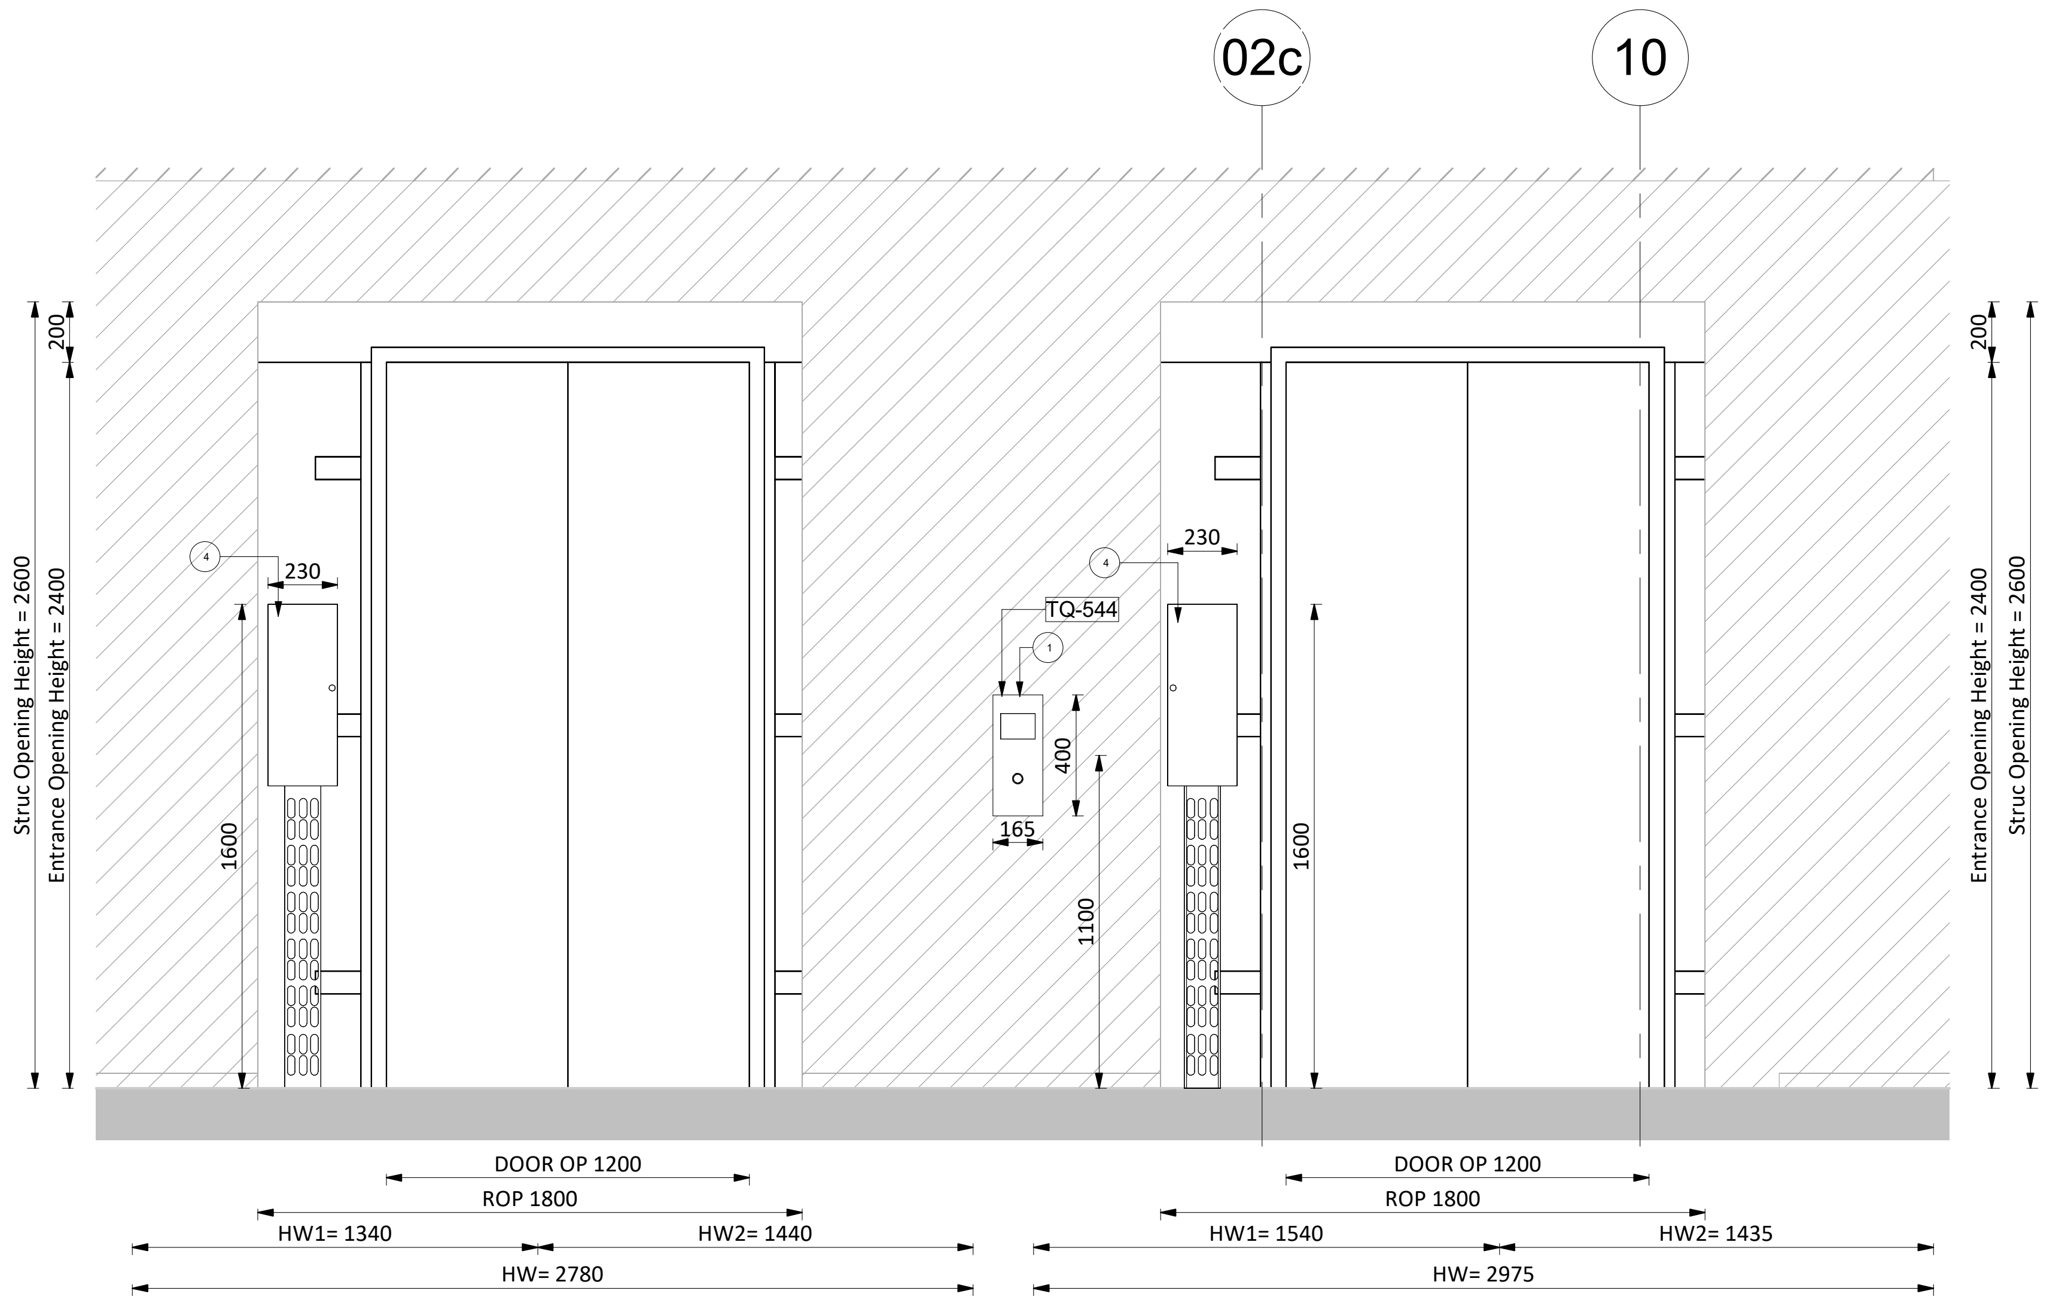
02c
10
200
Struc Opening Height = 2600
Entrance Opening Height = 2400
230
1600
TQ-544
230
400
165
1100
1600
Entrance Opening Height = 2400
Struc Opening Height = 2600
DOOR OP 1200
ROP 1800
HW1= 1340
HW2= 1440
HW= 2780
DOOR OP 1200
ROP 1800
HW1= 1540
HW2= 1435
HW= 2975

4 Door Elevation At "2" Floor (REAR) - ELEV -L13 & L14

1 : 25

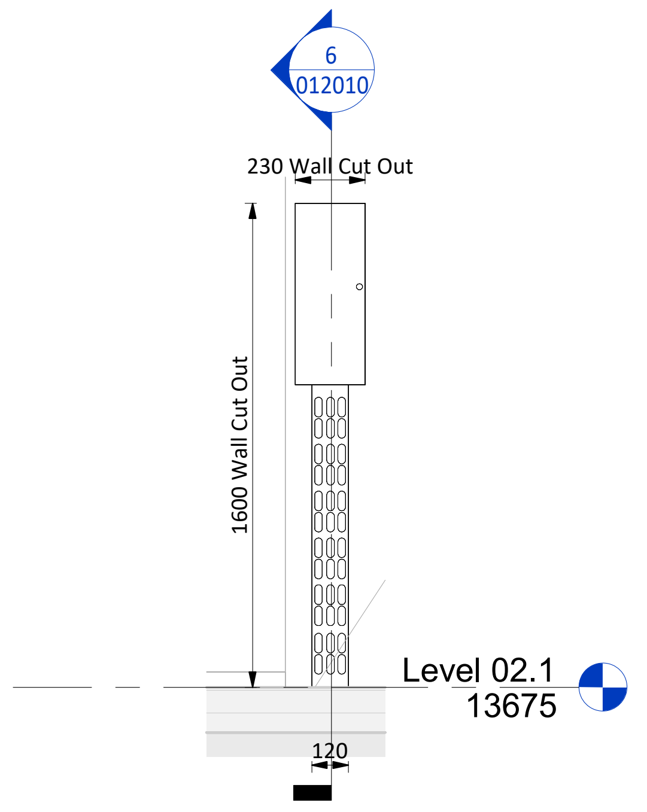
6
012010
230 Wall Cut Out
1600 Wall Cut Out
Level 02.1
13675
120

5 E&I SPOT DETAIL - ELEV -L13 & L14

1 : 25

CONTROLLED COPY
MBL IFC
JEDDAH OPERA HOUSE PROJECT
QA/QC Department
MBL QAM
Engr. Mudassar Altaf

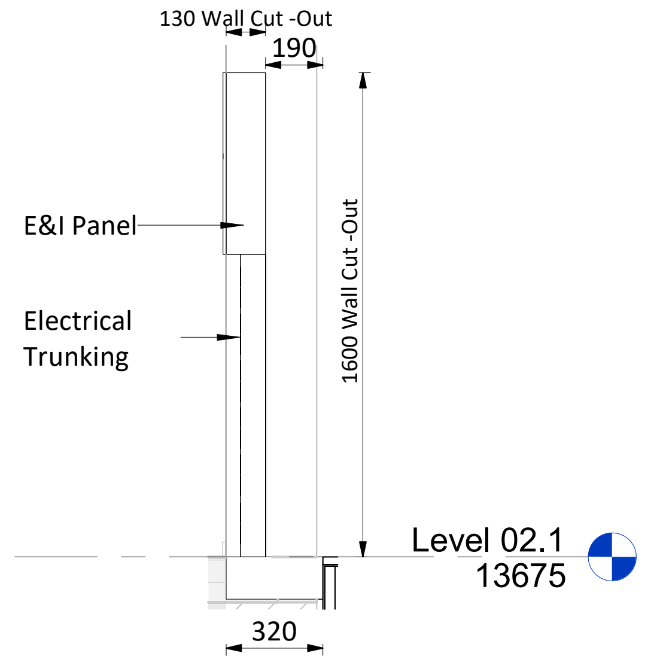
130 Wall Cut -Out
190
E&I Panel
Electrical Trunking
1600 Wall Cut -Out
Level 02.1
13675
320

6 Cross-Section View B-B - ELEV -L13 & L14

1 : 25

SCEC – K&A Reviewed

Civil ☐
Arch. ☐
Elec. ☒
ELV. ☐
Mech. ☒
Acoustic ☒

SCEC – K&A Reviewed
Code B – Approved with Comments
(Do not Resubmit)

Duplex Units

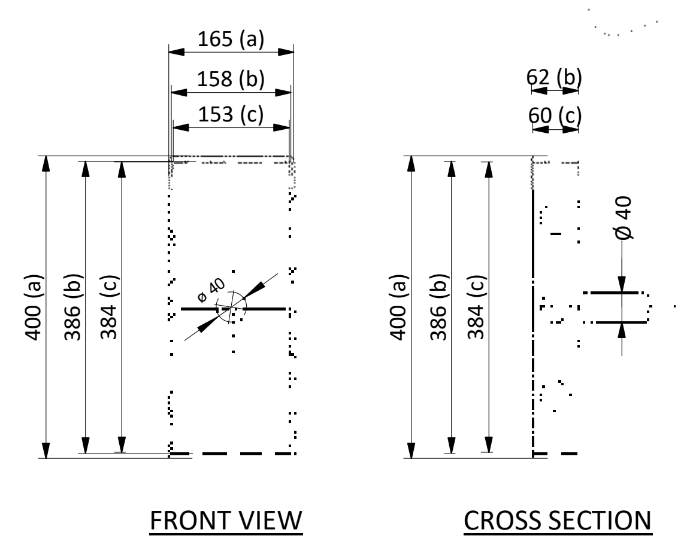
165 (a)
158 (b)
153 (c)
400 (a)
386 (b)
384 (c)
ø 40
62 (b)
60 (c)
400 (a)
386 (b)
384 (c)
ø 40

FRONT VIEW

CROSS SECTION

PUSH BUTTON

(a) FACE PLATE:400(L)x 165 (w)
(b) CONCRETE OPENING: 386 (L) x 158 (w) X 62 (D)
(c) Back BOX: 384(L) X 153(W) x 60(D)

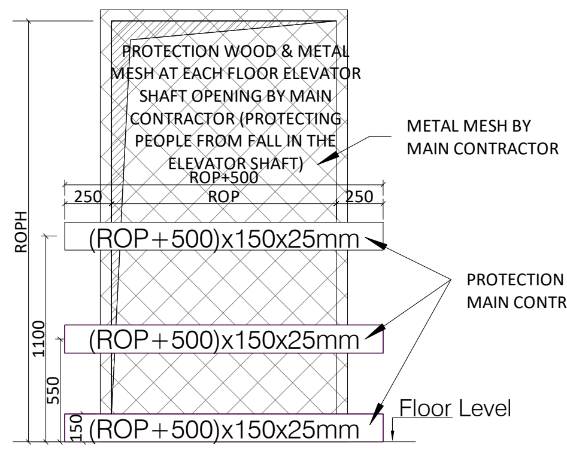
PROTECTION WOOD & METAL MESH AT EACH FLOOR ELEVATOR SHAFT OPENING BY MAIN CONTRACTOR (PROTECTING PEOPLE FROM FALL IN THE ELEVATOR SHAFT)
ROP+500
250
ROP
250
METAL MESH BY MAIN CONTRACTOR
(ROP+500)x150x25mm
(ROP+500)x150x25mm
(ROP+500)x150x25mm
PROTECTION WOOD BY MAIN CONTRACTOR
Floor Level
ROPH
1100
550
150

Protection Elevation Detail
At Each Elevator Shaft Opening

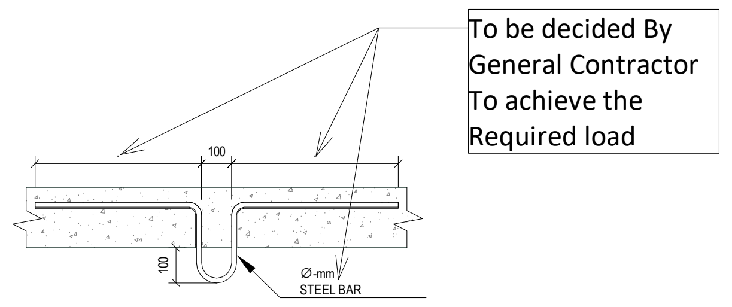
100
100
Ø-mm STEEL BAR

To be decided By General Contractor To achieve the Required load

Hook Fixation Detail

Hooks Design,Supply & Install By Main Contractor

LEGEND	
HW	HOIST WAY WIDTH
HD	HOIST WAY DEPTH
CRH	CAR ROUGH HEIGHT
DOOR OP	DOOR OPENING
ROP	ROUGH OPENING
CW	CAR WIDTH
CD	CAR DEPTH
CH	CAR HEIGHT
DBG	DISTANCE BETWEEN GUARDRAIL
CWT	COUNTERWEIGHT
E&I PANEL	EMERGENCY & INSPECTION PANEL
G.O.V	CAR GOVERNOR
COP	CAR OPERATING PANEL
HBP	HALL POSITION INDICATOR

REV	DATE	BY	DESCRIPTION	CHK	APD
S01	16-APR-2026	AK	Shop Drawing	NA	SS
S00	15-APR-2026	AK	Issued for Approval	NA	SS

DRAWING STATUS:
CONSTRUCTION SHOPDRAWING

CLIENT: شركة وسط جدة للتطوير Jeddah Central Development Co.

LEAD DESIGN CONSULTANTS: Henning Larsen

LEAD ENGINEERING CONSULTANT: BURO HAPPOLD

PROJECT SUPERVISION CONSULTANT: KHATIB & ALAMI

GENERAL CONTRACTOR: MBL

REVIEWER: dar

SUB CONTRACTOR: OTIS ELEVATOR COMPANY SAUDI ARABIA LIMITED OTIS

PROJECT: JEDDAH OPERA HOUSE

TITLE:
OPERA BUILDING
VERTICAL TRANSPORTATION
PART 003
ELEVATIONS - LIFT SHAFT (L13 & L14)

SCALE @ A1:	CHECKED:		APPROVED:
As indicated	Salma Sakr		Ali Basit
PROJECT No:	DESIGNED:	DRAWN:	DATE:
440014	Abdul Kafoor	Pranoti	16-APR-2026

DRAWING No: JOH-OTS-S5-01-056-003-ZZ-SD-VT-012010
REV: S01

MODEL FILE REF: JOH-OTS-S5-01-056-XXX-ZZ-M3-VT-010001

© JCDC

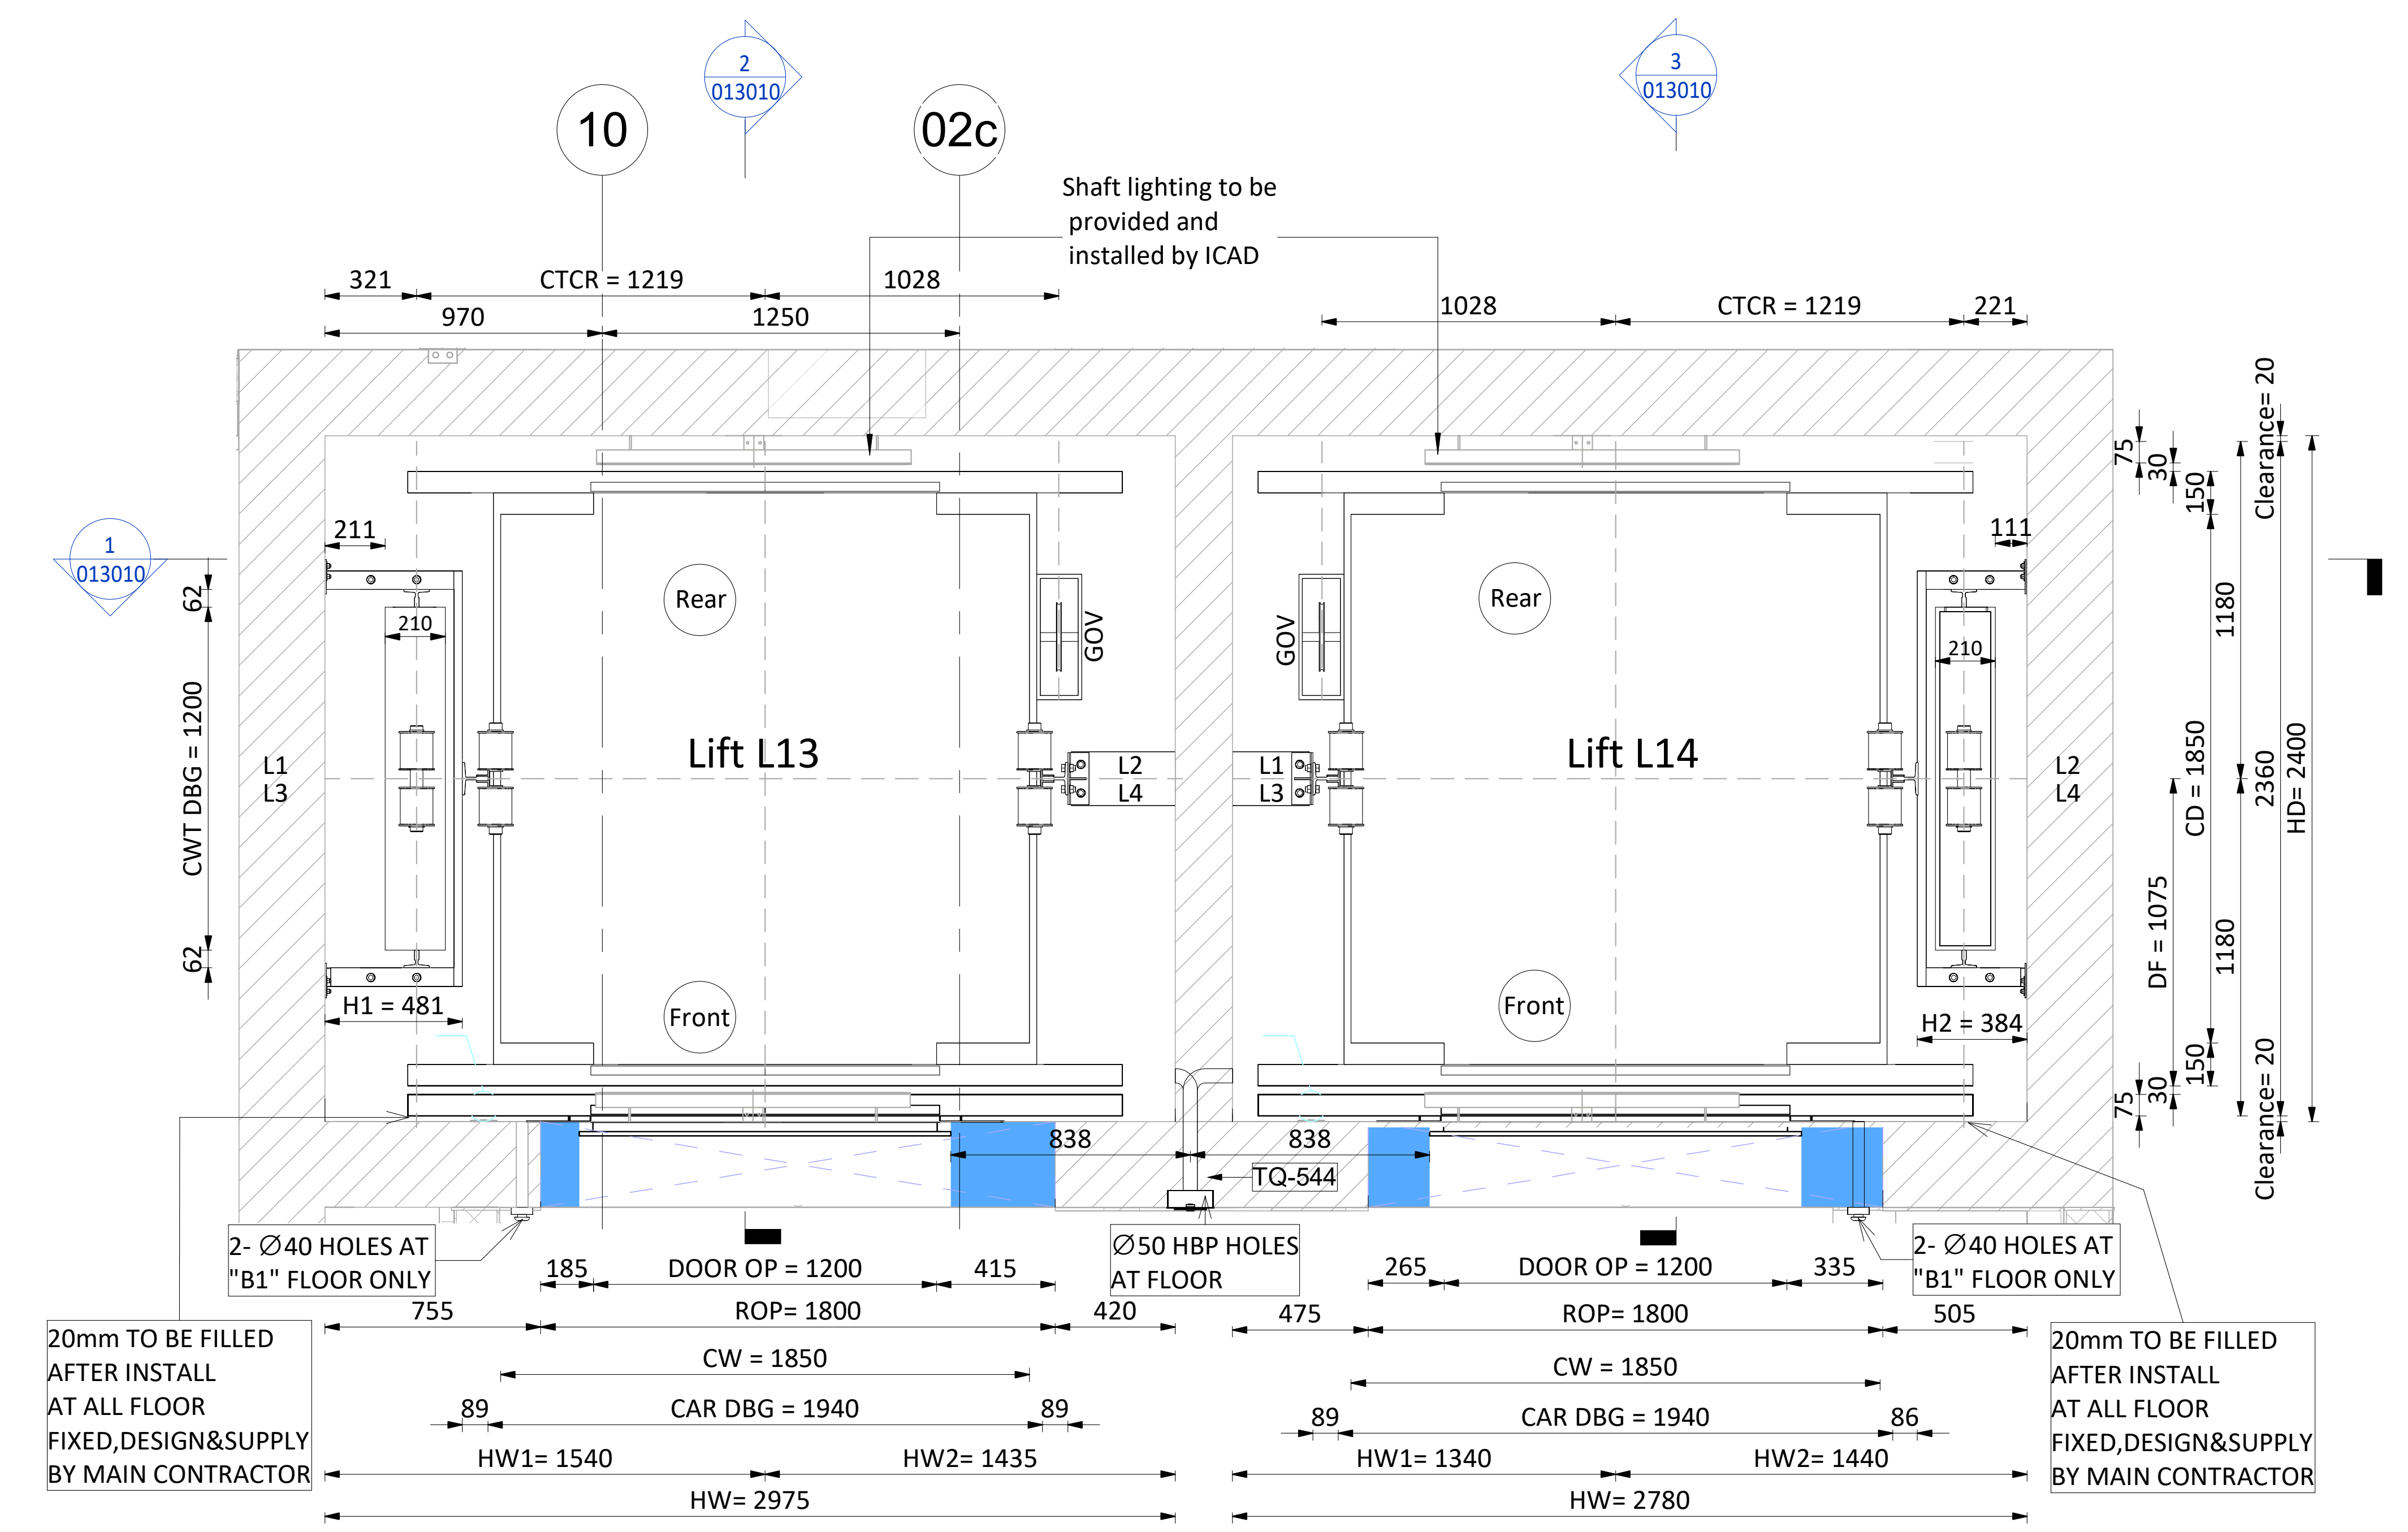
10
02c
2 013010
3 013010
1 013010
Shaft lighting to be provided and installed by ICAD
321
970
CTCR = 1219
1250
1028
1028
CTCR = 1219
221
211
210
Rear
GOV
Lift L13
Lift L14
L1 L3
L2 L4
111
CWT DBG = 1200
62
H1 = 481
H2 = 384
Front
838
TQ-544
2- Ø40 HOLES AT "B1" FLOOR ONLY
Ø50 HBP HOLES AT FLOOR
185
DOOR OP = 1200
415
265
335
755
ROP= 1800
420
475
505
CW = 1850
89
CAR DBG = 1940
86
HW1= 1540
HW2= 1435
HW1= 1340
HW2= 1440
HW= 2975
HW= 2780
20mm TO BE FILLED AFTER INSTALL AT ALL FLOOR FIXED,DESIGN&SUPPLY BY MAIN CONTRACTOR
75
30
150
Clearance= 20
1180
CD = 1850
DF = 1075
2360
HD= 2400

1 Hoist Way Plan At "G" Floor (FRONT) - ELEV -L13 & L14

1 : 25

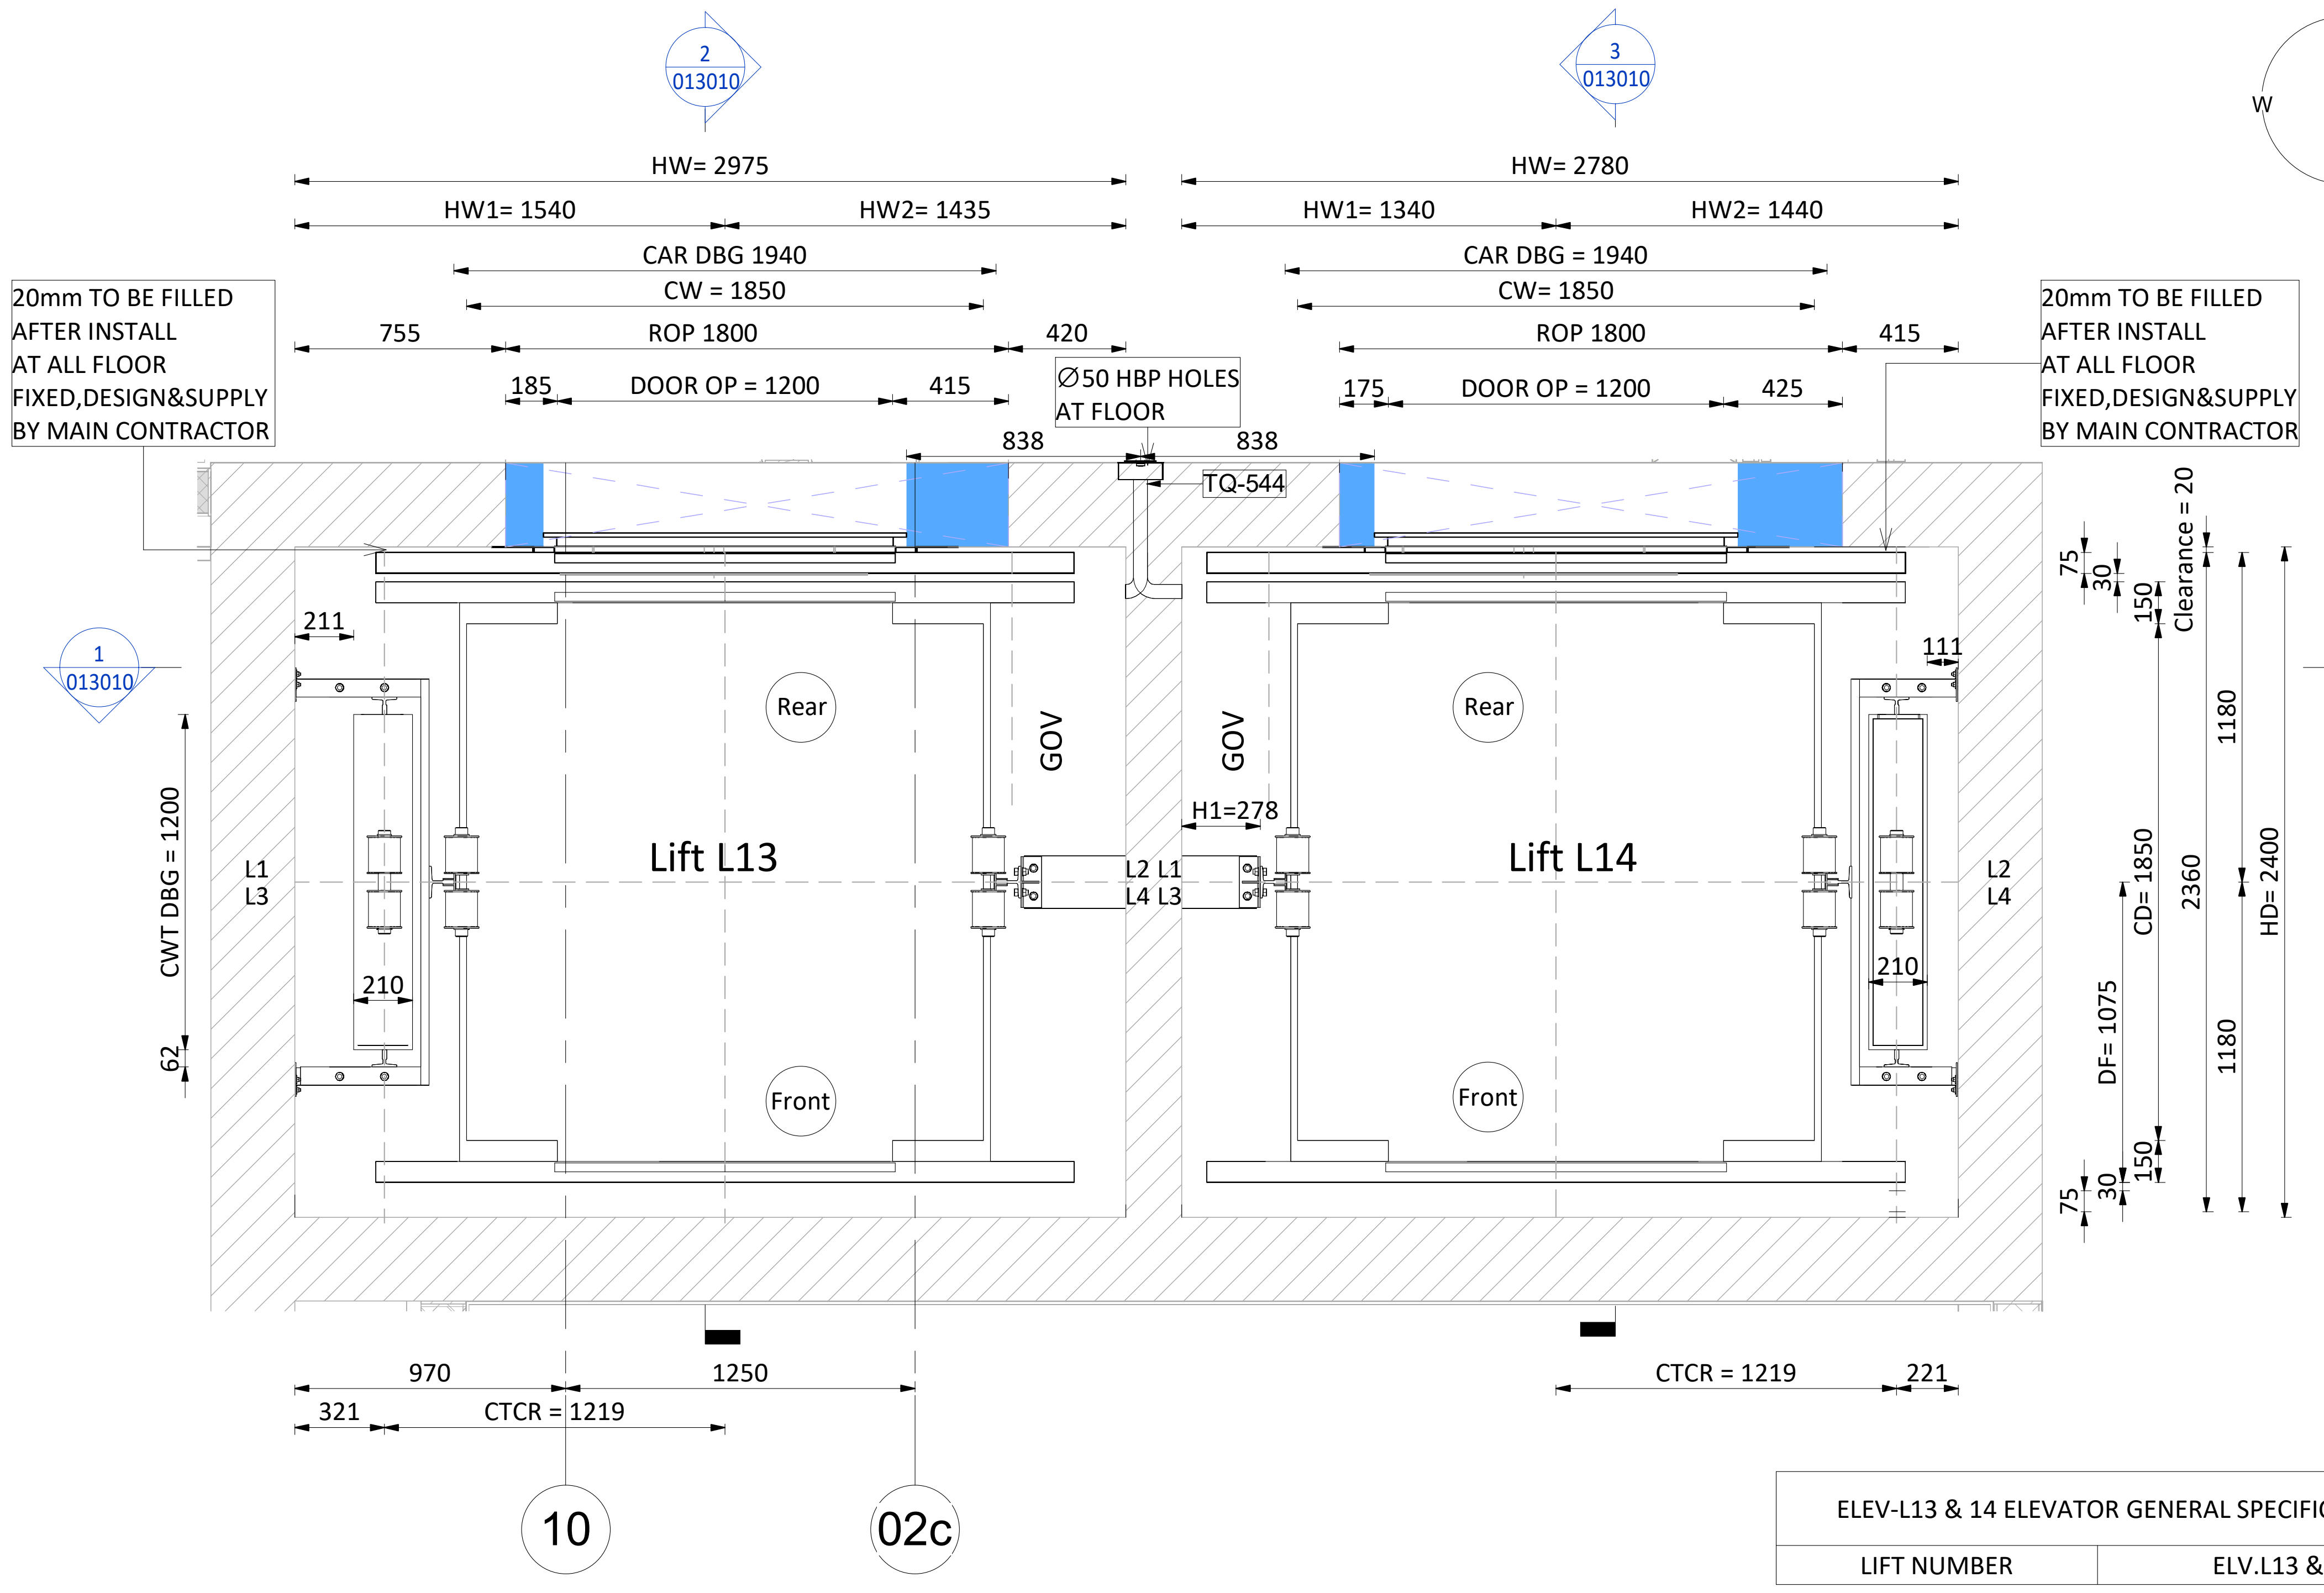
2 013010
3 013010
1 013010
HW= 2975
HW1= 1540
HW2= 1435
HW= 2780
HW1= 1340
HW2= 1440
CAR DBG 1940
CAR DBG = 1940
CW = 1850
755
ROP 1800
420
ROP 1800
415
185
DOOR OP = 1200
415
175
425
Ø50 HBP HOLES AT FLOOR
838
TQ-544
20mm TO BE FILLED AFTER INSTALL AT ALL FLOOR FIXED,DESIGN&SUPPLY BY MAIN CONTRACTOR
211
210
Rear
GOV
H1=278
Lift L13
Lift L14
L1 L3
L2 L4
111
CWT DBG = 1200
62
Front
75
30
150
Clearance = 20
1180
CD= 1850
DF= 1075
2360
HD= 2400
970
1250
321
CTCR = 1219
221
10
02c

2 Hoist Way Plan At "1" Floor (REAR) - ELEV -L13 & L14

1 : 25

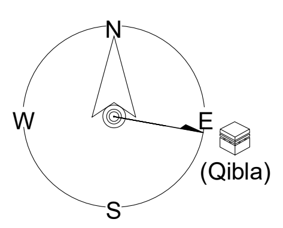

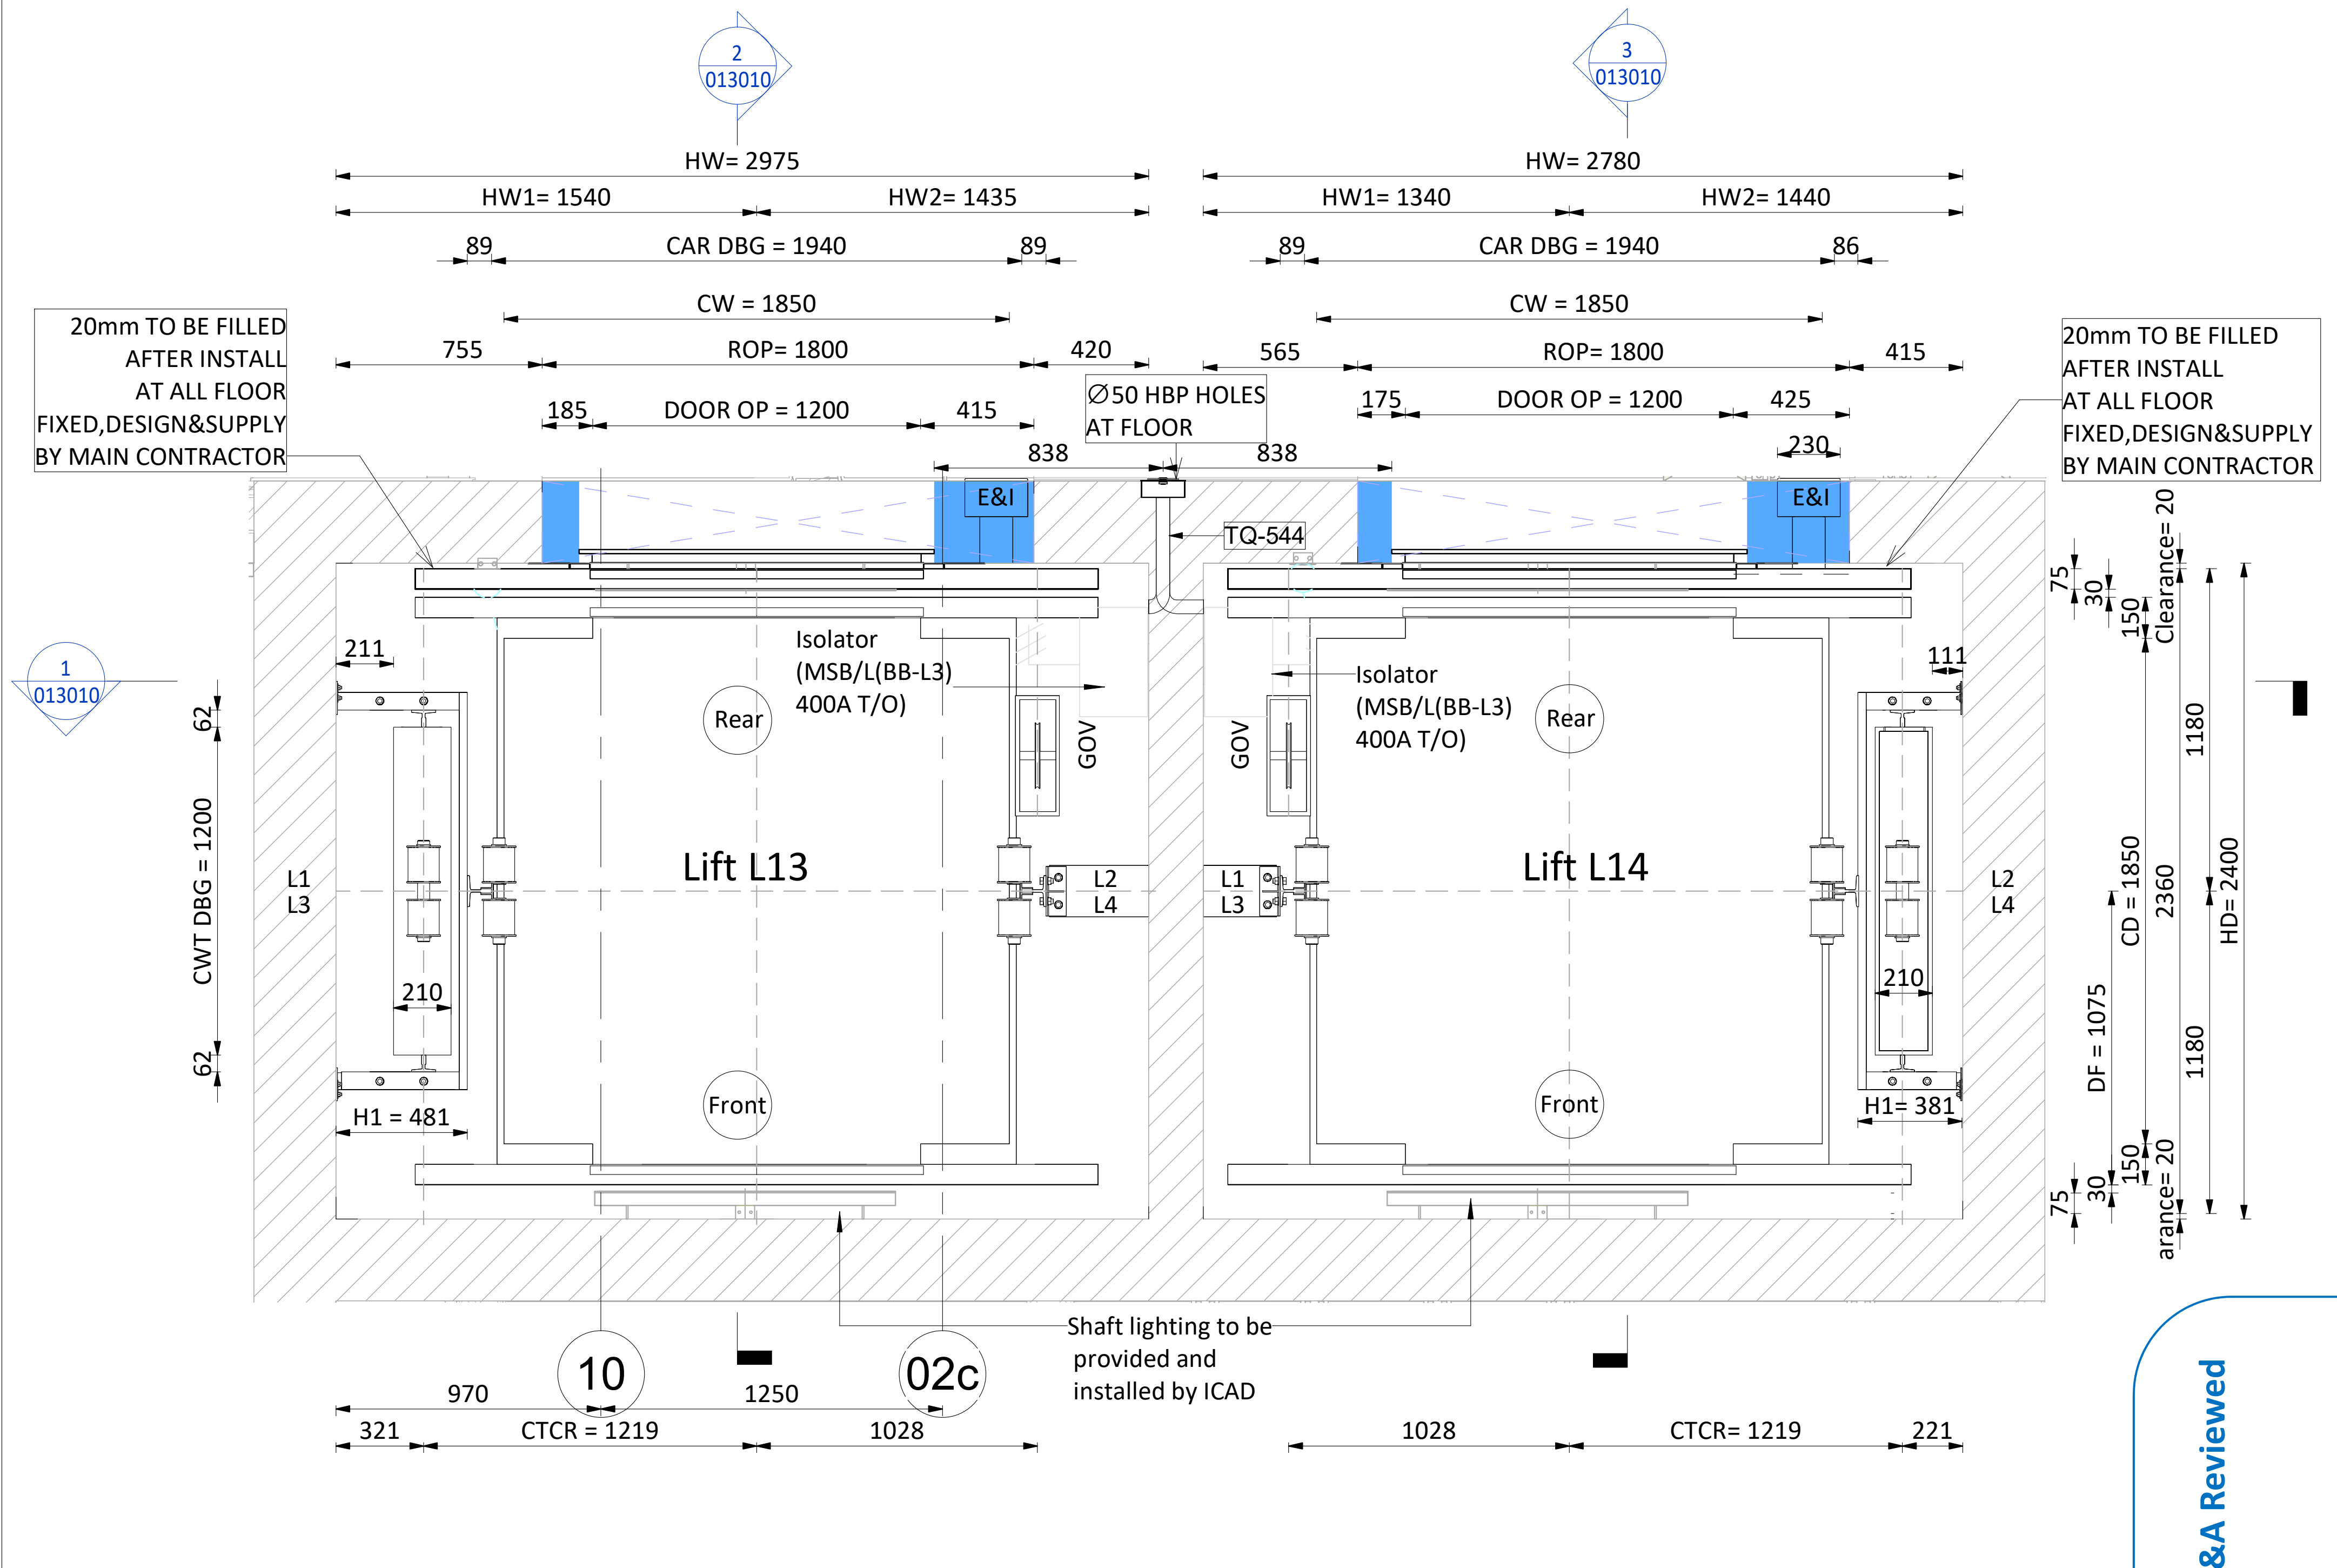
2 013010
3 013010
1 013010
HW= 2975
HW1= 1540
HW2= 1435
HW= 2780
HW1= 1340
HW2= 1440
89
CAR DBG = 1940
86
CW = 1850
755
ROP= 1800
420
565
415
185
DOOR OP = 1200
175
425
Ø50 HBP HOLES AT FLOOR
838
230
E&I
TQ-544
20mm TO BE FILLED AFTER INSTALL AT ALL FLOOR FIXED,DESIGN&SUPPLY BY MAIN CONTRACTOR
211
210
Isolator (MSB/L(BB-L3) 400A T/O)
Rear
GOV
Lift L13
Lift L14
L1 L3
L2 L4
111
CWT DBG = 1200
62
H1 = 481
H1= 381
Front
75
30
150
Clearance= 20
1180
CD = 1850
DF = 1075
2360
HD= 2400
10
02c
Shaft lighting to be provided and installed by ICAD
970
1250
321
CTCR = 1219
1028
1028
CTCR= 1219
221

3 Hoist Way Plan At "2" Floor (REAR) - ELEV -L13 & L14

1 : 25

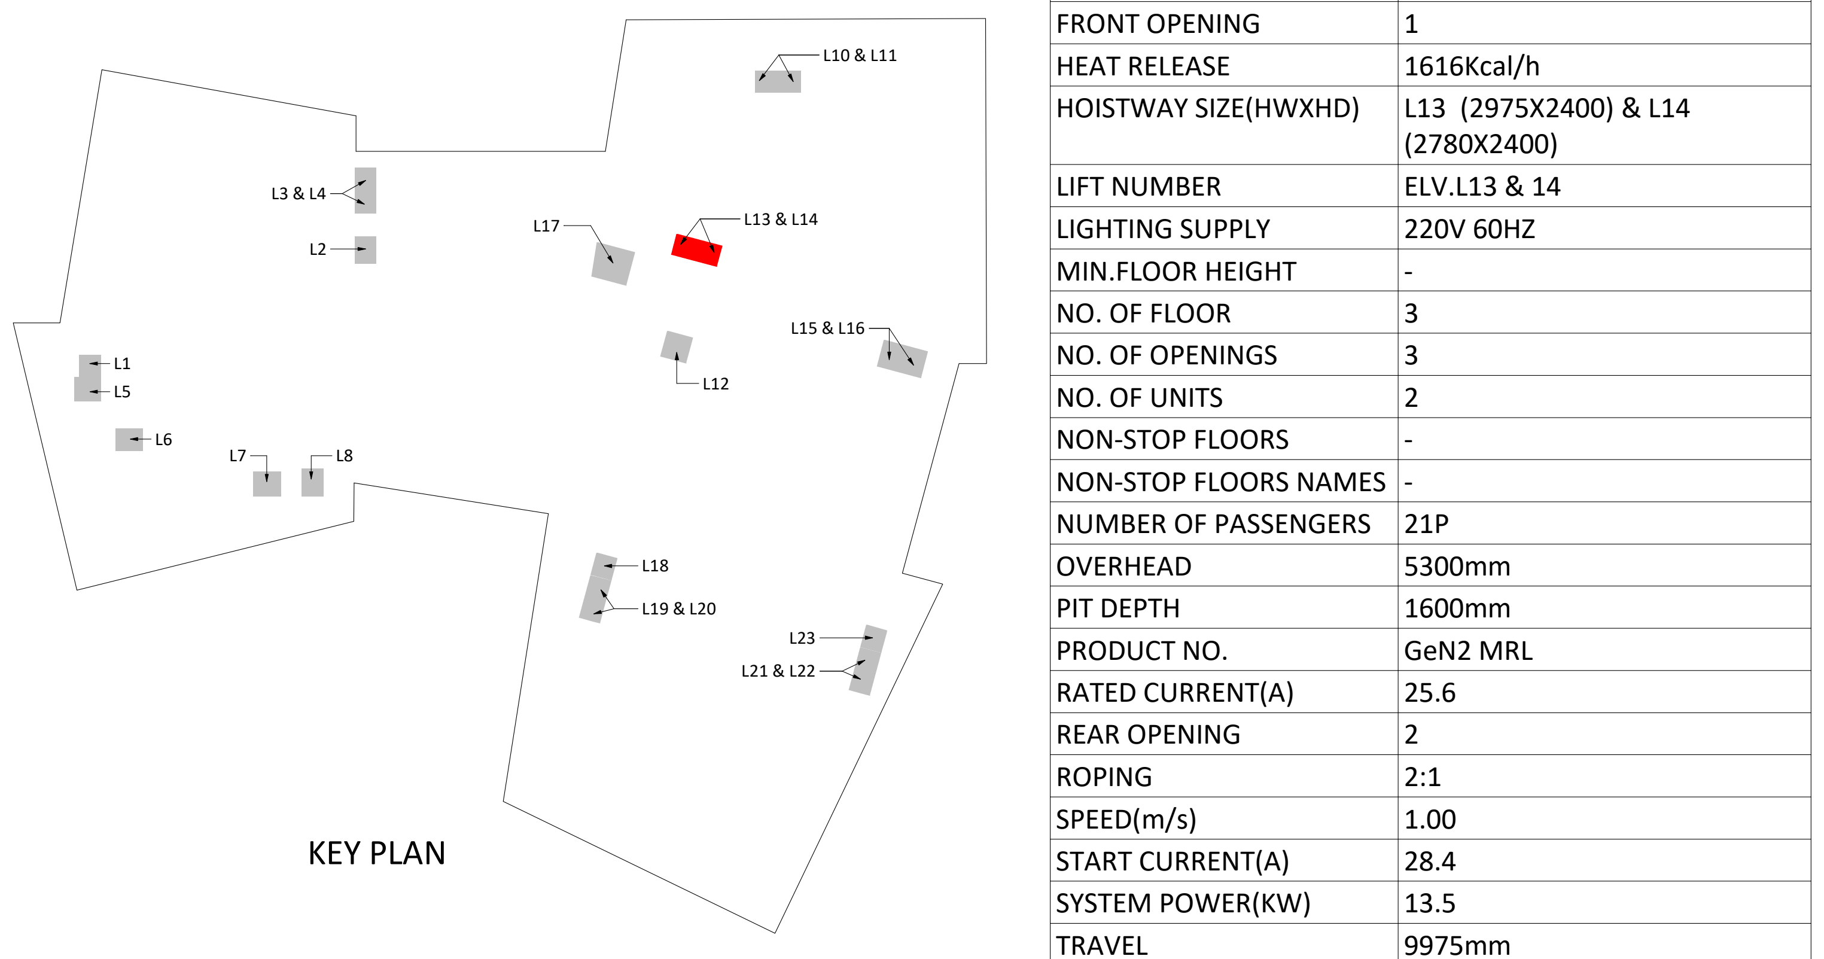
L10 & L11
L3 & L4
L2
L17
L13 & L14
L15 & L16
L12
L1
L5
L6
L7
L8
L18
L19 & L20
L23
L21 & L22

KEY PLAN

CONTROLLED COPY
MBL IFC
JEDDAH OPERA HOUSE PROJECT
QA/QC Department

MBL QAM
Engr. Mudassar Altaf

SCEC – K&A Reviewed

Civil	Arch.	Elec.	ELV.	Mech.	Acoustic
☐	☐	☒	☐	☒	☒

SCEC – K&A Reviewed

Code B – Approved with Comments
(Do not Resubmit)

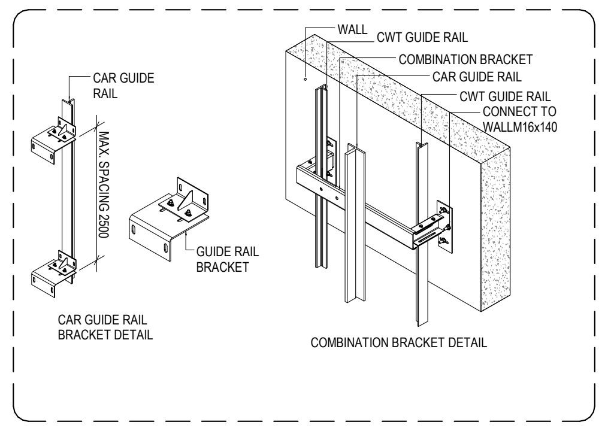
WALL
CWT GUIDE RAIL
COMBINATION BRACKET
CAR GUIDE RAIL
CWT GUIDE RAIL
CONNECT TO WALL(M16x140)
CAR GUIDE RAIL
GUIDE RAIL BRACKET
CAR GUIDE RAIL BRACKET DETAIL
COMBINATION BRACKET DETAIL

NOTE No.:
FRONT WALLS,FINISHES & ARCHITRAVES TO BE BUILT (BY CLIENT) AFTER THE INSTALLATION OF THE (LANDING) EXTERNAL DOORS.

IMPORTANT NOTE FOR MAIN CONTRACTOR.
FREEDOM OF ACCESS MUST BE AVAILABLE FOR POINT OF ENTRY INTO THE BUILDING UP TO THE ELEVATOR HOIST WAY AND THE FRONT WALLS OF THE HOIST WAY AT MAIN FLOOR TO BE LEFT OPEN FOR FULL WIDTH AND HEIGHT TO PERMIT ENTRY OF OUR EQUIPMENT.

ELEV-L13 & 14 ELEVATOR GENERAL SPECIFICATIONS	
LIFT NUMBER	ELV.L13 &L14

CABIN INTERNAL SIZE(WXDXH)	1850X1850X2600
CAPACITY	1600Kg
CLEAR ENTRANCE	1200X2400
CONTROL	VVVF
CONTROL SYSTEM	DUPLEX FULL COLLECTIVE
COUNTERWEIGHT SAFETY	NO
DOOR TYPE	CLD1
EMERGENCY EXITS	-
FRONT OPENING	1
HEAT RELEASE	1616Kcal/h
HOISTWAY SIZE(HWXHD)	L13 (2975X2400) & L14 (2780X2400)
LIFT NUMBER	ELV.L13 & 14
LIGHTING SUPPLY	220V 60HZ
MIN.FLOOR HEIGHT	-
NO. OF FLOOR	3
NO. OF OPENINGS	3
NO. OF UNITS	2
NON-STOP FLOORS	-
NON-STOP FLOORS NAMES	-
NUMBER OF PASSENGERS	21P
OVERHEAD	5300mm
PIT DEPTH	1600mm
PRODUCT NO.	GeN2 MRL
RATED CURRENT(A)	25.6
REAR OPENING	2
ROPING	2:1
SPEED(m/s)	1.00
START CURRENT(A)	28.4
SYSTEM POWER(KW)	13.5
TRAVEL	9975mm
USE	PASSENGER LIFT

REACTIONS FORCE (KN)

Car side rail	CWT guide rail	Pit reaction	
R= 41	R= 15	U= 165	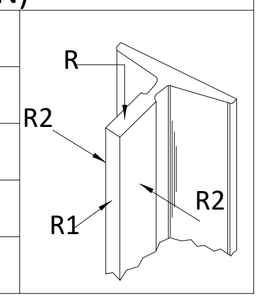
R1= 2.47	R1= 1.13	V= 132	
R2= 3.14	R2= 0.3		

LEGEND	
HW	HOIST WAY WIDTH
HD	HOIST WAY DEPTH
CRH	CAR ROUGH HEIGHT
DOOR OP	DOOR OPENING
ROP	ROUGH OPENING
CW	CAR WIDTH
CD	CAR DEPTH
CH	CAR HEIGHT
DBG	DISTANCE BETWEEN GUARDRAIL
CWT	COUNTERWEIGHT
E&I PANEL	EMERGENCY & INSPECTION PANEL
G.O.V	CAR GOVERNOR
COP	CAR OPERATING PANEL
HBP	HALL POSITION INDICATOR

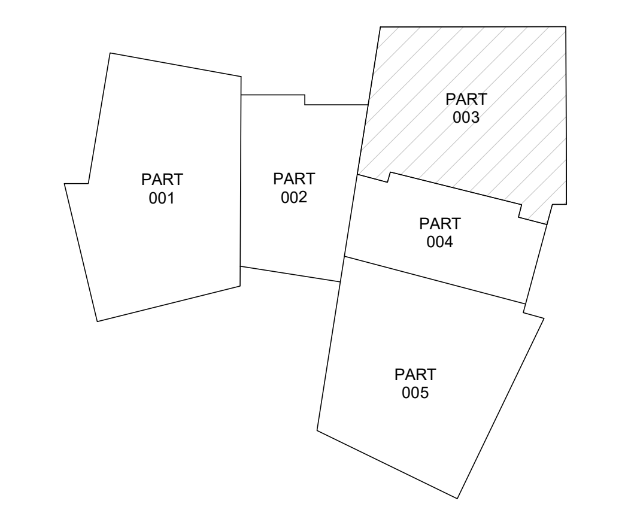
PART 001
PART 002
PART 003
PART 004
PART 005

KEY PLAN

GENERAL NOTES: ALL LEVELS SHOWN ON THE DRAWING ARE CHART DATUM LEVELS PROJECT LEVEL+0.000 = +3.700 CHART DATUM.

Dar Al-Handasah consultants (Shair and Partners)
Checked and Reviewed
Refer to CRS : SD-OPE-MBL-JCDC-01478

For ELE Panels distribution and Connection
Refer to (JOH-ICD-S5-01-056-003-02-SD-EL-011623)

DRAWING / DOCUMENT REFERENCE

NO.	NUMBER	TITLE	REV.
01	L-13 & L-14	JOH-HLA-S4-01-056-XXX-02-DR-AR-011120	F00
02		JOH-BHC-S4-01-056-XXX-XX-DR-VT-015001	
03		JOH-BHC-S4-01-056-XXX-XX-DR-VT-010001	
04		JOH-BHC-S4-01-056-005-ZZ-DR-VT-013001	
05		JOH-BHC-S4-01-056-005-ZZ-DR-VT-011001	
06		TQ-OPE-MBL-JCDC-00952	
07		TQ-OPE-MBL-JCDC-00544	
08		TQ-OPE-MBL-JCDC-00222	
09		TQ-OPE-MBL-JCDC-01052	
10		JCD-OPE-MBL-MR-003-NMR-601-03	
11		JCD-OPE-MBL-MR-003-NMR-602-01	

REVIEWED BY DISCIPLINE	SIGNATURE	DATE
ARCHITECTURAL	[illegible]	[illegible]-04-22
STRUCTURAL	[illegible]	[illegible]
MECHANICAL	ShA	2026-04-22
PLUMBING	ShA	2026-04-22
ELECTRICAL	[illegible]	[illegible]
ICT	[illegible]	[illegible]
ADDITIONAL DISCIPLINES TO BE ADDED AS REQUIRED		

REV	DATE	BY	DESCRIPTION	CHK	APD
S01	16-APR-2026	AK	Shop Drawing	NA	SS
S00	15-APR-2026	AK	Issued for Approval	NA	SS

DRAWING STATUS:
CONSTRUCTION SHOPDRAWING

CLIENT:
Jeddah Central Development Co.

LEAD DESIGN CONSULTANTS: Henning Larsen

LEAD ENGINEERING CONSULTANT: BURO HAPPOLD

PROJECT SUPERVISION CONSULTANT: KHATIB & ALAMI

GENERAL CONTRACTOR: MBL

REVIEWER: dar

SUB CONTRACTOR: OTIS ELEVATOR COMPANY SAUDI ARABIA LIMITED OTIS

PROJECT
JEDDAH OPERA HOUSE

TITLE:
OPERA BUILDING
VERTICAL TRANSPORTATION
PART 003
PLANS - LIFT SHAFT SHEET 01 OF 02 (L13 & L14)

SCALE @ A1:	CHECKED:		APPROVED:
1:25	Salma Sakr		Ali Basit
PROJECT No:	DESIGNED:	DRAWN:	DATE:
440014	Abdul Kafoor	Pranoti	16-APR-2026

DRAWING No:
JOH-OTS-S5-01-056-003-ZZ-SD-VT-011010

REV:
S01

MODEL FILE REF:
JOH-OTS-S5-01-056-XXX-ZZ-M3-VT-010001

© JCDC

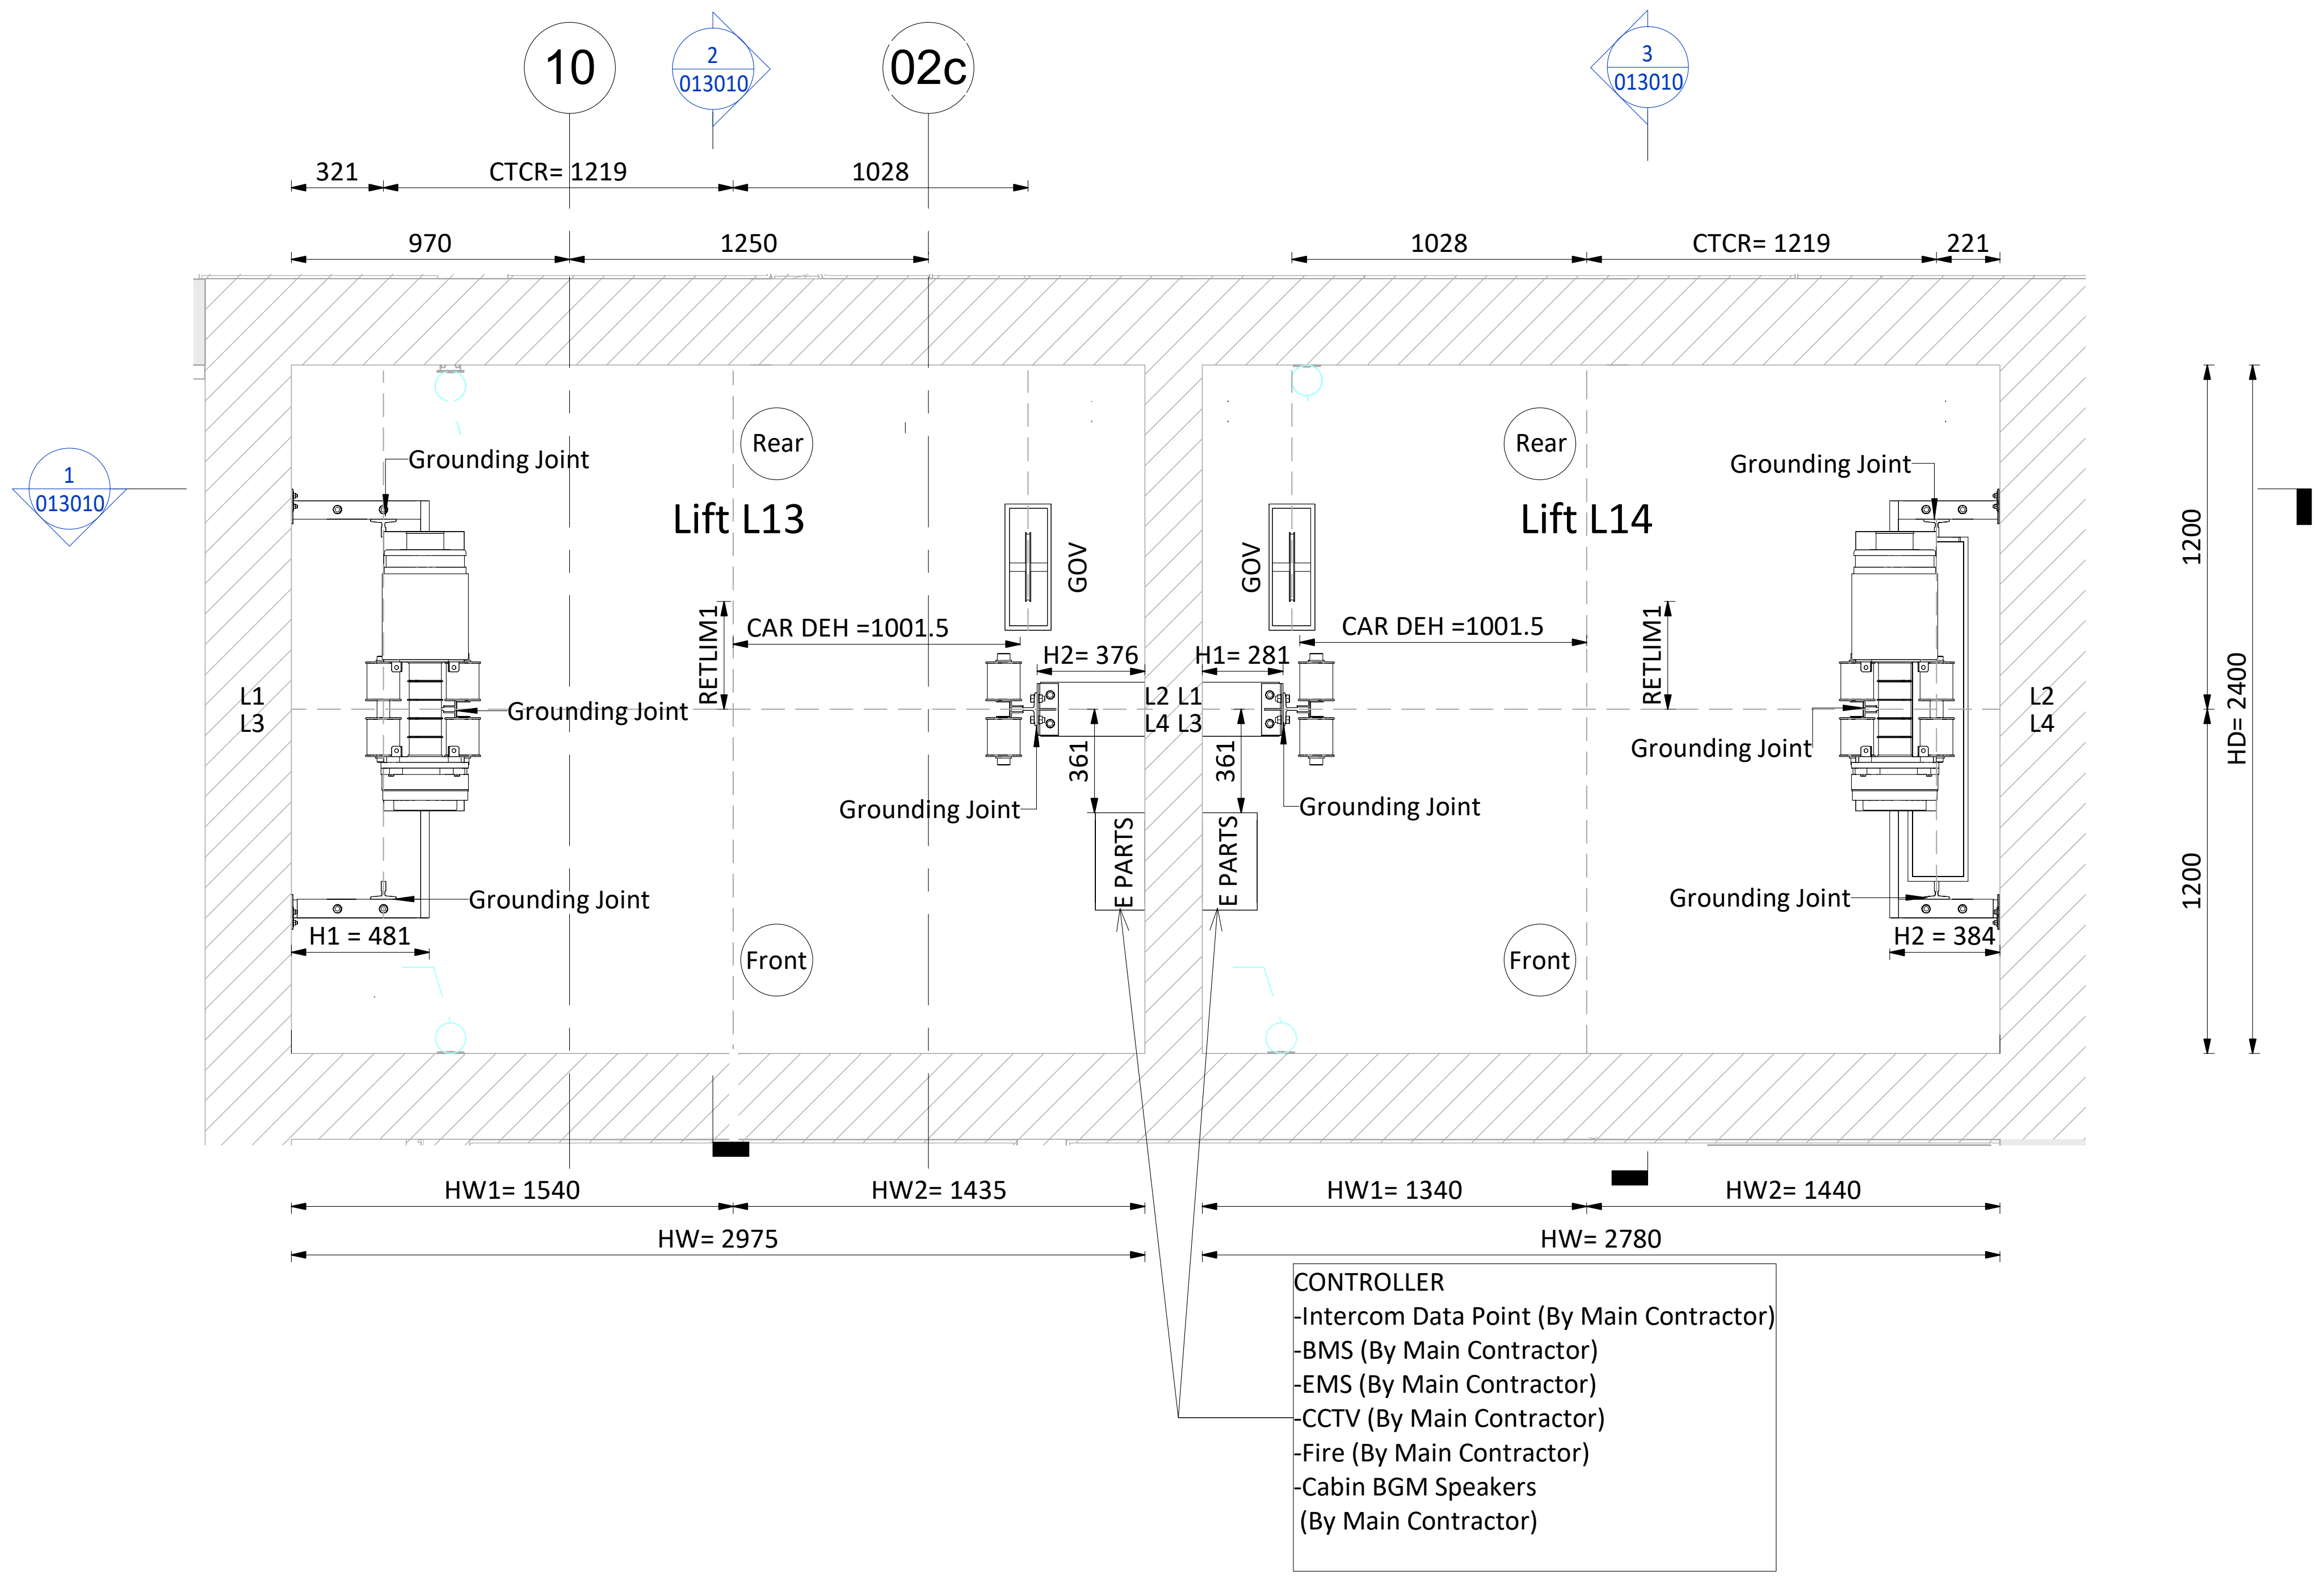
10
02c
2
013010
3
013010
1
013010
321
CTCR= 1219
1028
970
1250
1028
CTCR= 1219
221
Rear
Rear
Lift L13
Lift L14
Grounding Joint
Grounding Joint
Grounding Joint
Grounding Joint
Grounding Joint
Grounding Joint
Grounding Joint
Grounding Joint
GOV
GOV
RETLIM1
RETLIM1
CAR DEH =1001.5
CAR DEH =1001.5
H2= 376
H1= 281
L1
L3
L2 L1
L4 L3
L2
L4
361
361
E PARTS
E PARTS
H1 = 481
H2 = 384
Front
Front
1200
1200
HD= 2400
HW1= 1540
HW2= 1435
HW= 2975
HW1= 1340
HW2= 1440
HW= 2780
CONTROLLER
-Intercom Data Point (By Main Contractor)
-BMS (By Main Contractor)
-EMS (By Main Contractor)
-CCTV (By Main Contractor)
-Fire (By Main Contractor)
-Cabin BGM Speakers
(By Main Contractor)

1 Machine Plan Level - ELEV -L13 & L14

1 : 25

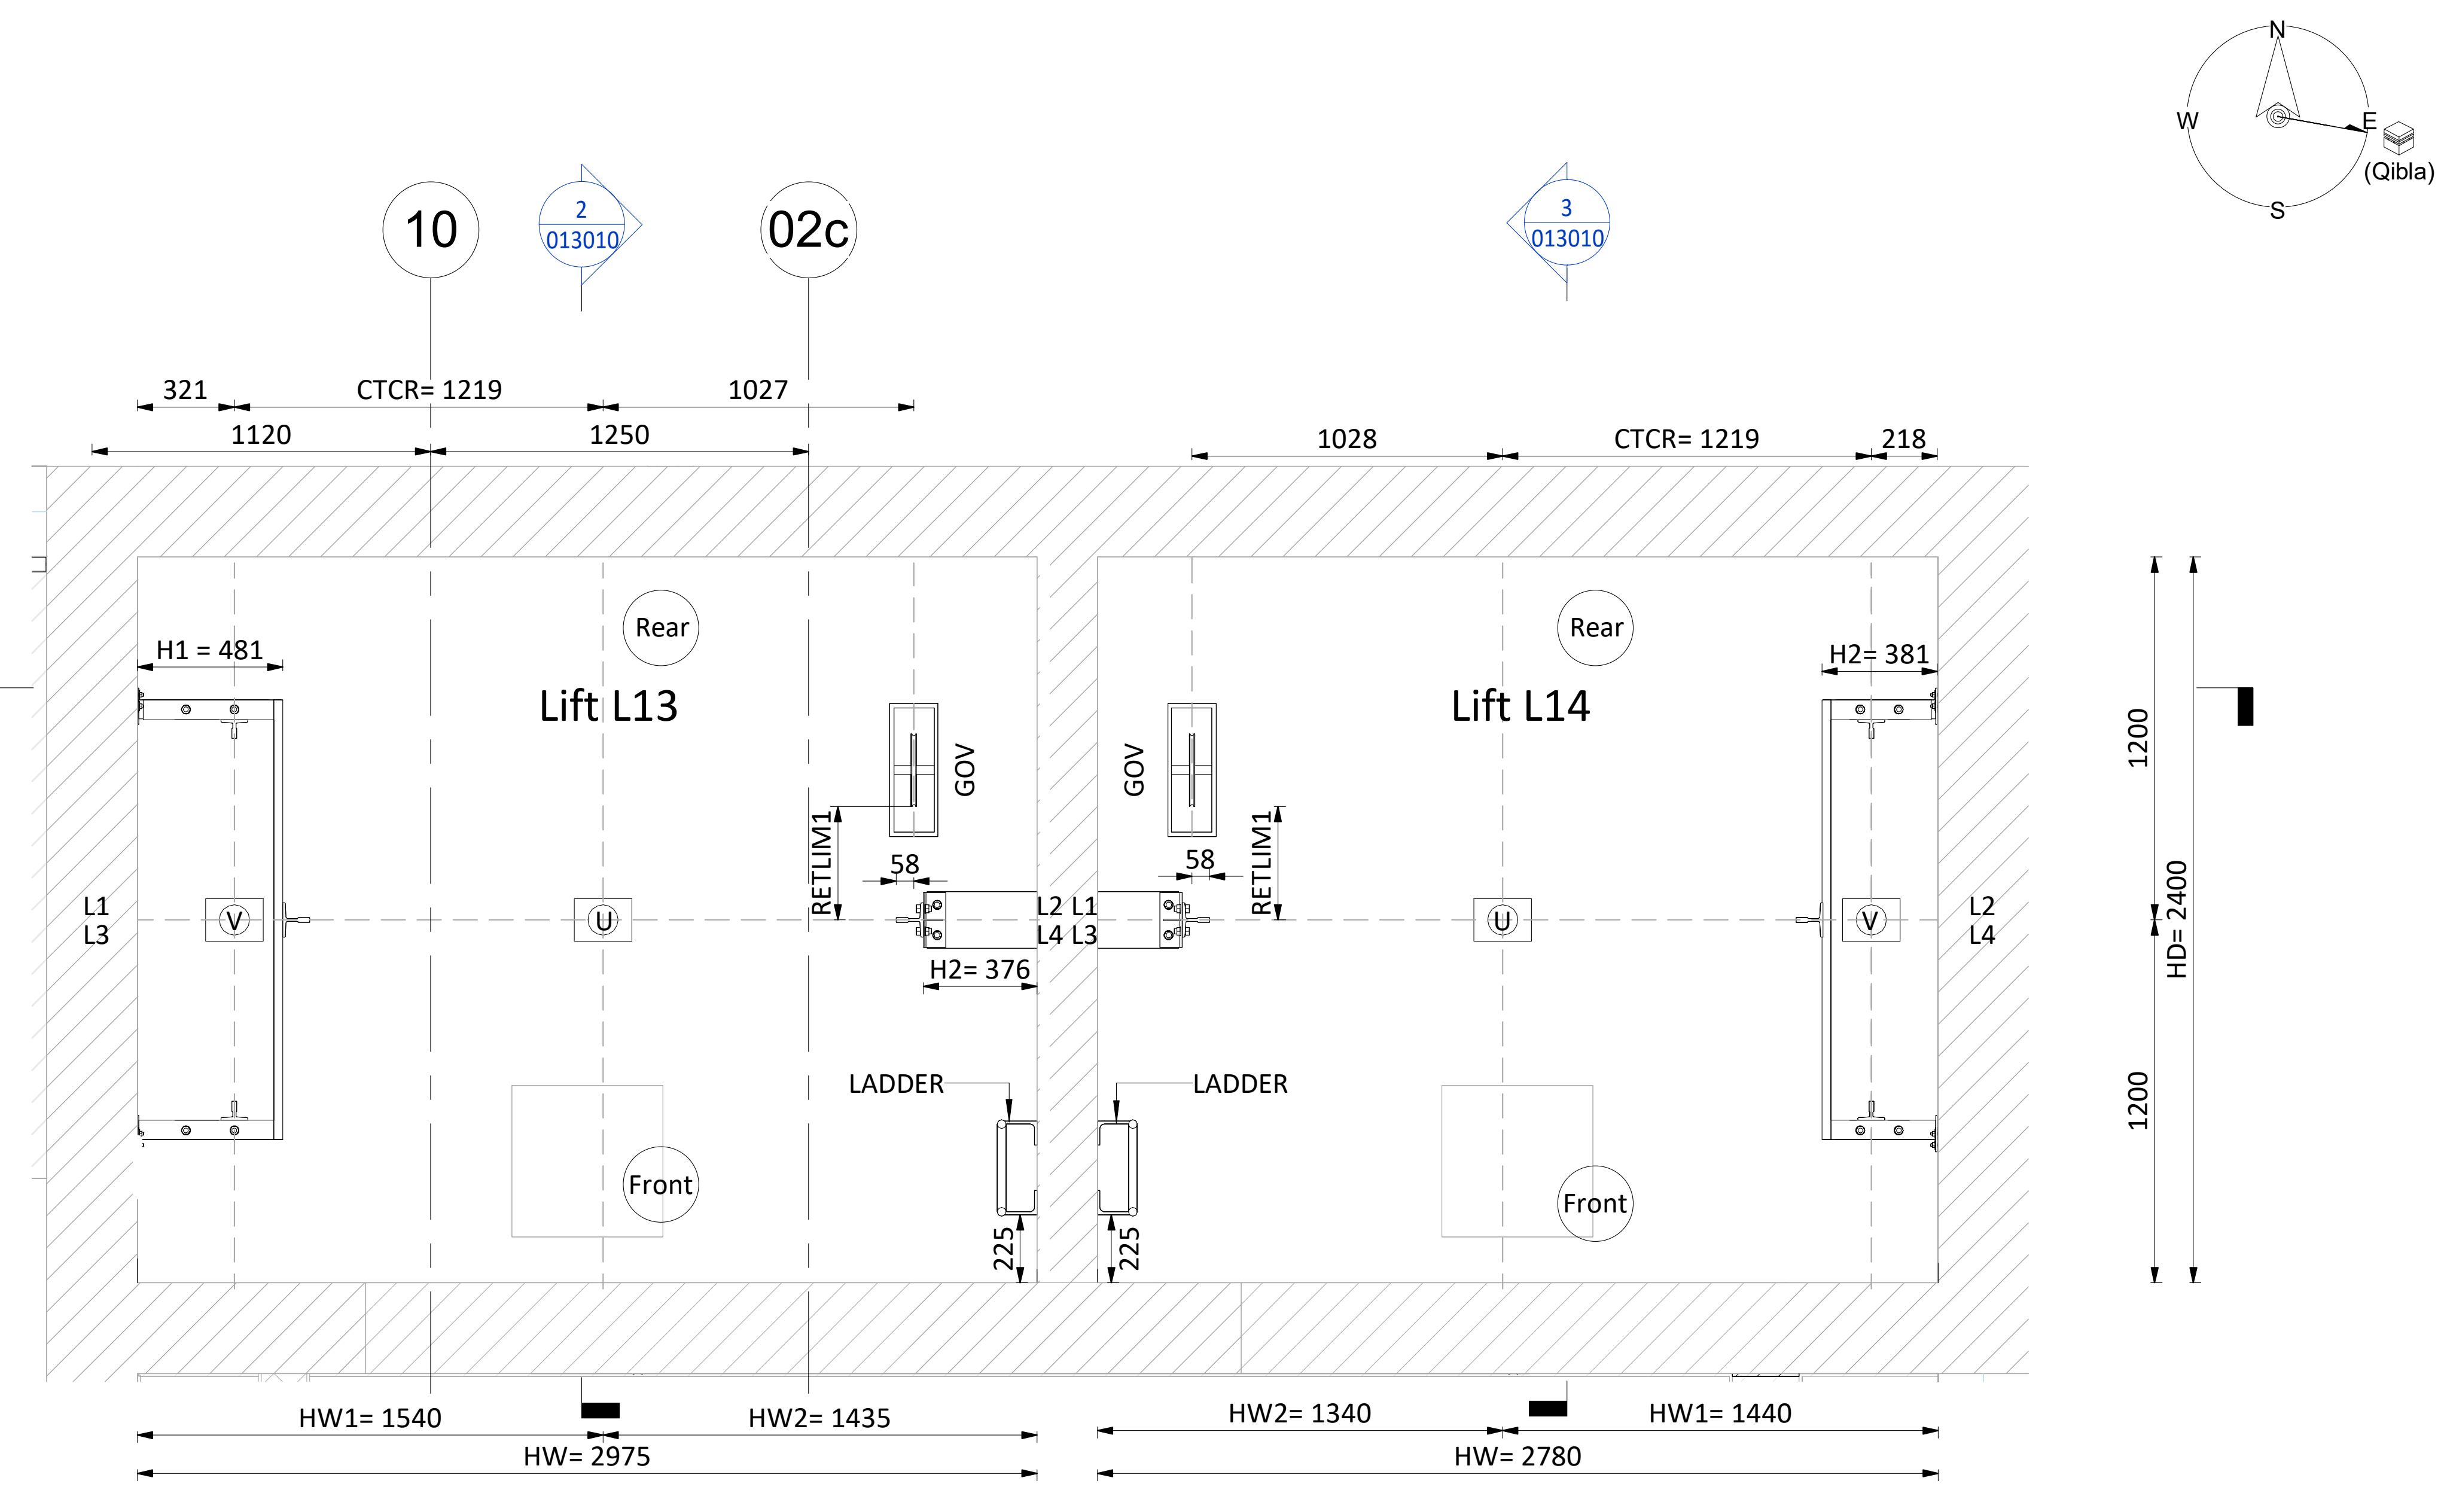
N
W
E
S
(Qibla)
10
02c
2
013010
3
013010
1
013010
321
CTCR= 1219
1027
1120
1250
1028
CTCR= 1219
218
Rear
Rear
Lift L13
Lift L14
H1 = 481
H2= 381
GOV
GOV
RETLIM1
RETLIM1
58
58
V
U
U
V
L1
L3
L2 L1
L4 L3
L2
L4
H2= 376
LADDER
LADDER
225
225
Front
Front
1200
1200
HD= 2400
HW1= 1540
HW2= 1435
HW= 2975
HW2= 1340
HW1= 1440
HW= 2780

2 Hoist Way Pit Plan - ELEV -L13 & L14

1 : 25

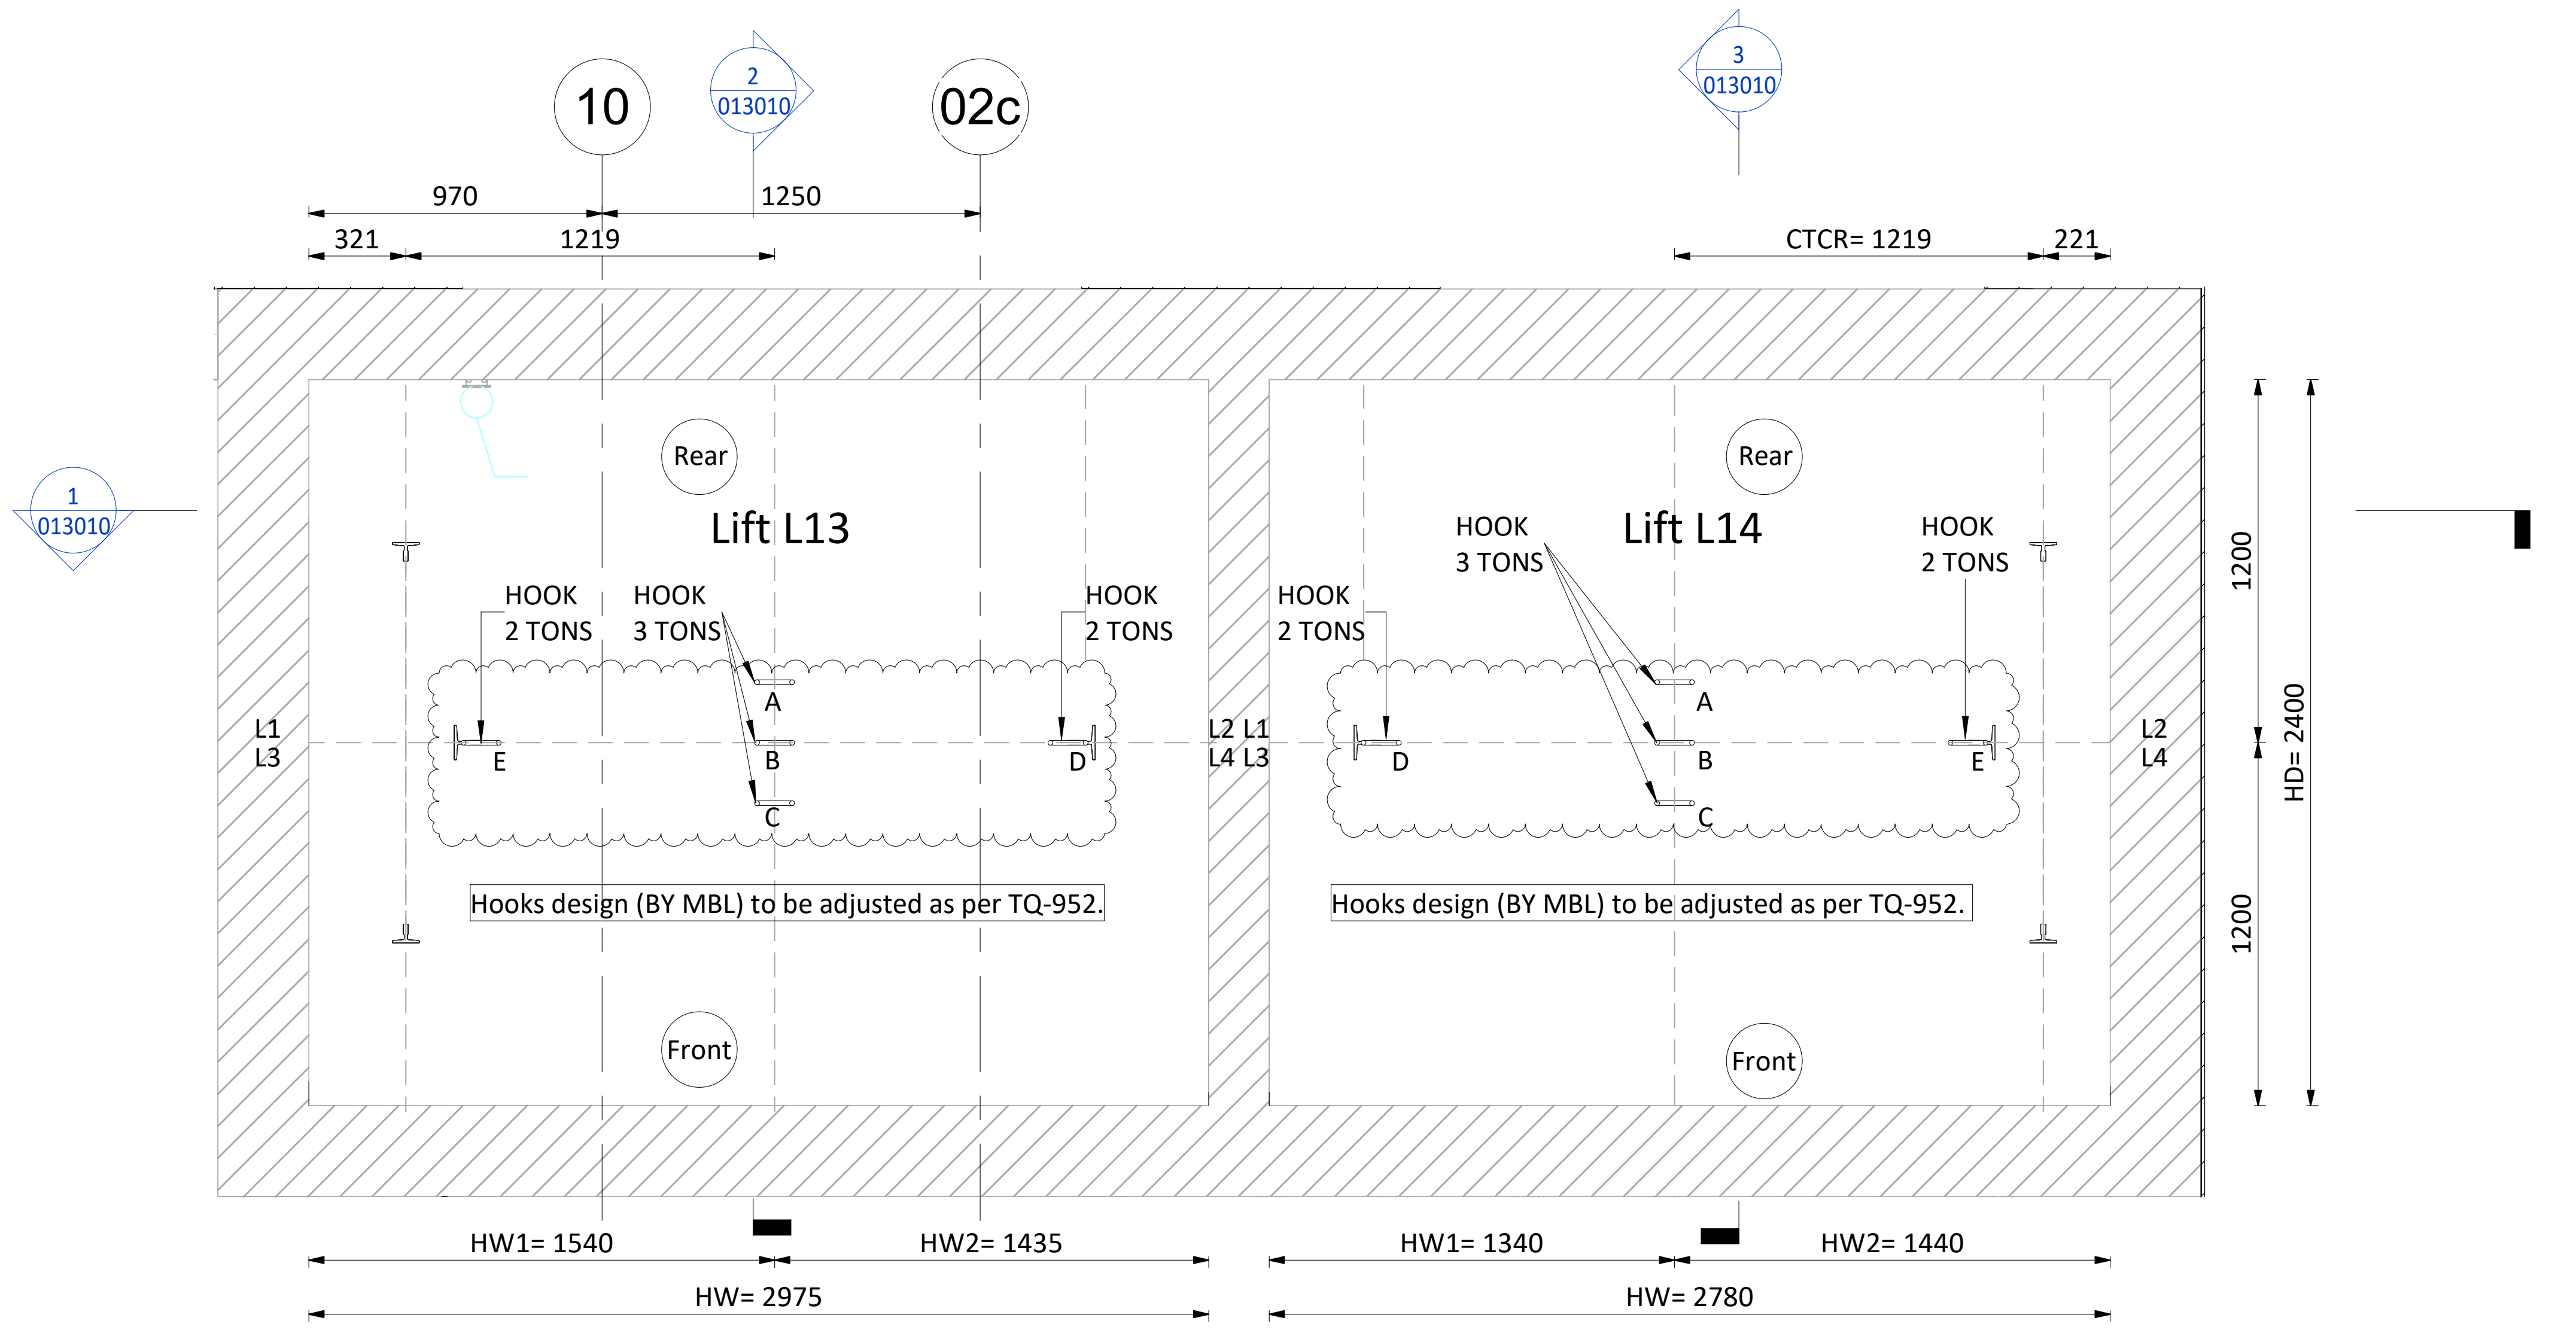
10
02c
2
013010
3
013010
1
013010
970
1250
321
1219
CTCR= 1219
221
Rear
Rear
Lift L13
Lift L14
HOOK
2 TONS
HOOK
3 TONS
HOOK
2 TONS
HOOK
2 TONS
HOOK
3 TONS
HOOK
2 TONS
A
B
C
D
E
A
B
C
D
E
L1
L3
L2 L1
L4 L3
L2
L4
Hooks design (BY MBL) to be adjusted as per TQ-952.
Hooks design (BY MBL) to be adjusted as per TQ-952.
Front
Front
1200
1200
HD= 2400
HW1= 1540
HW2= 1435
HW= 2975
HW1= 1340
HW2= 1440
HW= 2780

3 Top Hoist Way Hook Plan - ELEV -L13 & L14

1 : 25

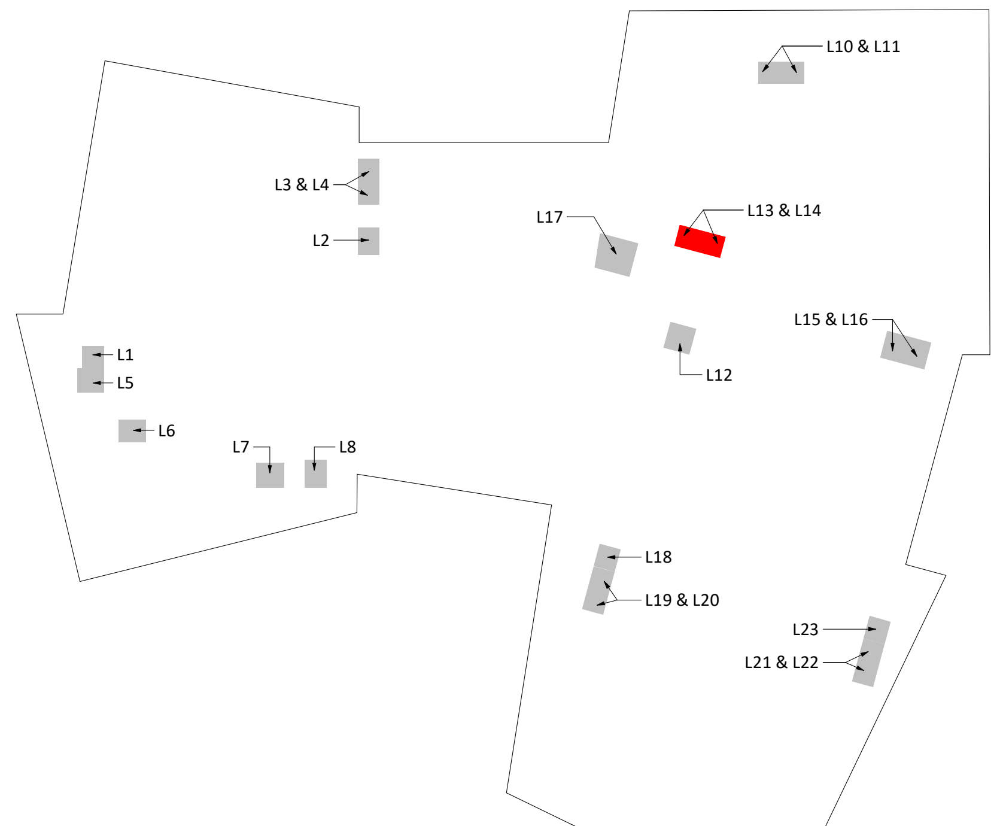
L10 & L11
L3 & L4
L2
L17
L13 & L14
L15 & L16
L12
L1
L5
L6
L7
L8
L18
L19 & L20
L23
L21 & L22

KEY PLAN

CONTROLLED COPY
MBL IFC
JEDDAH OPERA HOUSE PROJECT
QA/QC Department
MBL QAM
Engr. Mudassar Altaf

ELEV-L13 & 14 ELEVATOR GENERAL SPECIFICATIONS	
LIFT NUMBER	ELV.L13 &L14

CABIN INTERNAL SIZE(WXDXH)	1850X1850X2600
CAPACITY	1600Kg
CLEAR ENTRANCE	1200X2400
CONTROL	VVVF
CONTROL SYSTEM	DUPLEX FULL COLLECTIVE
COUNTERWEIGHT SAFETY	NO
DOOR TYPE	CLD1
EMERGENCY EXITS	-
FRONT OPENING	1
HEAT RELEASE	1616Kcal/h
HOISTWAY SIZE(HWXHD)	L13 (2975X2400) & L14 (2780X2400)
LIFT NUMBER	ELV.L13 & 14
LIGHTING SUPPLY	220V 60HZ
MIN.FLOOR HEIGHT	-
NO. OF FLOOR	3
NO. OF OPENINGS	3
NO. OF UNITS	2
NON-STOP FLOORS	-
NON-STOP FLOORS NAMES	-
NUMBER OF PASSENGERS	21P
OVERHEAD	5300mm
PIT DEPTH	1600mm
PRODUCT NO.	GeN2 MRL
RATED CURRENT(A)	25.6
REAR OPENING	2
ROPING	2:1
SPEED(m/s)	1.00
START CURRENT(A)	28.4
SYSTEM POWER(KW)	13.5
TRAVEL	9975mm
USE	PASSENGER LIFT

REACTIONS FORCE (KN)

Car side rail	CWT guide rail	Pit reaction	
R= 41	R= 15	U= 165	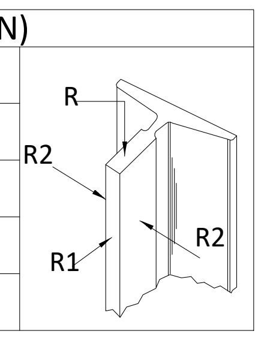
R1= 2.47	R1= 1.13	V= 132	
R2= 3.14	R2= 0.3		

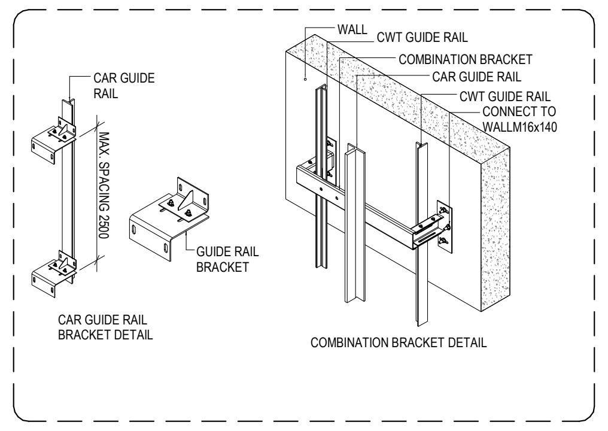
CAR GUIDE RAIL
MAX. SPACING 2500
GUIDE RAIL BRACKET
CAR GUIDE RAIL BRACKET DETAIL
WALL
CWT GUIDE RAIL
COMBINATION BRACKET
CAR GUIDE RAIL
CWT GUIDE RAIL
CONNECT TO WALLM16x140
COMBINATION BRACKET DETAIL

LEGEND

HW	HOIST WAY WIDTH
HD	HOIST WAY DEPTH
CRH	CAR ROUGH HEIGHT
DOOR OP	DOOR OPENING
ROP	ROUGH OPENING
CW	CAR WIDTH
CD	CAR DEPTH
CH	CAR HEIGHT
DBG	DISTANCE BETWEEN GUARDRAIL
CWT	COUNTERWEIGHT
E&I PANEL	EMERGENCY & INSPECTION PANEL
G.O.V	CAR GOVERNOR
COP	CAR OPERATING PANEL
HBP	HALL POSITION INDICATOR

NOTE No.:
FRONT WALLS,FINISHES & ARCHITRAVES TO BE BUILT (BY CLIENT) AFTER THE INSTALLATION OF THE (LANDING) EXTERNAL DOORS.

IMPORTANT NOTE FOR MAIN CONTRACTOR.
FREEDOM OF ACCESS MUST BE AVAILABLE FOR POINT OF ENTRY INTO THE BUILDING UP TO THE ELEVATOR HOIST WAY AND THE FRONT WALLS OF THE HOIST WAY AT MAIN FLOOR TO BE LEFT OPEN FOR FULL WIDTH AND HEIGHT TO PERMIT ENTRY OF OUR EQUIPMENT.

SCEC – K&A Reviewed

Civil	Arch.	Elec.	ELV.	Mech.	Acoustic
☐	☐	☒	☐	☒	☒

KHATIB & ALAMI
SAUDI CONSOLIDATED ENGINEERING COMPANY

SCEC – K&A Reviewed

Code B – Approved with Comments (Do not Resubmit)

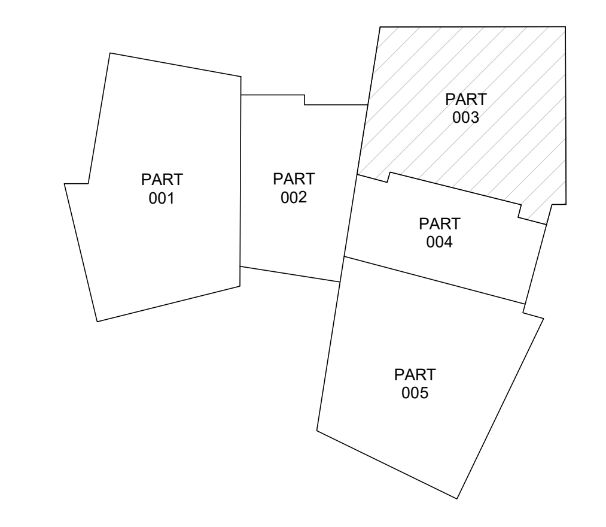
PART 001
PART 002
PART 003
PART 004
PART 005

KEY PLAN

GENERAL NOTES: ALL LEVELS SHOWN ON THE DRAWING ARE CHART DATUM LEVELS PROJECT LEVEL+0.000 = +3.700 CHART DATUM.

dar
Dar Al-Handasah consultants (Shair and Partners)
Checked and Reviewed
Refer to CRS : SD-OPE-MBL-JCDC-01478

For ELE Panels distribution and Connection

Refer to (JOH-ICD-S5-01-056-003-02-SD-EL-011623)

DRAWING / DOCUMENT REFERENCE

NO.	NUMBER	TITLE	REV.
01	L-13 & L-14	JOH-HLA-S4-01-056-XXX-02-DR-AR-011120	F00
02		JOH-BHC-S4-01-056-XXX-XX-DR-VT-015001	
03		JOH-BHC-S4-01-056-XXX-XX-DR-VT-010001	
04		JOH-BHC-S4-01-056-005-ZZ-DR-VT-013001	
05		JOH-BHC-S4-01-056-005-ZZ-DR-VT-011001	
06		TQ-OPE-MBL-JCDC-00952	
07		TQ-OPE-MBL-JCDC-00544	
08		TQ-OPE-MBL-JCDC-00222	
09		TQ-OPE-MBL-JCDC-01052	
10		JCD-OPE-MBL-MR-003-NMR-601-03	
11		JCD-OPE-MBL-MR-003-NMR-602-01	

REVIEWED BY DISCIPLINE	SIGNATURE	DATE
ARCHITECTURAL	[illegible]	[illegible]-04-22
STRUCTURAL	[illegible]	[illegible]
MECHANICAL	ShA	2026-04-22
PLUMBING	ShA	2026-04-22
ELECTRICAL	[illegible]	[illegible]
ICT	[illegible]	[illegible]-04-2[illegible]
ADDITIONAL DISCIPLINES TO BE ADDED AS REQUIRED		

REV	DATE	BY	DESCRIPTION	CHK	APD
S01	16-APR-2026	AK	Shop Drawing	NA	SS
S00	15-APR-2026	AK	Issued for Approval	NA	SS

DRAWING STATUS:
CONSTRUCTION SHOPDRAWING

CLIENT:
شركة وسط جدة للتطوير
Jeddah Central Development Co.

LEAD DESIGN CONSULTANTS:
Henning Larsen

LEAD ENGINEERING CONSULTANT:
BURO HAPPOLD

PROJECT SUPERVISION CONSULTANT:
KHATIB & ALAMI

GENERAL CONTRACTOR:
MBL

REVIEWER:
dar

SUB CONTRACTOR:
OTIS ELEVATOR COMPANY SAUDI ARABIA LIMITED
OTIS

PROJECT
JEDDAH OPERA HOUSE

TITLE:
OPERA BUILDING
VERTICAL TRANSPORTATION
PART 003
PLANS - LIFT SHAFT SHEET 02 OF 02 (L13 & L14)

SCALE @ A1:	CHECKED:		APPROVED:
1:25	Salma Sakr		Ali Basit
PROJECT No:	DESIGNED:	DRAWN:	DATE:
440014	Abdul Kafoor	Pranoti	16-APR-2026

DRAWING No:
JOH-OTS-S5-01-056-003-ZZ-SD-VT-011011

REV:
S01

MODEL FILE REF:
JOH-OTS-S5-01-056-XXX-ZZ-M3-VT-010001

© JCDC

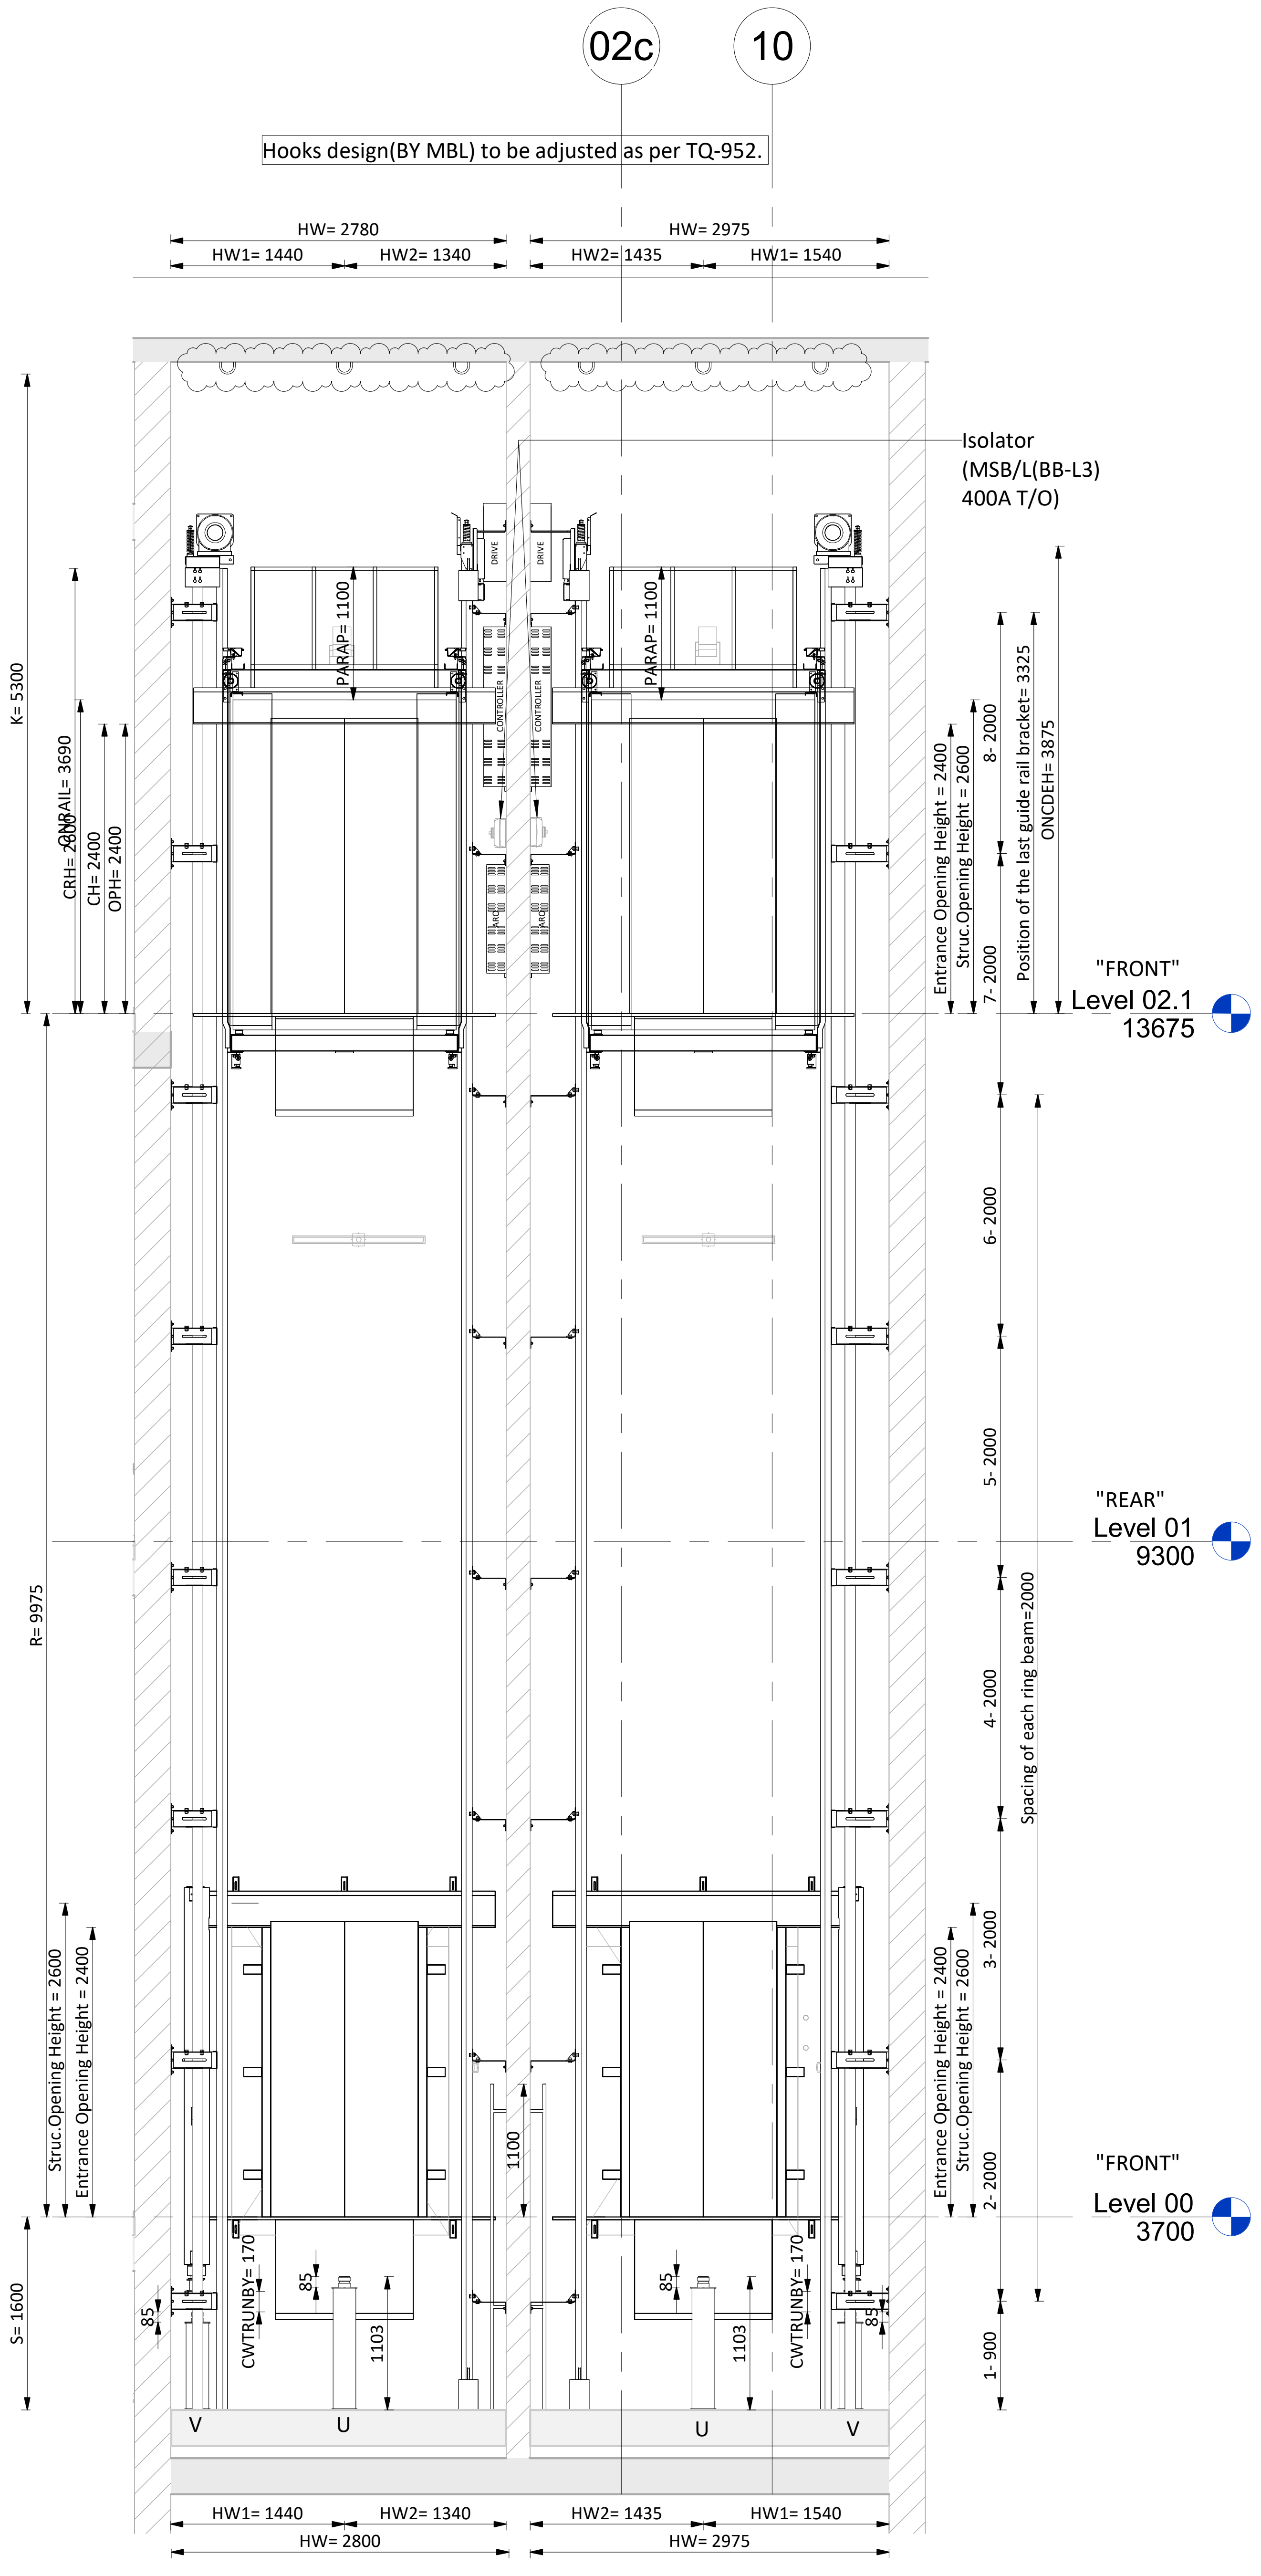
02c
10
Hooks design(BY MBL) to be adjusted as per TQ-952.
HW= 2780
HW1= 1440
HW2= 1340
HW= 2975
HW2= 1435
HW1= 1540
Isolator
(MSB/L(BB-L3)
400A T/O)
PARAP= 1100
K= 5300
CRH= 2600
CRAIL= 3690
CH= 2400
OPH= 2400
Entrance Opening Height = 2400
Struc.Opening Height = 2600
Position of the last guide rail bracket= 3325
ONCDEH= 3875
8- 2000
7- 2000
6- 2000
5- 2000
4- 2000
3- 2000
2- 2000
1- 900
"FRONT"
Level 02.1
13675
"REAR"
Level 01
9300
"FRONT"
Level 00
3700
R= 9975
Spacing of each ring beam=2000
1100
S= 1600
CWTRUNBY= 170
85
1103
V
U
HW1= 1440
HW2= 1340
HW= 2800
HW2= 1435
HW1= 1540
HW= 2975

1 Section "A" - ELEV -L13 & L14
1 : 50

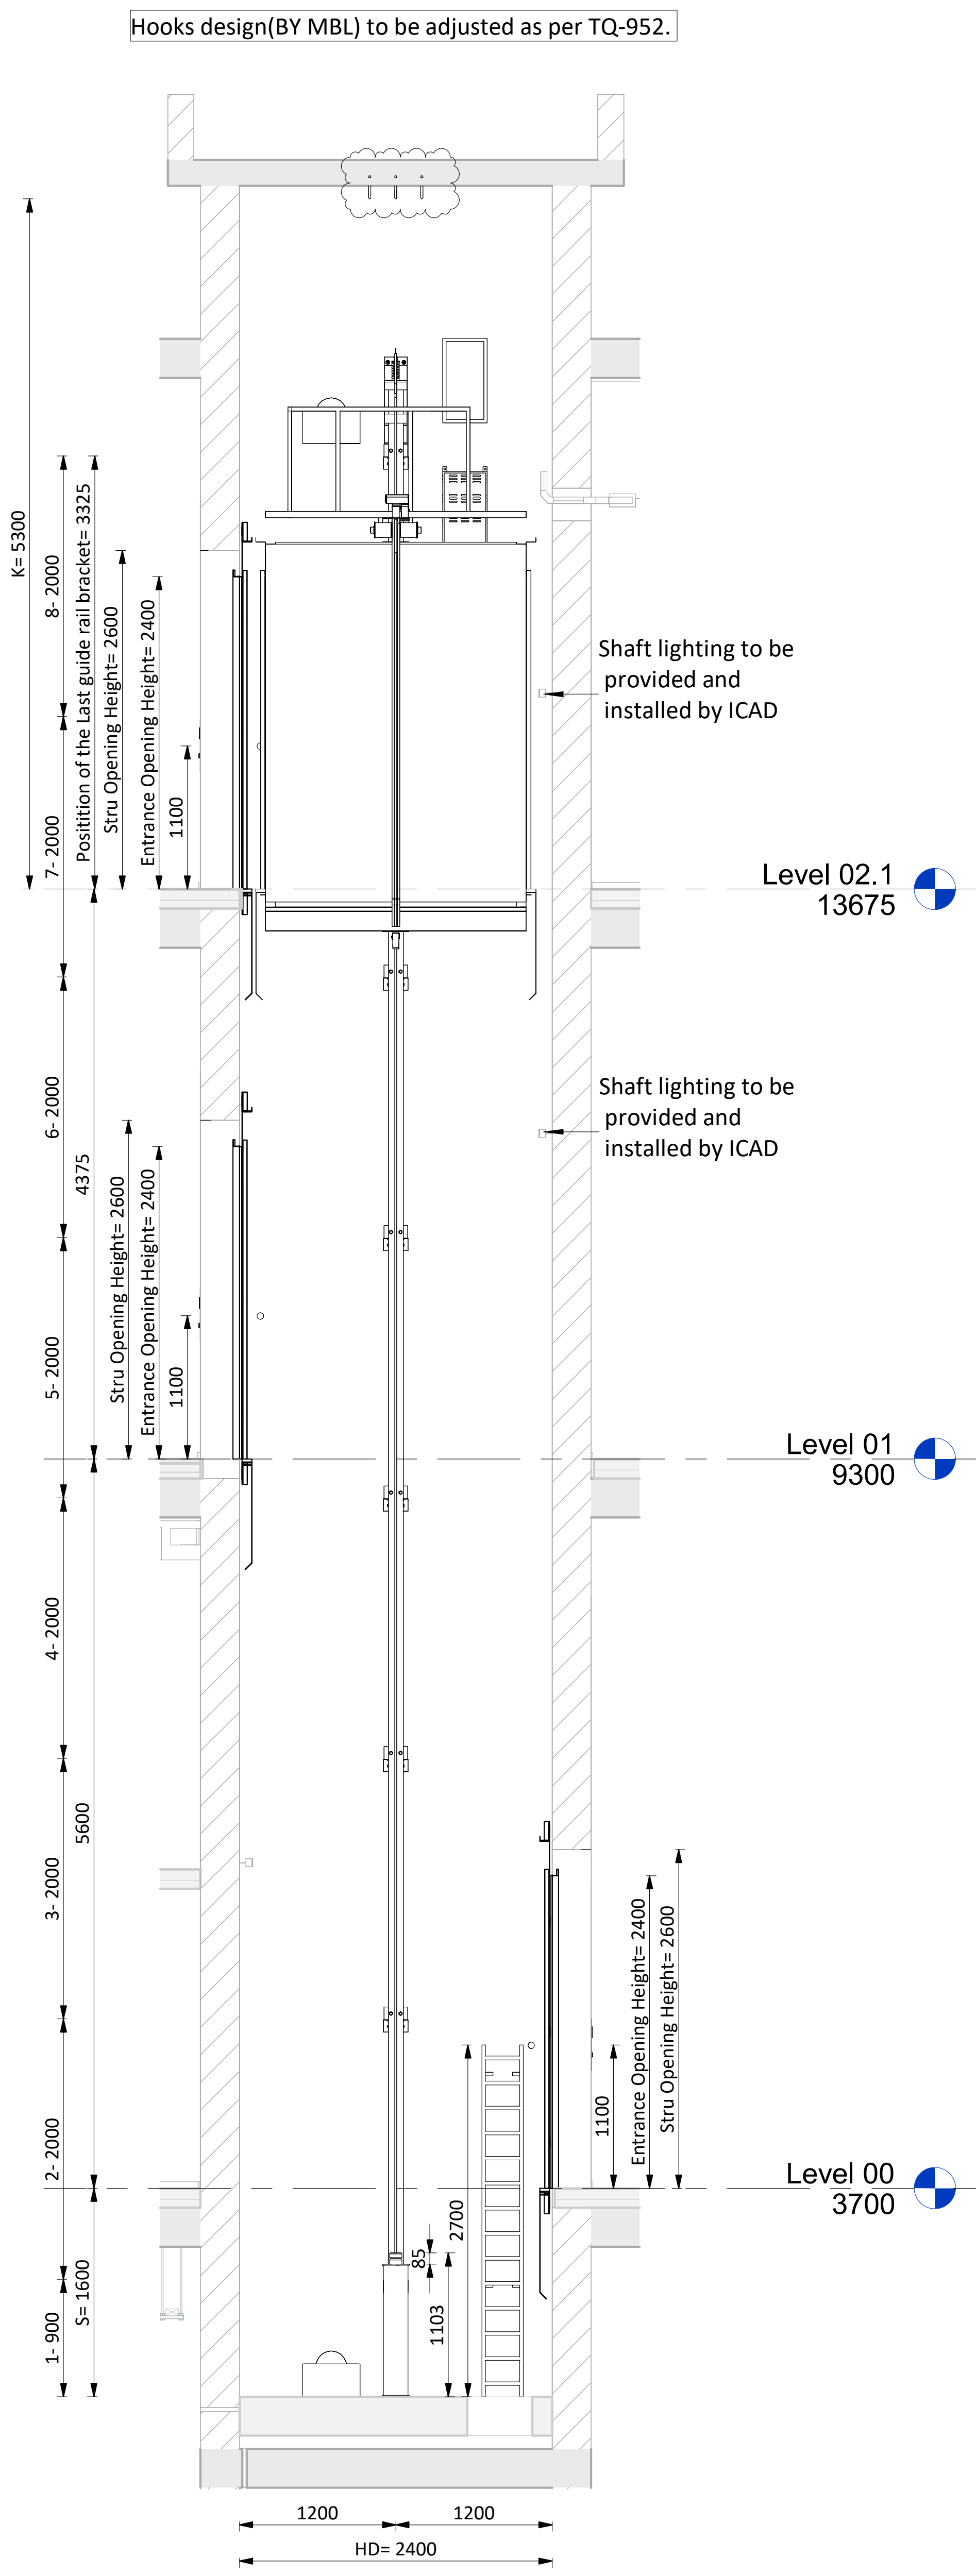
Hooks design(BY MBL) to be adjusted as per TQ-952.
K= 5300
Position of the Last guide rail bracket= 3325
Stru Opening Height= 2600
Entrance Opening Height= 2400
1100
8- 2000
7- 2000
6- 2000
5- 2000
4- 2000
3- 2000
2- 2000
1- 900
4375
5600
S= 1600
Shaft lighting to be provided and installed by ICAD
Level 02.1
13675
Level 01
9300
Level 00
3700
2700
85
1103
1200
1200
HD= 2400

2 Section "B" - ELEV -L13
1 : 50

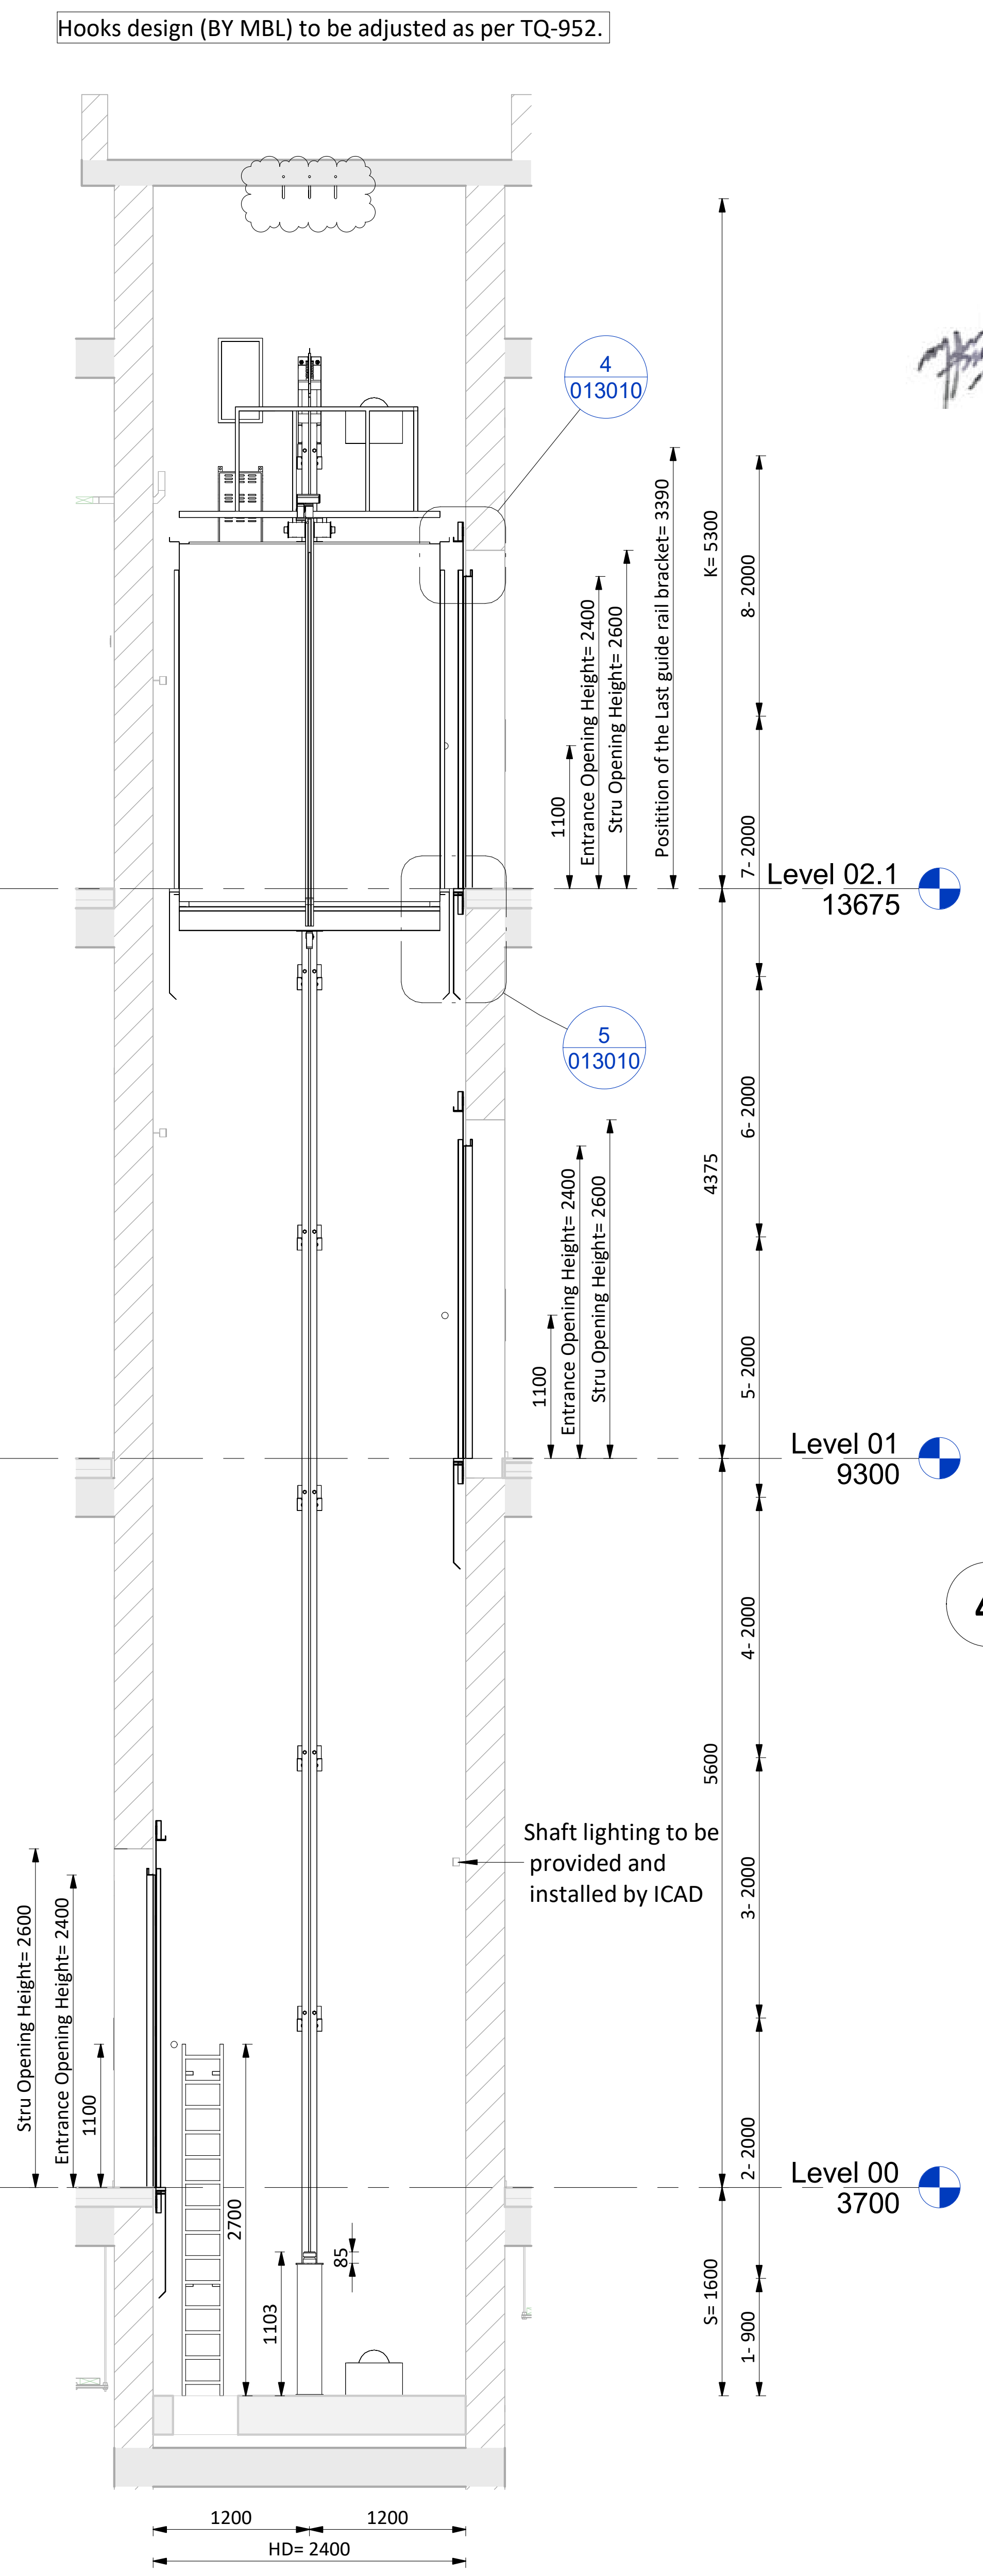
Hooks design (BY MBL) to be adjusted as per TQ-952.
4
013010
5
013010
K= 5300
Position of the Last guide rail bracket= 3390
Entrance Opening Height= 2400
Stru Opening Height= 2600
1100
8- 2000
7- 2000
6- 2000
5- 2000
4- 2000
3- 2000
2- 2000
1- 900
4375
5600
S= 1600
Shaft lighting to be provided and installed by ICAD
Level 02.1
13675
Level 01
9300
Level 00
3700
2700
85
1103
1200
1200
HD= 2400

3 Section "C" - ELEV -L14
1 : 50

CONTROLLED COPY
MBL IFC
JEDDAH OPERA HOUSE PROJECT
QA/QC Department
MBL QAM
Engr. Mudassar Altaf

SCEC – K&A Reviewed

Code B – Approved with Comments (Do not Resubmit)

KHATIB & ALAMI

SAUDI CONSOLIDATED ENGINEERING COMPANY

SCEC – K&A Reviewed

Civil	Arch.	Elec.	ELV.	Mech.	Acoustic
☐	☐	☒	☐	☒	☒

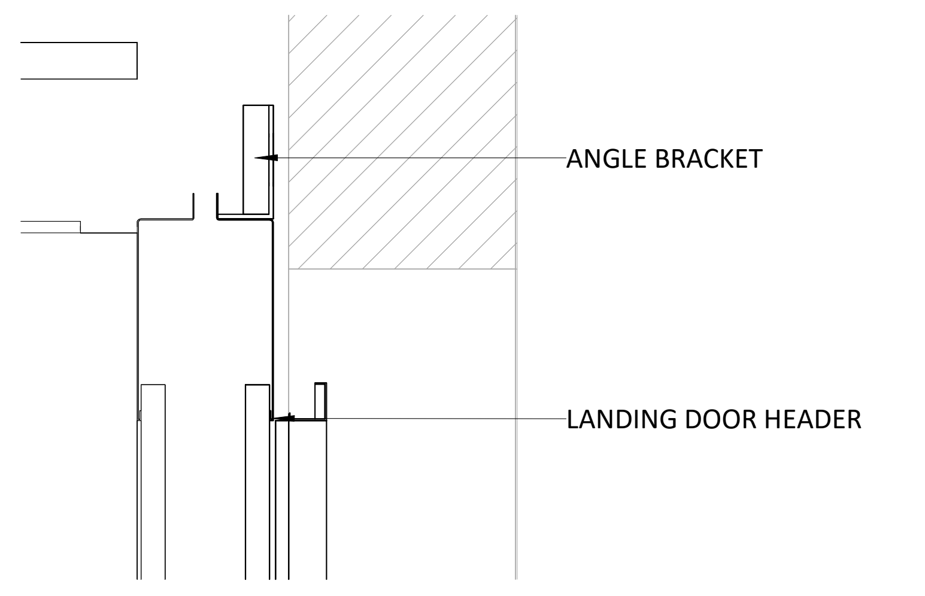
ANGLE BRACKET
LANDING DOOR HEADER

4 Landing Door Header Detail - ELEV -L13 & L14
1 : 10

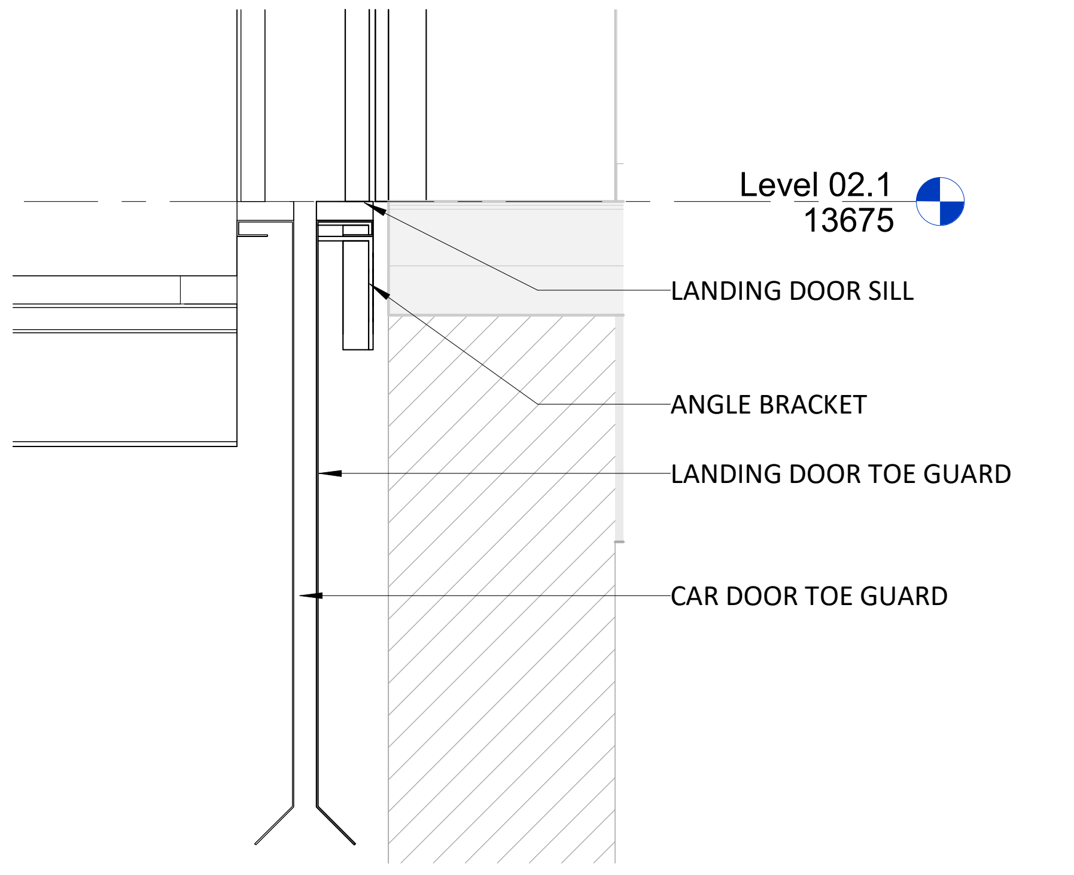
Level 02.1
13675
LANDING DOOR SILL
ANGLE BRACKET
LANDING DOOR TOE GUARD
CAR DOOR TOE GUARD

5 Landing Door Bottom Detail - ELEV -L13 & L14
1 : 10

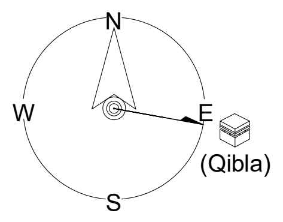

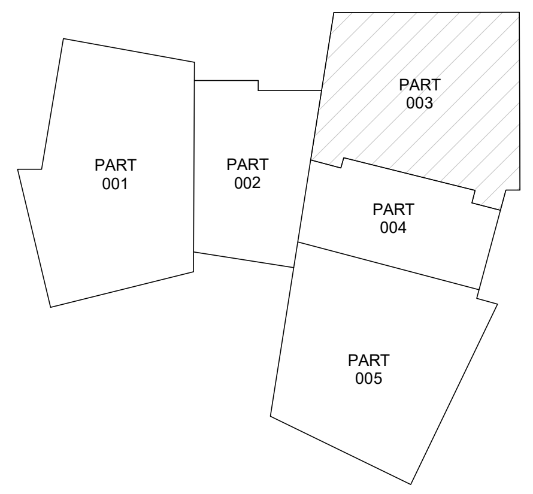
PART 001
PART 002
PART 003
PART 004
PART 005

KEY PLAN

GENERAL NOTES: ALL LEVELS SHOWN ON THE DRAWING ARE CHART DATUM LEVELS PROJECT LEVEL+0.000 = +3.700 CHART DATUM.

dar (Dar Al-Handasah consultants (Shair and Partners))
Checked and Reviewed
Refer to CRS : SD-OPE-MBL-JCDC-01478

For ELE Panels distribution and Connection
Refer to (JOH-ICD-S5-01-056-003-02-SD-EL-011623)

DRAWING / DOCUMENT REFERENCE

NO.	NUMBER	TITLE	REV.
01	L-13 & L-14	JOH-HLA-S4-01-056-XXX-02-DR-AR-011120	F00
02		JOH-BHC-S4-01-056-XXX-XX-DR-VT-015001	
03		JOH-BHC-S4-01-056-XXX-XX-DR-VT-010001	
04		JOH-BHC-S4-01-056-005-ZZ-DR-VT-013001	
05		JOH-BHC-S4-01-056-005-ZZ-DR-VT-011001	
06		TQ-OPE-MBL-JCDC-00952	
07		TQ-OPE-MBL-JCDC-00544	
08		TQ-OPE-MBL-JCDC-00222	
09		TQ-OPE-MBL-JCDC-01052	
10		JCD-OPE-MBL-MR-003-NMR-601-03	
11		JCD-OPE-MBL-MR-003-NMR-602-01	

REVIEWED BY DISCIPLINE	SIGNATURE	DATE
ARCHITECTURAL	[illegible]	[illegible]
STRUCTURAL	[illegible]	[illegible]
MECHANICAL	ShA	2026-04-22
PLUMBING	ShA	2026-04-22
ELECTRICAL	[illegible]	[illegible]
ICT	[illegible]	[illegible]
ADDITIONAL DISCIPLINES TO BE ADDED AS REQUIRED		

REV	DATE	BY	DESCRIPTION	CHK	APD
S01	16-APR-2026	AK	Shop Drawing	NA	SS
S00	15-APR-2026	AK	Issued for Approval	NA	SS

DRAWING STATUS:
CONSTRUCTION SHOPDRAWING

CLIENT:
شركة وسط جدة للتطوير
Jeddah Central Development Co.

LEAD DESIGN CONSULTANTS:
Henning Larsen

LEAD ENGINEERING CONSULTANT:
BURO HAPPOLD

PROJECT SUPERVISION CONSULTANT:
KHATIB & ALAMI

GENERAL CONTRACTOR:
MBL

REVIEWER:
dar

SUB CONTRACTOR:
OTIS ELEVATOR COMPANY SAUDI ARABIA LIMITED
OTIS

PROJECT
JEDDAH OPERA HOUSE

TITLE:
OPERA BUILDING
VERTICAL TRANSPORTATION
PART 003
SECTIONS - LIFT SHAFT (L13 & L14)

SCALE @ A1:	CHECKED:		APPROVED:
As indicated	Salma Sakr		Ali Basit
PROJECT No:	DESIGNED:	DRAWN:	DATE:
440014	Abdul Kafoor	Pranoti	16-APR-2026

DRAWING No:
JOH-OTS-S5-01-056-003-ZZ-SD-VT-013010

REV:
S01

MODEL FILE REF:
JOH-OTS-S5-01-056-XXX-ZZ-M3-VT-010001

© JCDC