Lift 19,20

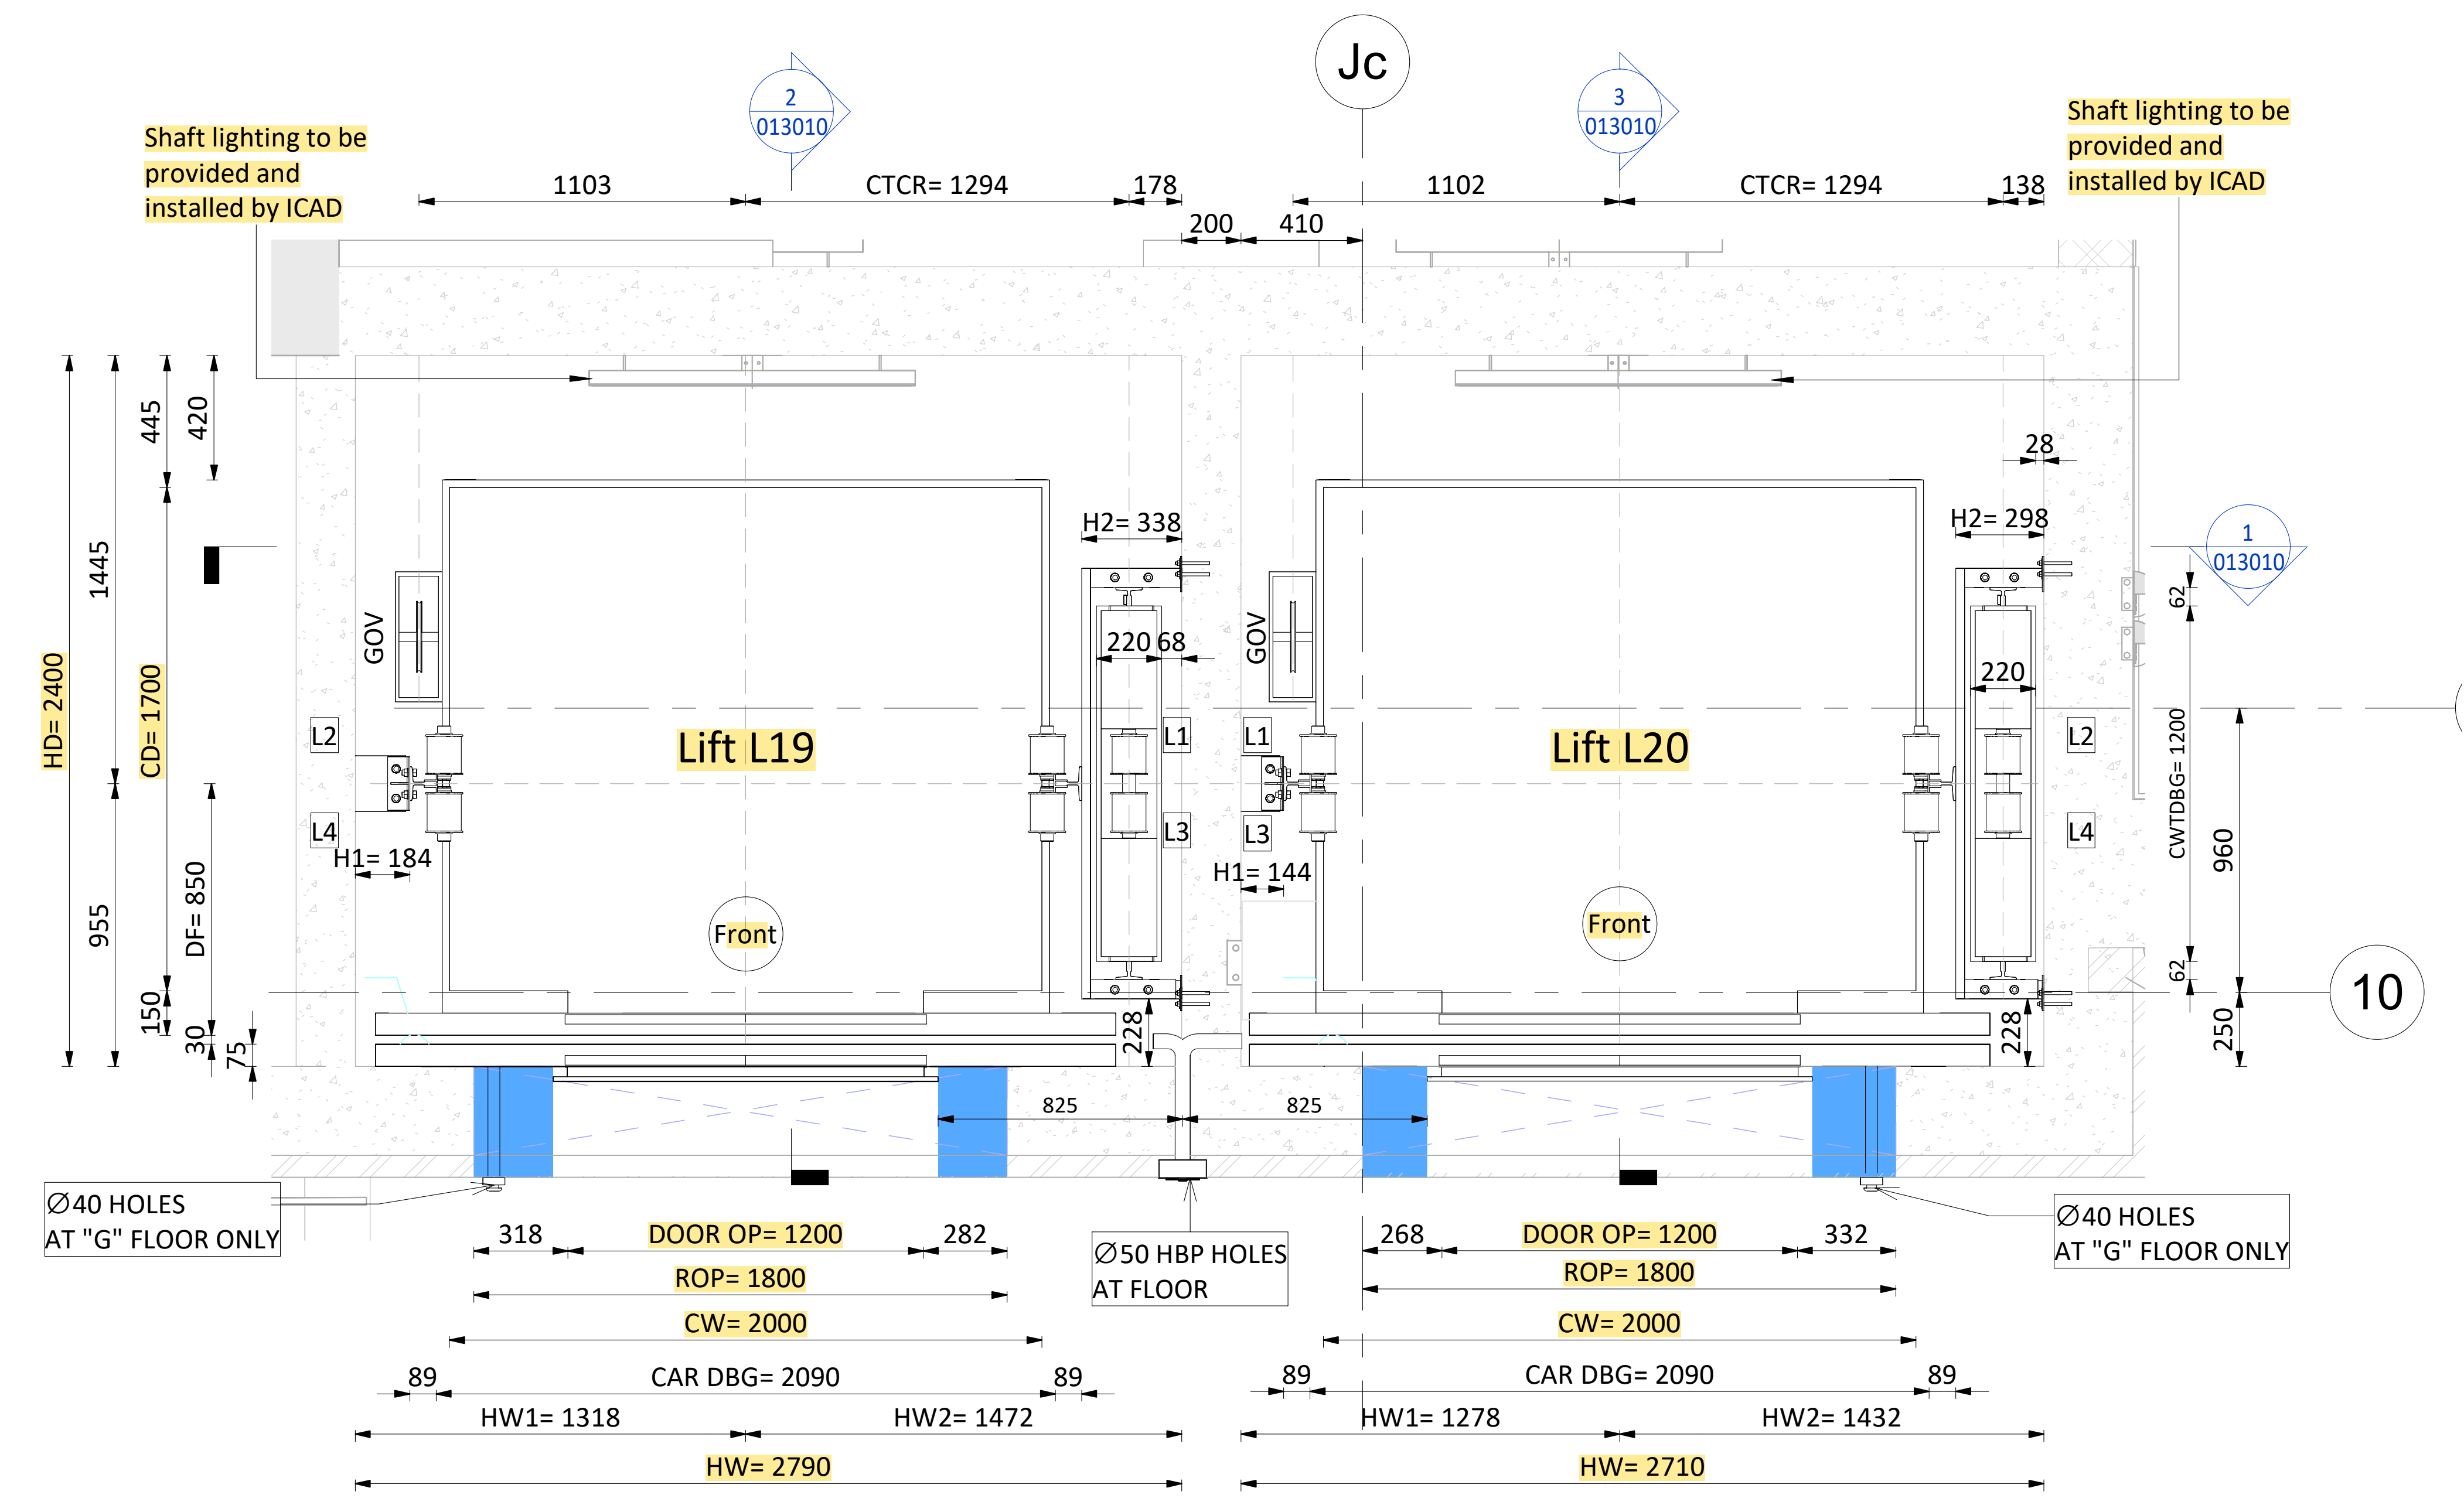

1 Hoist Way Plan At "G" Floor - ELEV-L19 & L20

1 : 25

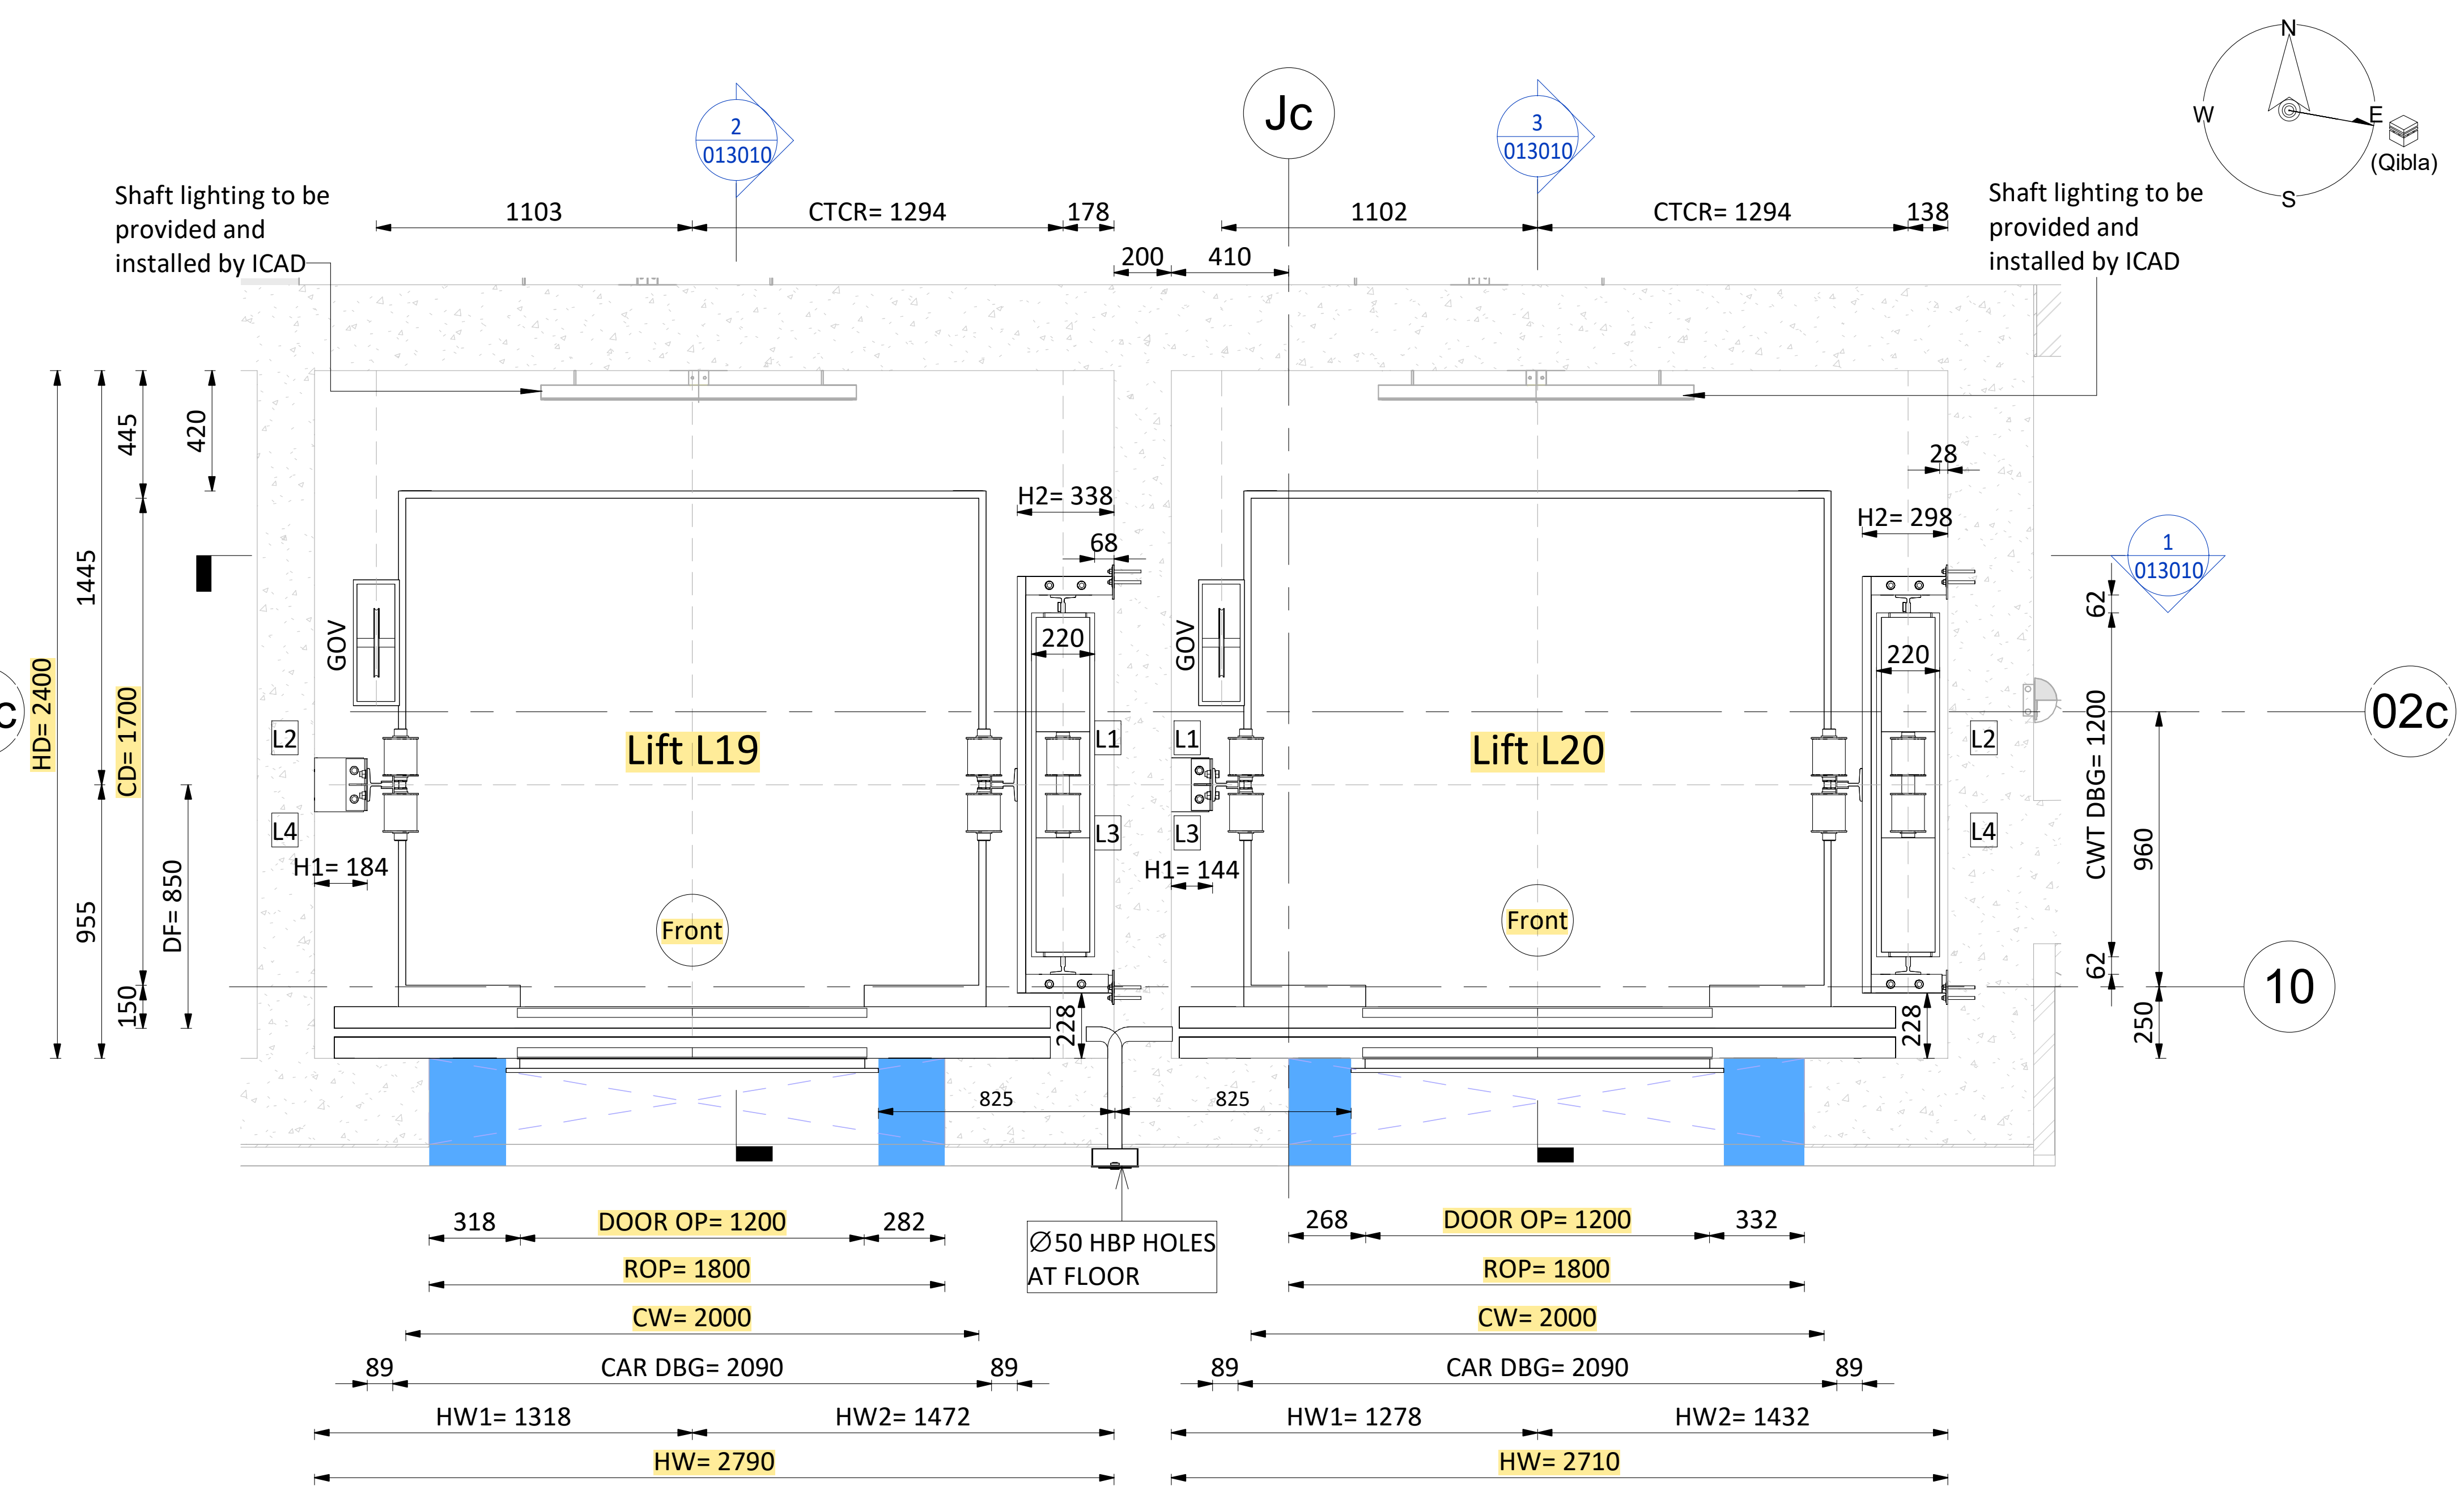

2 Hoist Way Plan At "Typical" Floor - ELEV-L19 & L20

1 : 25

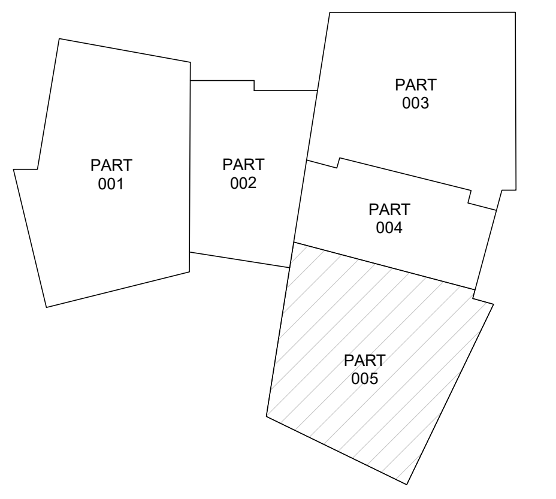

KEY PLAN

GENERAL NOTES: ALL LEVELS SHOWN ON THE DRAWING ARE CHART DATUM LEVELS PROJECT LEVEL+0.000 = +3.700 CHART DATUM.

Refer to :
LIFTS overhead steel hook beams structural calculation and fixation details: TR-OPE-MBL-JCDC-05193-S01
CRS: SD-OPE-MBL-JCDC-01382 - CRS - version-(0_00)-L19,20
Electrical Panels distribution:
JOH-ICD-S5-01-056-005-02-SD-EL-011625
JOH-ICD-S5-01-056-XXX-03-SD-EL-011630_1
wiring diagram opera lift
Acoustic Letter: L-OTIS-MBL-OPE-26-0015

DRAWING / DOCUMENT REFERENCE

NO.	NUMBER	TITLE	REV.
01	L-19 & L-20	JOH-HLA-S4-01-056-005-00-DR-AR-011105	F00
02		JOH-BHC-S4-01-056-XXX-XX-DR-VT-015001	
03		JOH-BHC-S4-01-056-XXX-XX-DR-VT-010001	
04		JOH-BHC-S4-01-056-005-ZZ-DR-VT-013001	
05		JOH-BHC-S4-01-056-005-ZZ-DR-VT-011001	
06		TQ-OPE-MBL-JCDC-00222	
07		TQ-OPE-MBL-JCDC-01258	
08		JCD-OPE-MBL-MR-003-NMR-601-03	
09		JCD-OPE-MBL-MR-003-NMR-602-01	
10		TR-OPE-MBL-JCDC-05193-01	

REVIEWED BY DISCIPLINE	SIGNATURE	DATE
ARCHITECTURAL	MT	[illegible]
STRUCTURAL	PC	[illegible]
MECHANICAL	ShA	2026-05-20
PLUMBING	[illegible]	[illegible]
ELECTRICAL	ShA	2026-05-20
ICT	ShA	[illegible]
ADDITIONAL DISCIPLINES TO BE ADDED AS REQUIRED		

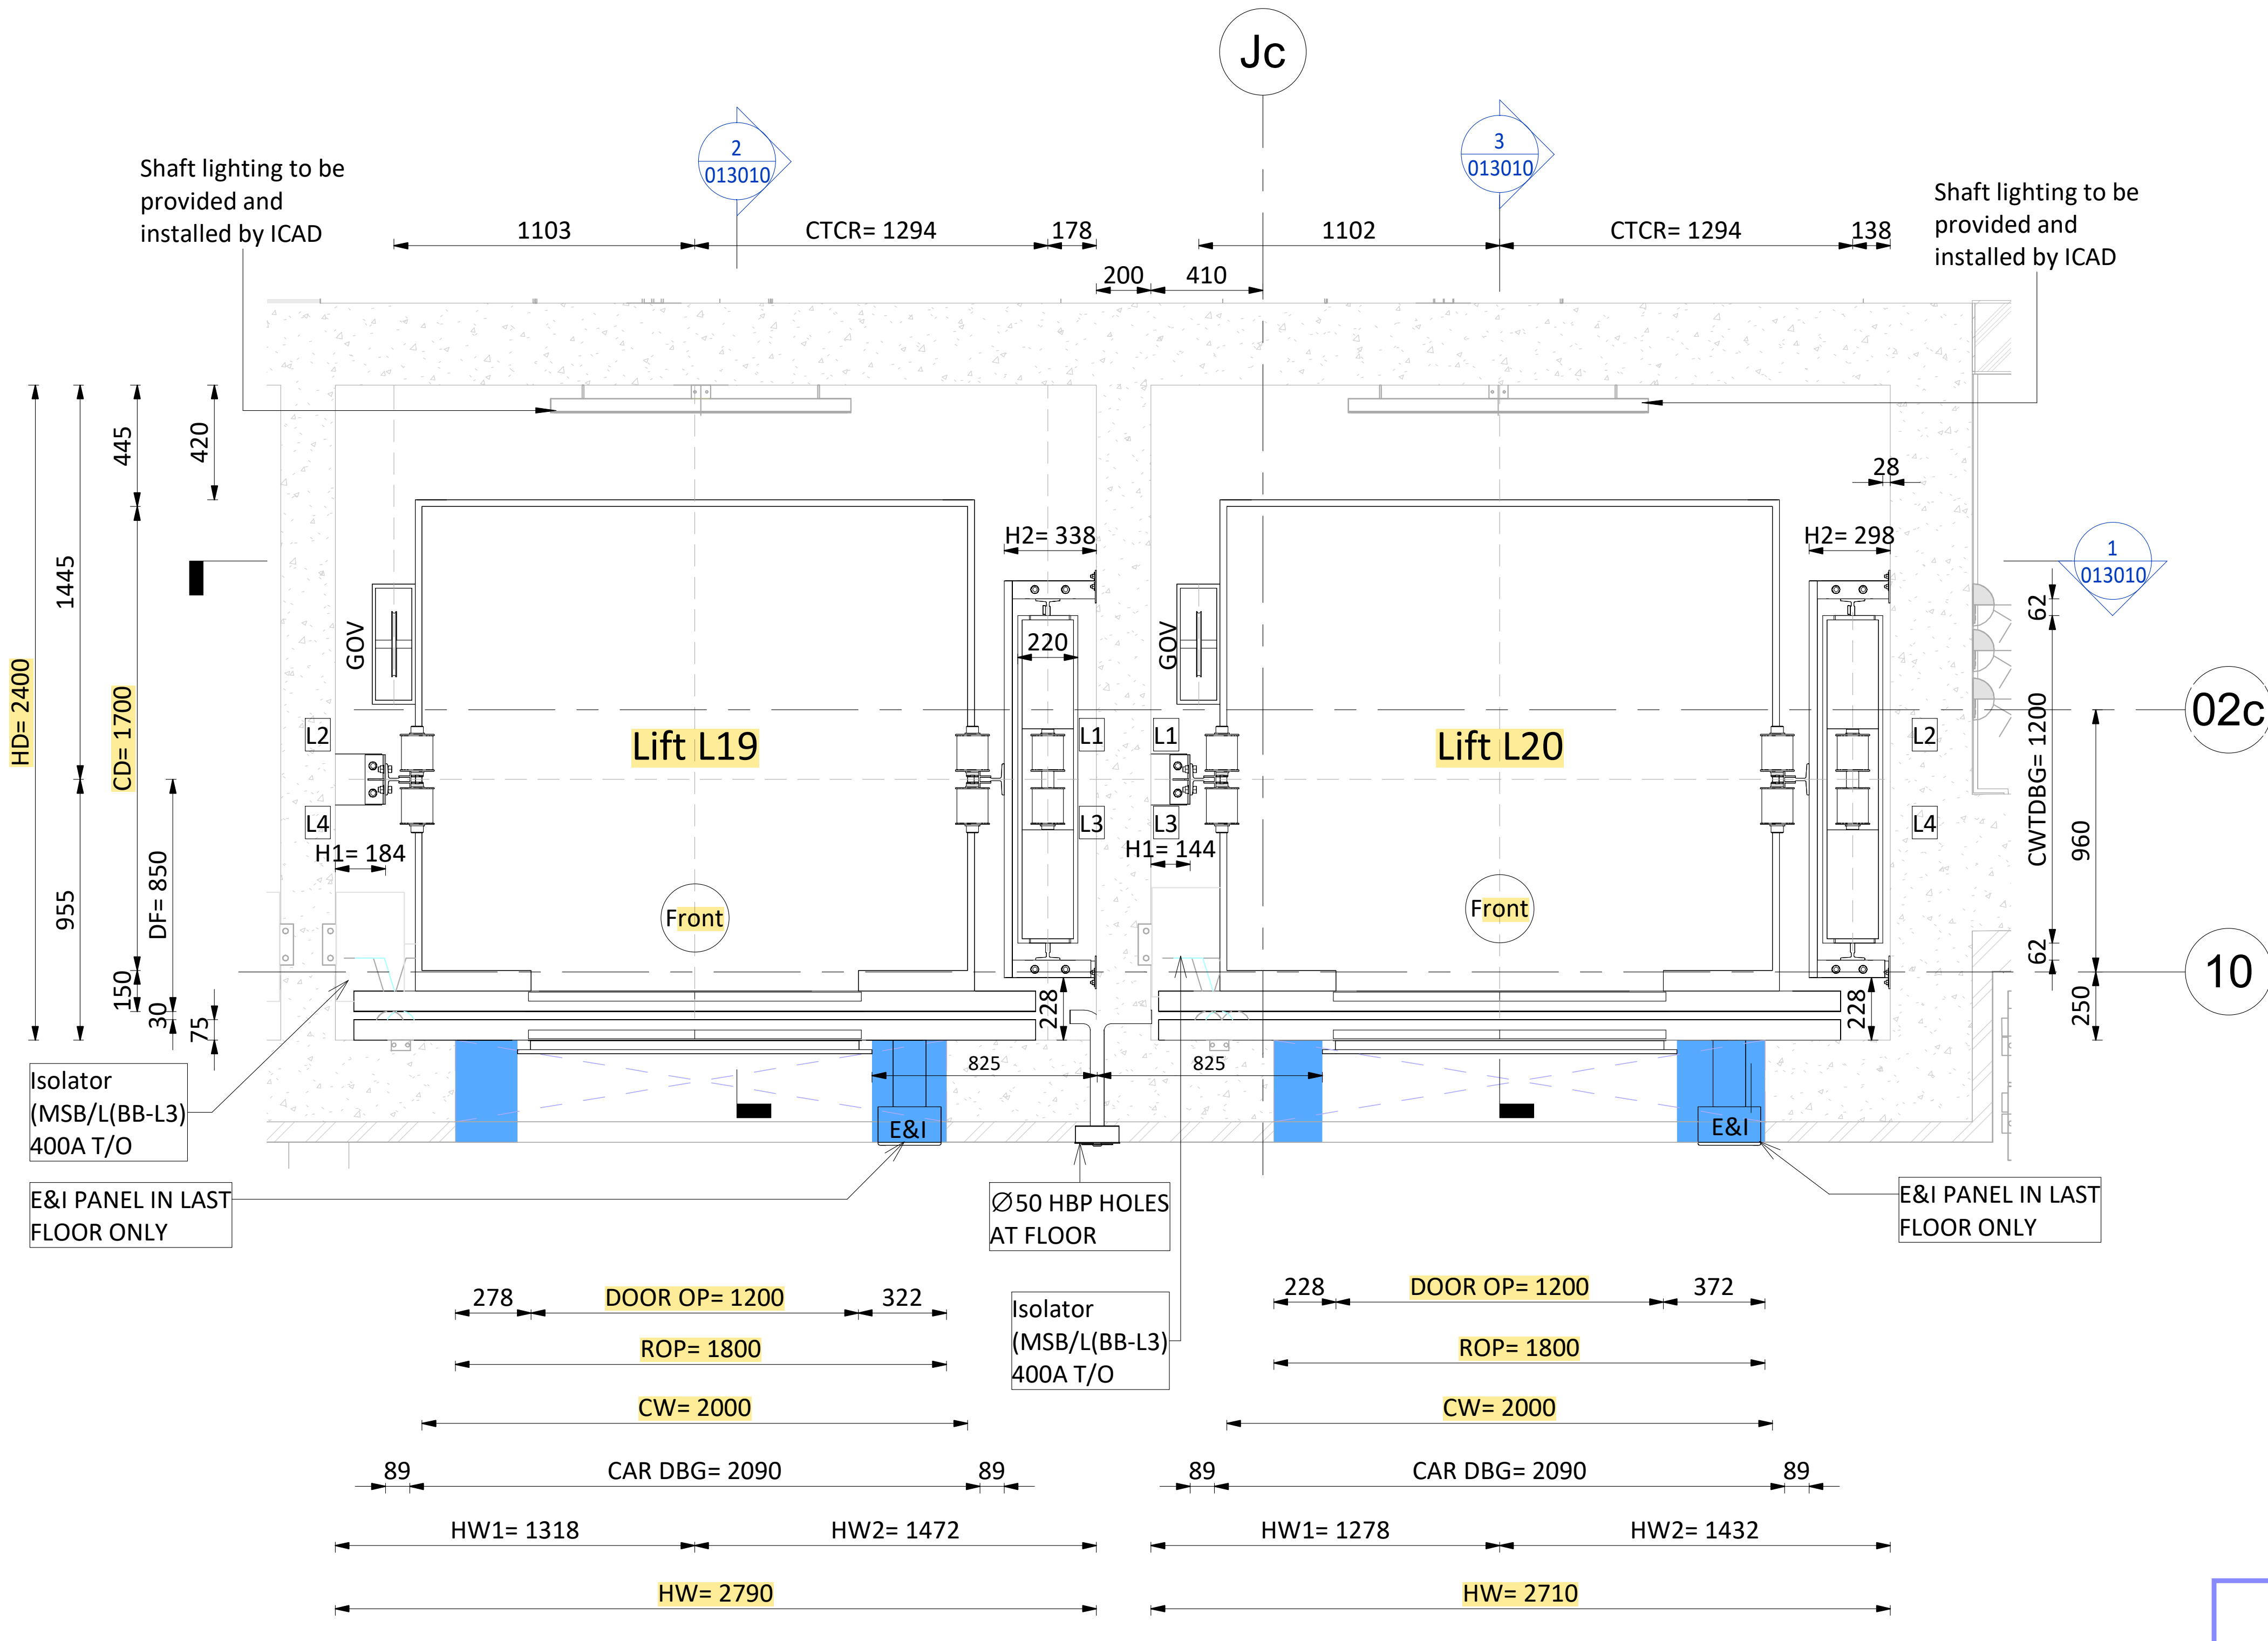

3 Hoist Way Plan At "3" Floor - ELEV-L19 & L20

1 : 25

CONTROLLED COPY
MBL IFC
JEDDAH OPERA HOUSE PROJECT
QA/QC Department
MBL QAM
Engr. Mudassar Altaf

SCEC – K&A Reviewed
KHATIB & ALAMI
SAUDI CONSOLIDATED ENGINEERING COMPANY

Civil	Arch.	Elec.	ELV.	Mech.	Acoustic
☒	☒	☒	☐	☒	☒

KHATIB & ALAMI
SAUDI CONSOLIDATED ENGINEERING COMPANY
SCEC – K&A Reviewed
Code B – Approved with Comments (Do not Resubmit)

dar
Dar Al-Handasah consultants (Shair and Partners)
Checked and Reviewed

MBL to provide a comprehensive Method Statement describing the procedure for filling all gaps and correcting / adjusting the rough openings for doors

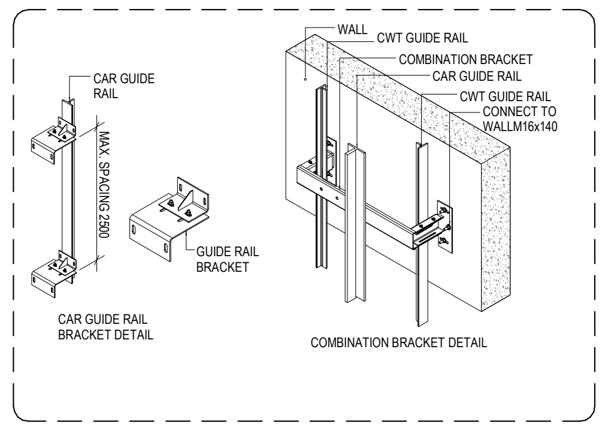
CAR GUIDE RAIL
GUIDE RAIL BRACKET
CAR GUIDE RAIL BRACKET DETAIL
WALL
CWT GUIDE RAIL
COMBINATION BRACKET
CAR GUIDE RAIL
CWT GUIDE RAIL CONNECT TO WALL
COMBINATION BRACKET DETAIL

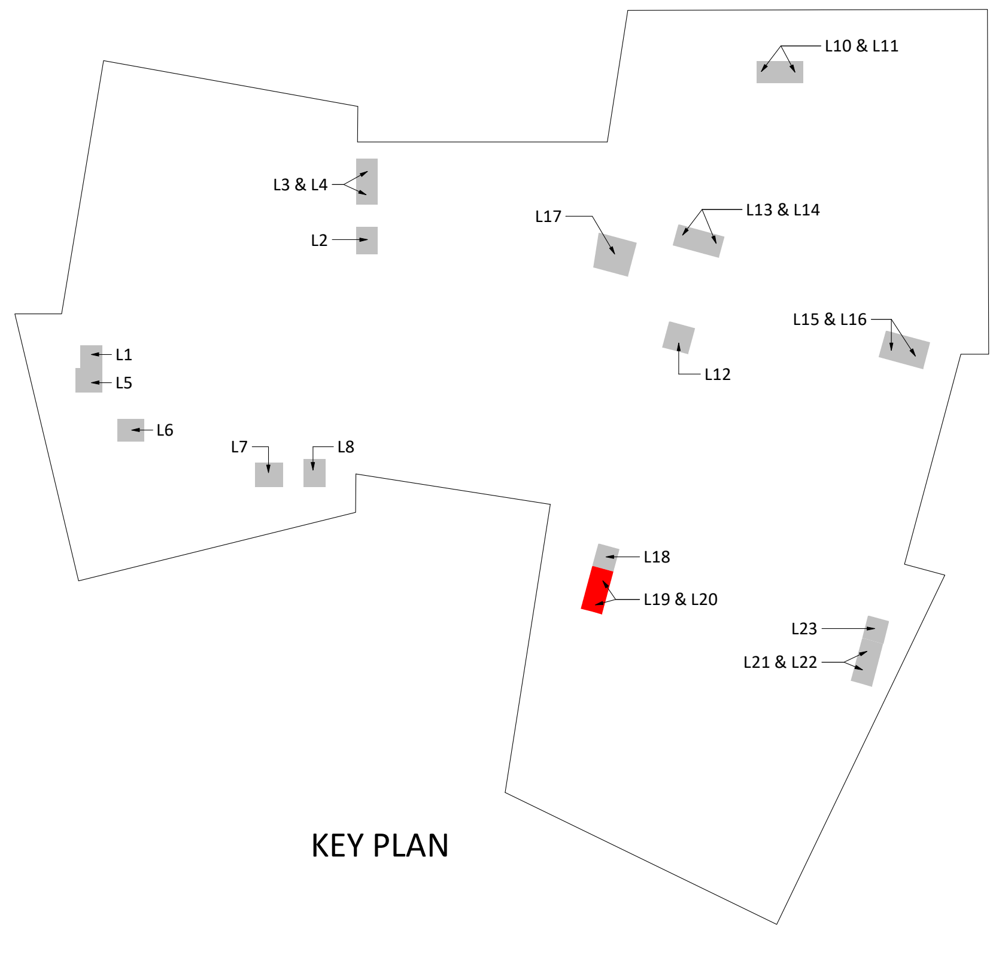

KEY PLAN

ELEV-L19 & 20 ELEVATOR GENERAL SPECIFICATIONS	
LIFT NUMBER	ELEV.L19 & 20

CABIN INTERNAL SIZE(WXDXH)	2000X1700X2600
CAPACITY	1600 Kg
CLEAR ENTRANCE	1200X2400
CONTROL	VVVF
CONTROL SYSTEM	DUPLEX FULL COLLECTIVE
COUNTERWEIGHT SAFETY	YES
DOOR TYPE	CLD1
EMERGENCY EXITS	-
FRONT OPENING	4
HEAT RELEASE	1616Kcal/h
HOISTWAY SIZE(HWXHD)	2790X2400&2710X2400
LIFT NUMBER	ELV.L19 & 20
LIGHTING SUPPLY	220V 60HZ
MIN.FLOOR HEIGHT	3000
NO. OF FLOOR	4
NO. OF OPENINGS	4
NO. OF UNITS	2
NON-STOP FLOORS	-
NON-STOP FLOORS NAMES	-
NUMBER OF PASSENGERS	21P
OVERHEAD	5400mm
PIT DEPTH	1600mm
POWER SUPPLY	380V 3P 60HZ
PRODUCT NO.	GeN2 MRL
RATED CURRENT(A)	25.6
REAR OPENING	-
ROPING	2:1
SPEED(m/s)	1.00
START CURRENT(A)	28.4
SYSTEM POWER(KW)	13.5
TRAVEL	13825mm
USE	PASSENGER LIFT

Public

REACTIONS FORCE (KN)			
Car side rail	CWT guide rail	Pit reaction	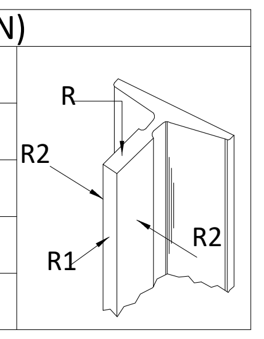 R R1 R2
R= 41	R= 48	U= 165	
R1= 2.47	R1= 1.13	V= 132	
R2= 3.14	R2= 0.3		

LEGEND	
HW	HOIST WAY WIDTH
HD	HOIST WAY DEPTH
CRH	CAR ROUGH HEIGHT
DOOR OP	DOOR OPENING
ROP	ROUGH OPENING
CW	CAR WIDTH
CD	CAR DEPTH
CH	CAR HEIGHT
DBG	DISTANCE BETWEEN GUARDRAIL
CWT	COUNTERWEIGHT
E&I PANEL	EMERGENCY & INSPECTION PANEL
G.O.V	CAR GOVERNOR
COP	CAR OPERATING PANEL
HBP	HALL POSITION INDICATOR

NOTE No.:
FRONT WALLS,FINISHES & ARCHITRAVES TO BE BUILT (BY CLIENT) AFTER THE INSTALLATION OF THE (LANDING) EXTERNAL DOORS.

IMPORTANT NOTE FOR MAIN CONTRACTOR.
FREEDOM OF ACCESS MUST BE AVAILABLE FOR POINT OF ENTRY INTO THE BUILDING UP TO THE ELEVATOR HOIST WAY AND THE FRONT WALLS OF THE HOIST WAY AT MAIN FLOOR TO BE LEFT OPEN FOR FULL WIDTH AND HEIGHT TO PERMIT ENTRY OF OUR EQUIPMENT.

REV	DATE	BY	DESCRIPTION	CHK	APD
S01	07-MAY-2026	AK	Shop Drawing	SS	AB
S00	06-MAY-2026	AK	Issued for Approval	SS	AB

DRAWING STATUS:
CONSTRUCTION SHOPDRAWING

CLIENT:
شركة وسط جدة للتطوير
Jeddah Central Development Co.

LEAD DESIGN CONSULTANTS:
Henning Larsen

LEAD ENGINEERING CONSULTANT:
BURO HAPPOLD

PROJECT SUPERVISION CONSULTANT:
KHATIB & ALAMI

GENERAL CONTRACTOR:
MBL

REVIEWER:
dar

SUB CONTRACTOR:
OTIS ELEVATOR COMPANY SAUDI ARABIA LIMITED
OTIS

PROJECT
JEDDAH OPERA HOUSE

TITLE:
OPERA BUILDING
VERTICAL TRANSPORTATION
PART 005
PLANS - LIFT SHAFT SHEET 01 OF 02 (L19 & L20)

SCALE @ A1:	CHECKED:		APPROVED:
1:25	SS		AB
PROJECT No:	DESIGNED:	DRAWN:	DATE:
440014	AK	PR	07-MAY-2026

DRAWING No:
JOH-OTS-S5-01-056-005-ZZ-SD-VT-011010

REV:
S01

MODEL FILE REF:
JOH-OTS-S5-01-056-XXX-ZZ-M3-VT-010001

© JCDC

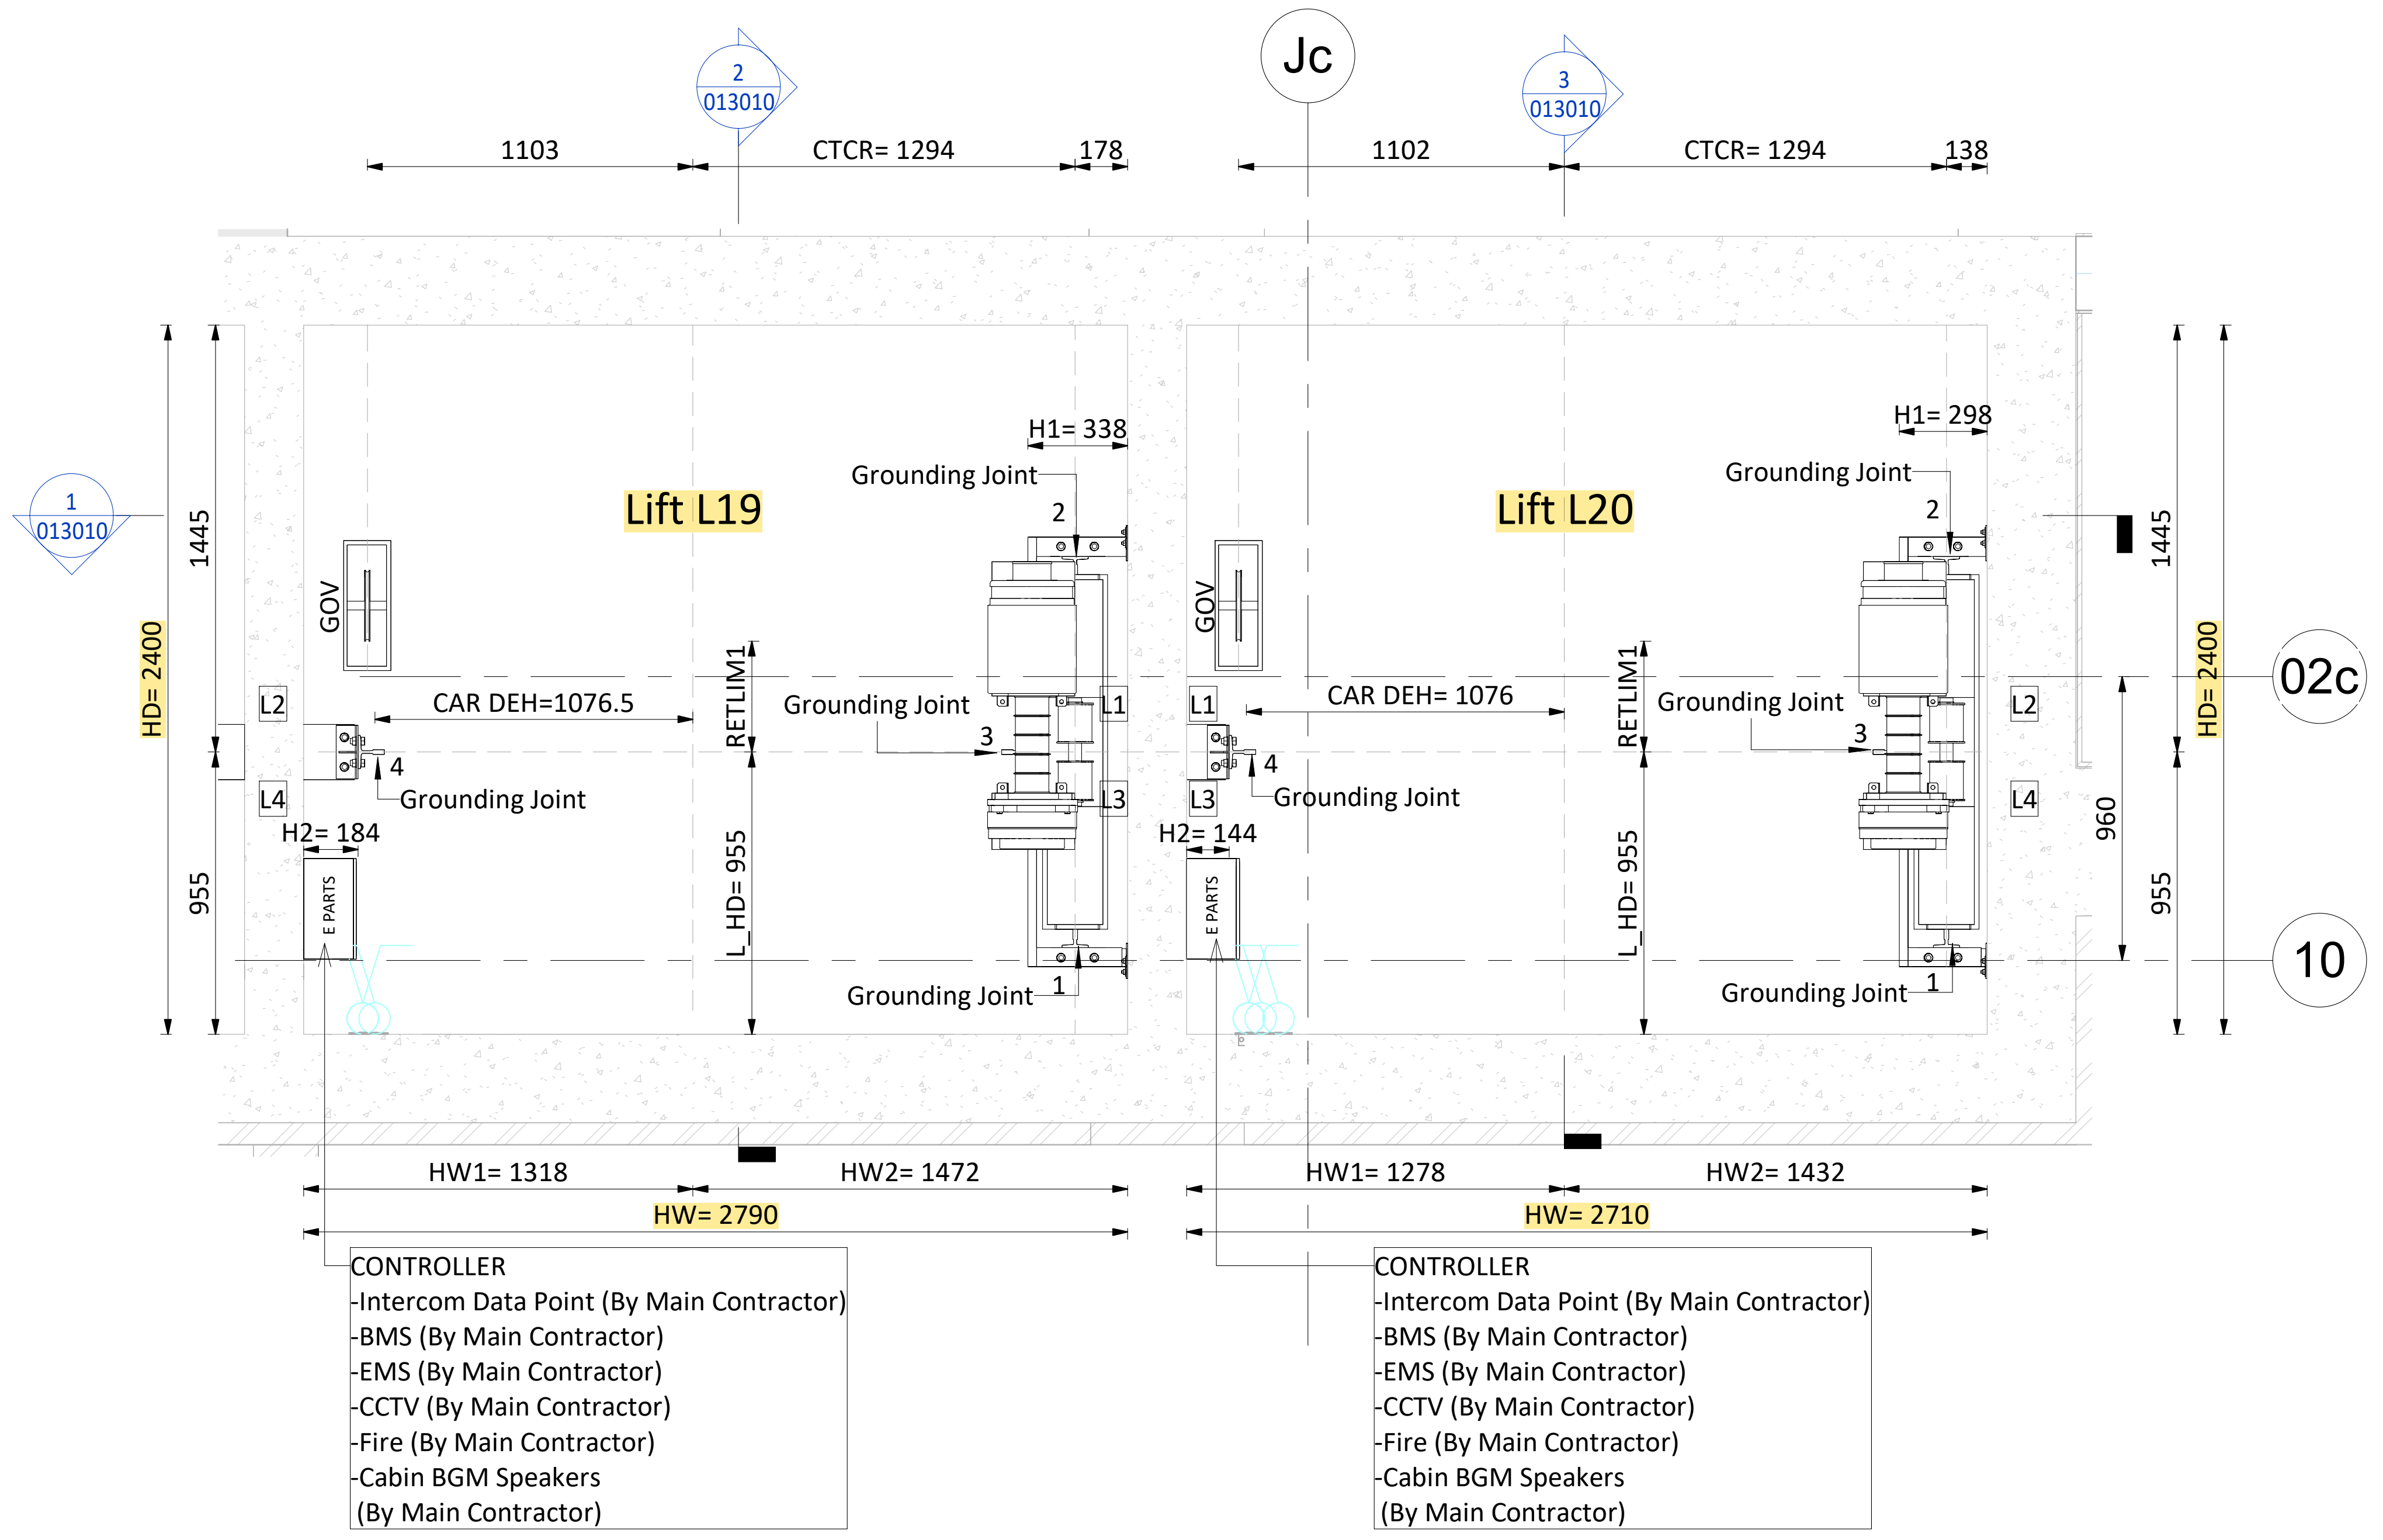

CONTROLLER
-Intercom Data Point (By Main Contractor)
-BMS (By Main Contractor)
-EMS (By Main Contractor)
-CCTV (By Main Contractor)
-Fire (By Main Contractor)
-Cabin BGM Speakers
(By Main Contractor)

CONTROLLER
-Intercom Data Point (By Main Contractor)
-BMS (By Main Contractor)
-EMS (By Main Contractor)
-CCTV (By Main Contractor)
-Fire (By Main Contractor)
-Cabin BGM Speakers
(By Main Contractor)

1 Machine Plan Level - ELEV-L19 & L20

1 : 25

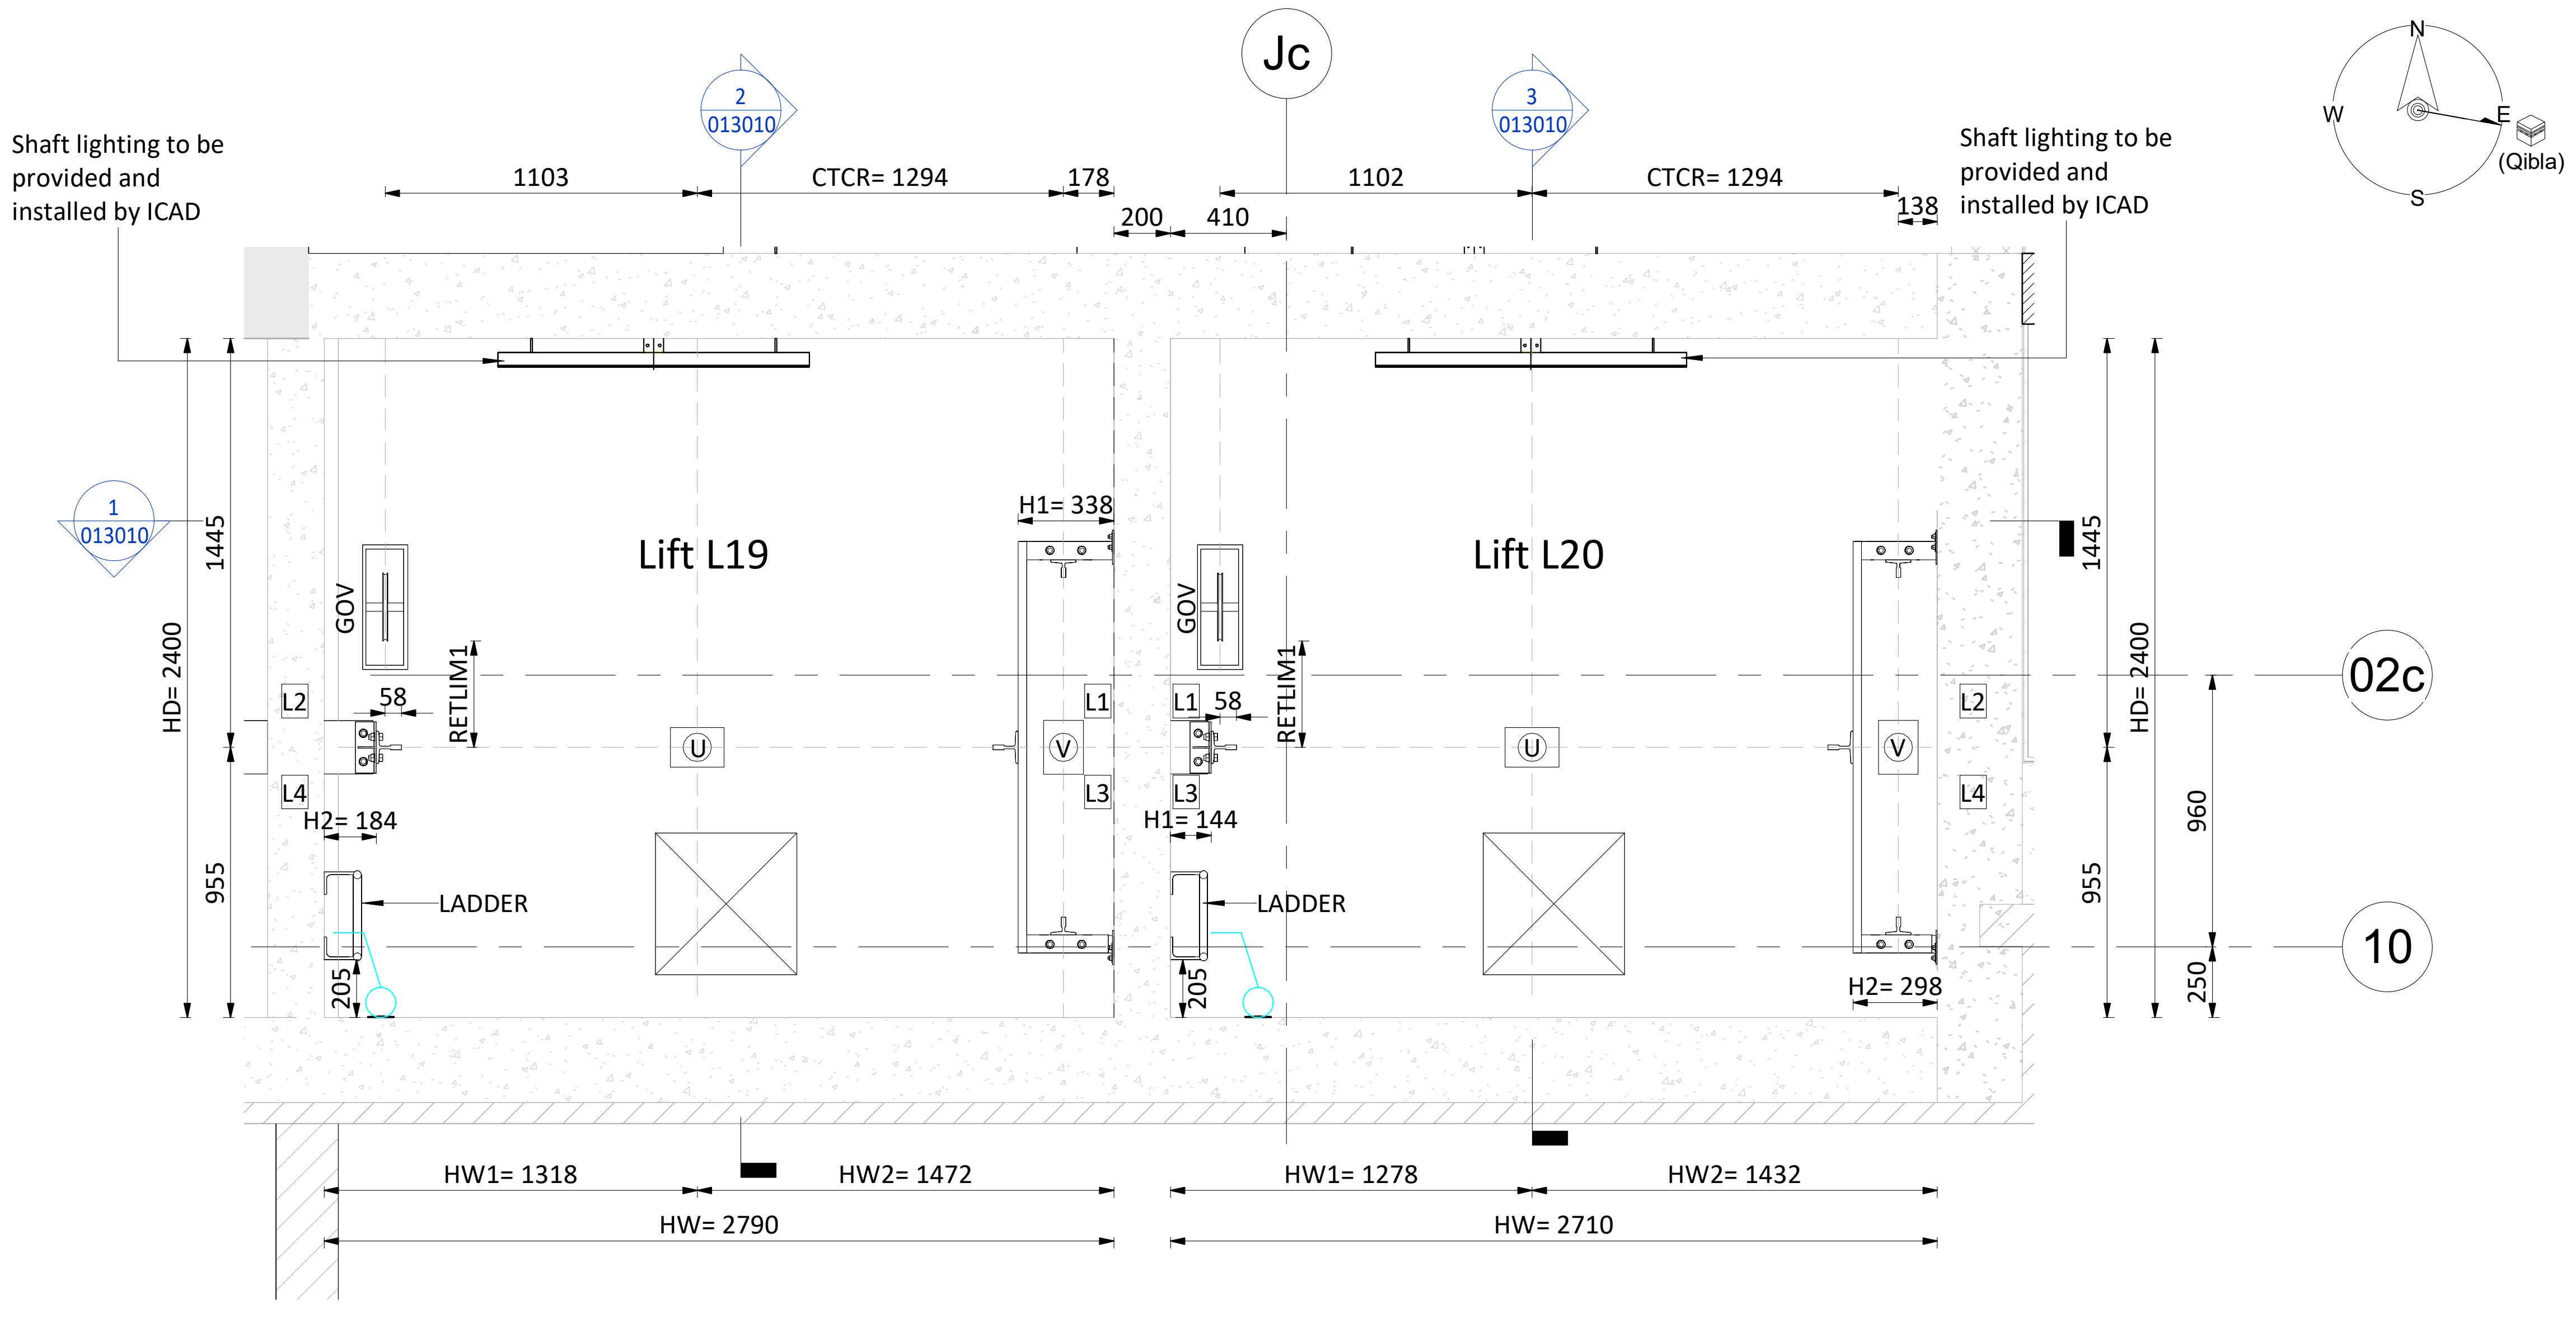

2 Hoist Way Pit Plan Floor - ELEV-L19 & L20

1 : 25

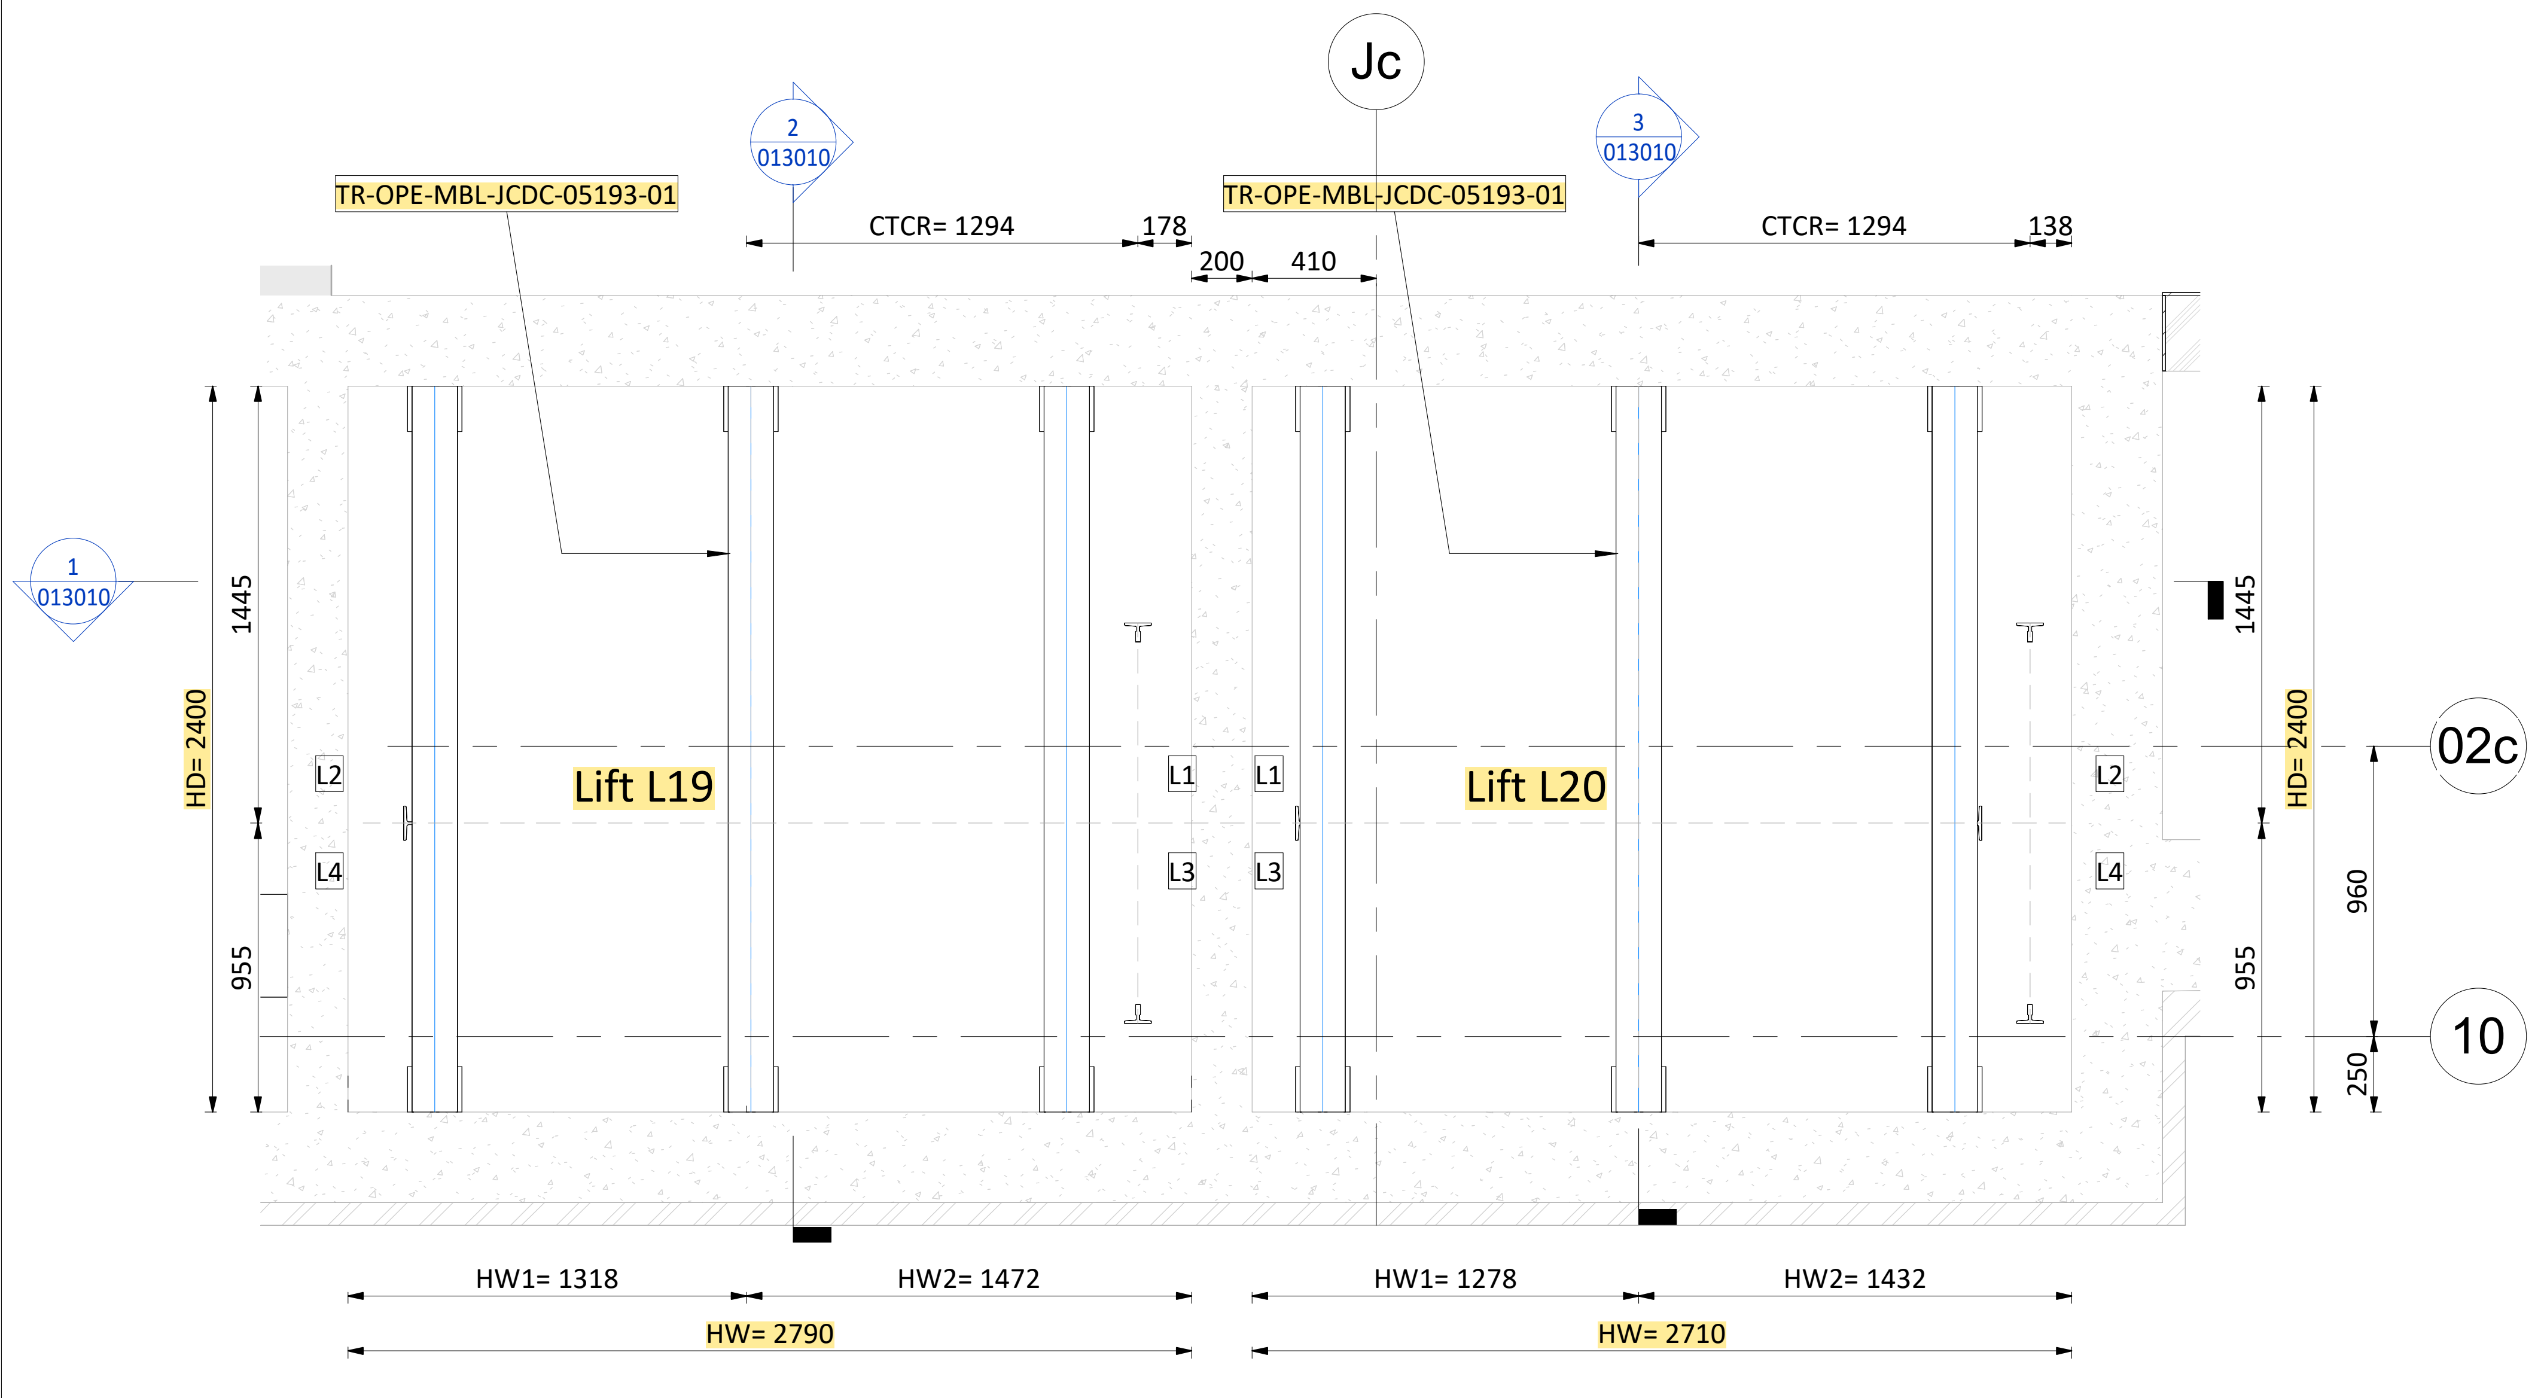

3 Hoist Way Hook Plan Floor - ELEV-L19 & L20

1 : 25

CONTROLLED COPY
MBL IFC
JEDDAH OPERA HOUSE PROJECT
QA/QC Department
MBL QAM
Engr. Mudassar Altaf

SCEC – K&A Reviewed

Civil	Arch.	Elec.	ELV.	Mech.	Acoustic
☒	☒	☒	☐	☒	☒

SCEC – K&A Reviewed
KHATIB & ALAMI
SAUDI CONSOLIDATED ENGINEERING COMPANY
Code B – Approved with Comments
(Do not Resubmit)

Dar Al-Handasah
Checked and Reviewed

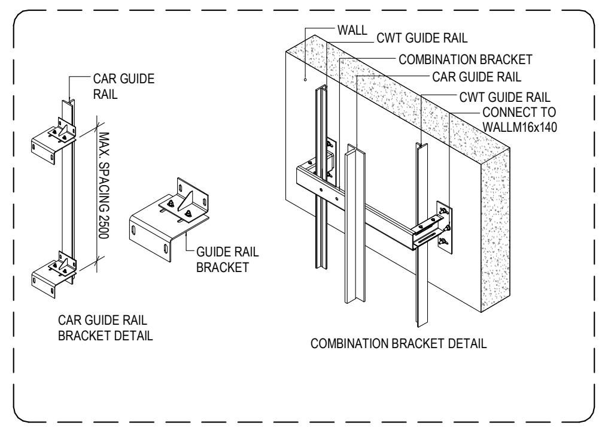

ELEV-L19 & 20 ELEVATOR GENERAL SPECIFICATIONS	
LIFT NUMBER	ELEV.L19 & 20

CABIN INTERNAL SIZE(WXDXH)	2000X1700X2600
CAPACITY	1600 Kg
CLEAR ENTRANCE	1200X2400
CONTROL	VVVF
CONTROL SYSTEM	DUPLEX FULL COLLECTIVE
COUNTERWEIGHT SAFETY	YES
DOOR TYPE	CLD1
EMERGENCY EXITS	-
FRONT OPENING	4
HEAT RELEASE	1616Kcal/h
HOISTWAY SIZE(HWXHD)	2790X2400&2710X2400
LIFT NUMBER	ELV.L19 & 20
LIGHTING SUPPLY	220V 60HZ
MIN.FLOOR HEIGHT	3000
NO. OF FLOOR	4
NO. OF OPENINGS	4
NO. OF UNITS	2
NON-STOP FLOORS	-
NON-STOP FLOORS NAMES	-
NUMBER OF PASSENGERS	21P
OVERHEAD	5400mm
PIT DEPTH	1600mm
POWER SUPPLY	380V 3P 60HZ
PRODUCT NO.	GeN2 MRL
RATED CURRENT(A)	25.6
REAR OPENING	-
ROPING	2:1
SPEED(m/s)	1.00
START CURRENT(A)	28.4
SYSTEM POWER(KW)	13.5
TRAVEL	13825mm
USE	PASSENGER LIFT Public

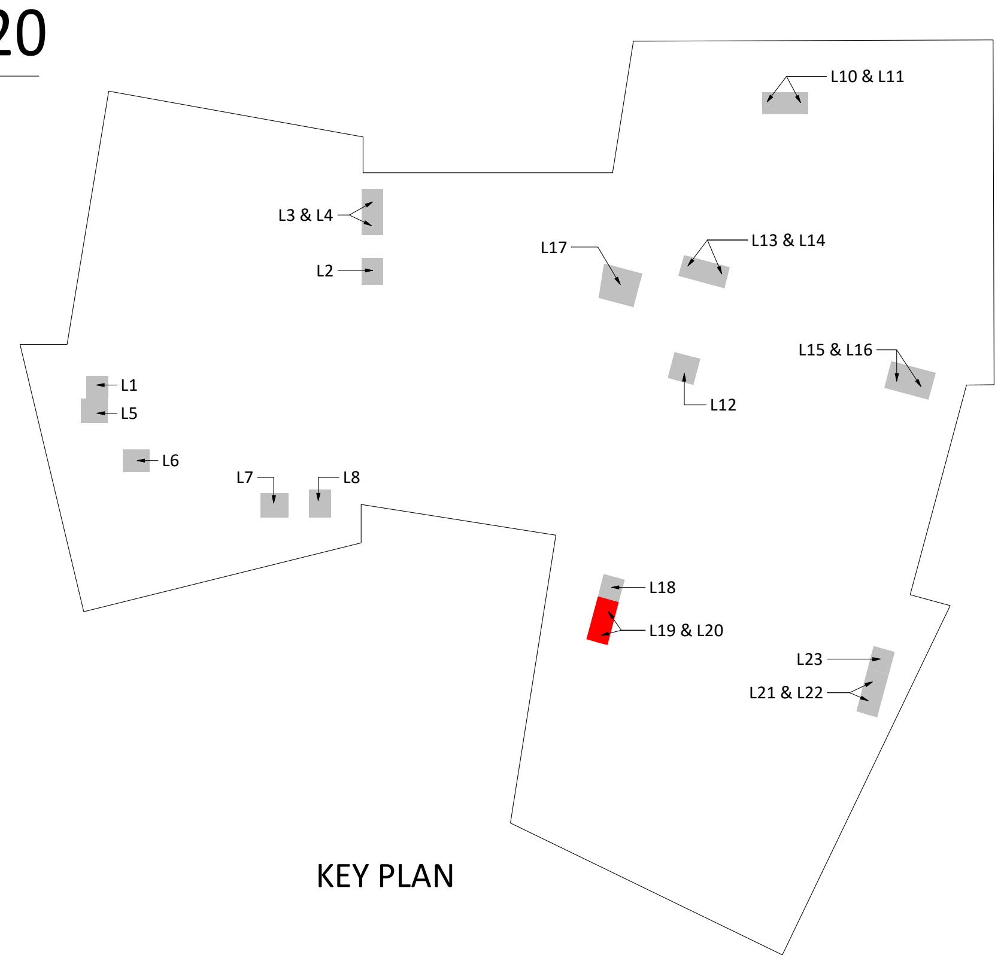

KEY PLAN

REACTIONS FORCE (KN)			
Car side rail	CWT guide rail	Pit reaction	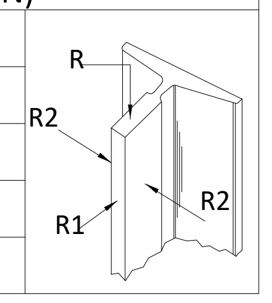
R= 41	R= 48	U= 165	
R1= 2.47	R1= 1.13	V= 132	
R2= 3.14	R2= 0.3		

LEGEND	
HW	HOIST WAY WIDTH
HD	HOIST WAY DEPTH
CRH	CAR ROUGH HEIGHT
DOOR OP	DOOR OPENING
ROP	ROUGH OPENING
CW	CAR WIDTH
CD	CAR DEPTH
CH	CAR HEIGHT
DBG	DISTANCE BETWEEN GUARDRAIL
CWT	COUNTERWEIGHT
E&I PANEL	EMERGENCY & INSPECTION PANEL
G.O.V	CAR GOVERNOR
COP	CAR OPERATING PANEL
HBP	HALL POSITION INDICATOR

NOTE No.:
FRONT WALLS,FINISHES & ARCHITRAVES TO BE BUILT (BY CLIENT) AFTER THE INSTALLATION OF THE (LANDING) EXTERNAL DOORS.

IMPORTANT NOTE FOR MAIN CONTRACTOR.
FREEDOM OF ACCESS MUST BE AVAILABLE FOR POINT OF ENTRY INTO THE BUILDING UP TO THE ELEVATOR HOIST WAY AND THE FRONT WALLS OF THE HOIST WAY AT MAIN FLOOR TO BE LEFT OPEN FOR FULL WIDTH AND HEIGHT TO PERMIT ENTRY OF OUR EQUIPMENT.

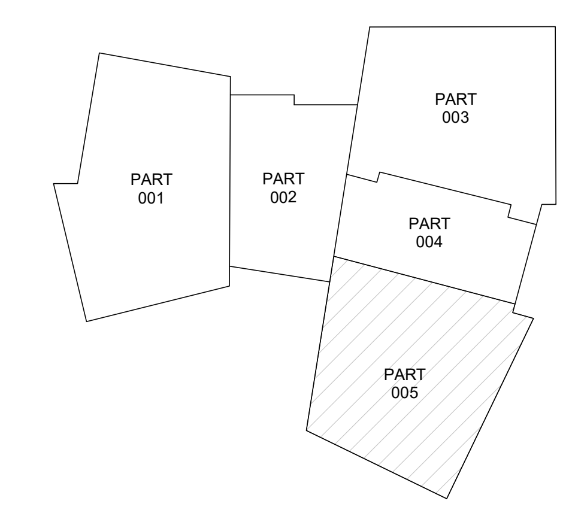

KEY PLAN

GENERAL NOTES: ALL LEVELS SHOWN ON THE DRAWING ARE CHART DATUM LEVELS PROJECT LEVEL+0.000 = +3.700 CHART DATUM.

Refer to :
LIFTS overhead steel hook beams structural calculation and fixation details: TR-OPE-MBL-JCDC-05193-S01
CRS: SD-OPE-MBL-JCDC-01382 - CRS - version-(0_00)-L19,20
Electrical Panels distribution:
JOH-ICD-S5-01-056-005-02-SD-EL-011625
JOH-ICD-S5-01-056-XXX-03-SD-EL-011630_1
wiring diagram opera lift
Acoustic Letter: L-OTIS-MBL-OPE-26-0015

DRAWING / DOCUMENT REFERENCE

NO.	NUMBER	TITLE	REV.
01	L-19 & L-20	JOH-HLA-S4-01-056-005-00-DR-AR-011105	F00
02		JOH-BHC-S4-01-056-XXX-XX-DR-VT-015001	
03		JOH-BHC-S4-01-056-XXX-XX-DR-VT-010001	
04		JOH-BHC-S4-01-056-005-ZZ-DR-VT-013001	
05		JOH-BHC-S4-01-056-005-ZZ-DR-VT-011001	
06		TQ-OPE-MBL-JCDC-00222	
07		TQ-OPE-MBL-JCDC-01258	
08		JCD-OPE-MBL-MR-003-NMR-601-03	
09		JCD-OPE-MBL-MR-003-NMR-602-01	
10		TR-OPE-MBL-JCDC-05193-01	

REVIEWED BY DISCIPLINE	SIGNATURE	DATE
ARCHITECTURAL	MT	[illegible]
STRUCTURAL	PC	[illegible]
MECHANICAL	ShA	[illegible]
PLUMBING	[illegible]	[illegible]
ELECTRICAL	ShA	2026-05-20
ICT	ShA	[illegible]
ADDITIONAL DISCIPLINES TO BE ADDED AS REQUIRED		

REV	DATE	BY	DESCRIPTION	CHK	APD
S01	07-MAY-2026	AK	Shop Drawing	SS	AB
S00	06-MAY-2026	AK	Issued for Approval	SS	AB

DRAWING STATUS:
CONSTRUCTION SHOPDRAWING

CLIENT:
شركة وسط جدة للتطوير
Jeddah Central Development Co.

LEAD DESIGN CONSULTANTS: Henning Larsen

LEAD ENGINEERING CONSULTANT: BURO HAPPOLD

PROJECT SUPERVISION CONSULTANT: KHATIB & ALAMI

GENERAL CONTRACTOR: MBL

REVIEWER: dar

SUB CONTRACTOR: OTIS ELEVATOR COMPANY SAUDI ARABIA LIMITED OTIS

PROJECT
JEDDAH OPERA HOUSE

TITLE:
OPERA BUILDING
VERTICAL TRANSPORTATION
PART 005
PLANS - LIFT SHAFT SHEET 02 OF 02 (L19 & L20)

SCALE @ A1:	CHECKED:		APPROVED:
1:25	SS		AB
PROJECT No:	DESIGNED:	DRAWN:	DATE:
440014	AK	PR	07-MAY-2026

DRAWING No: JOH-OTS-S5-01-056-005-ZZ-SD-VT-011011
REV: S01

MODEL FILE REF: JOH-OTS-S5-01-056-XXX-ZZ-M3-VT-010001

ⓒ JCDC

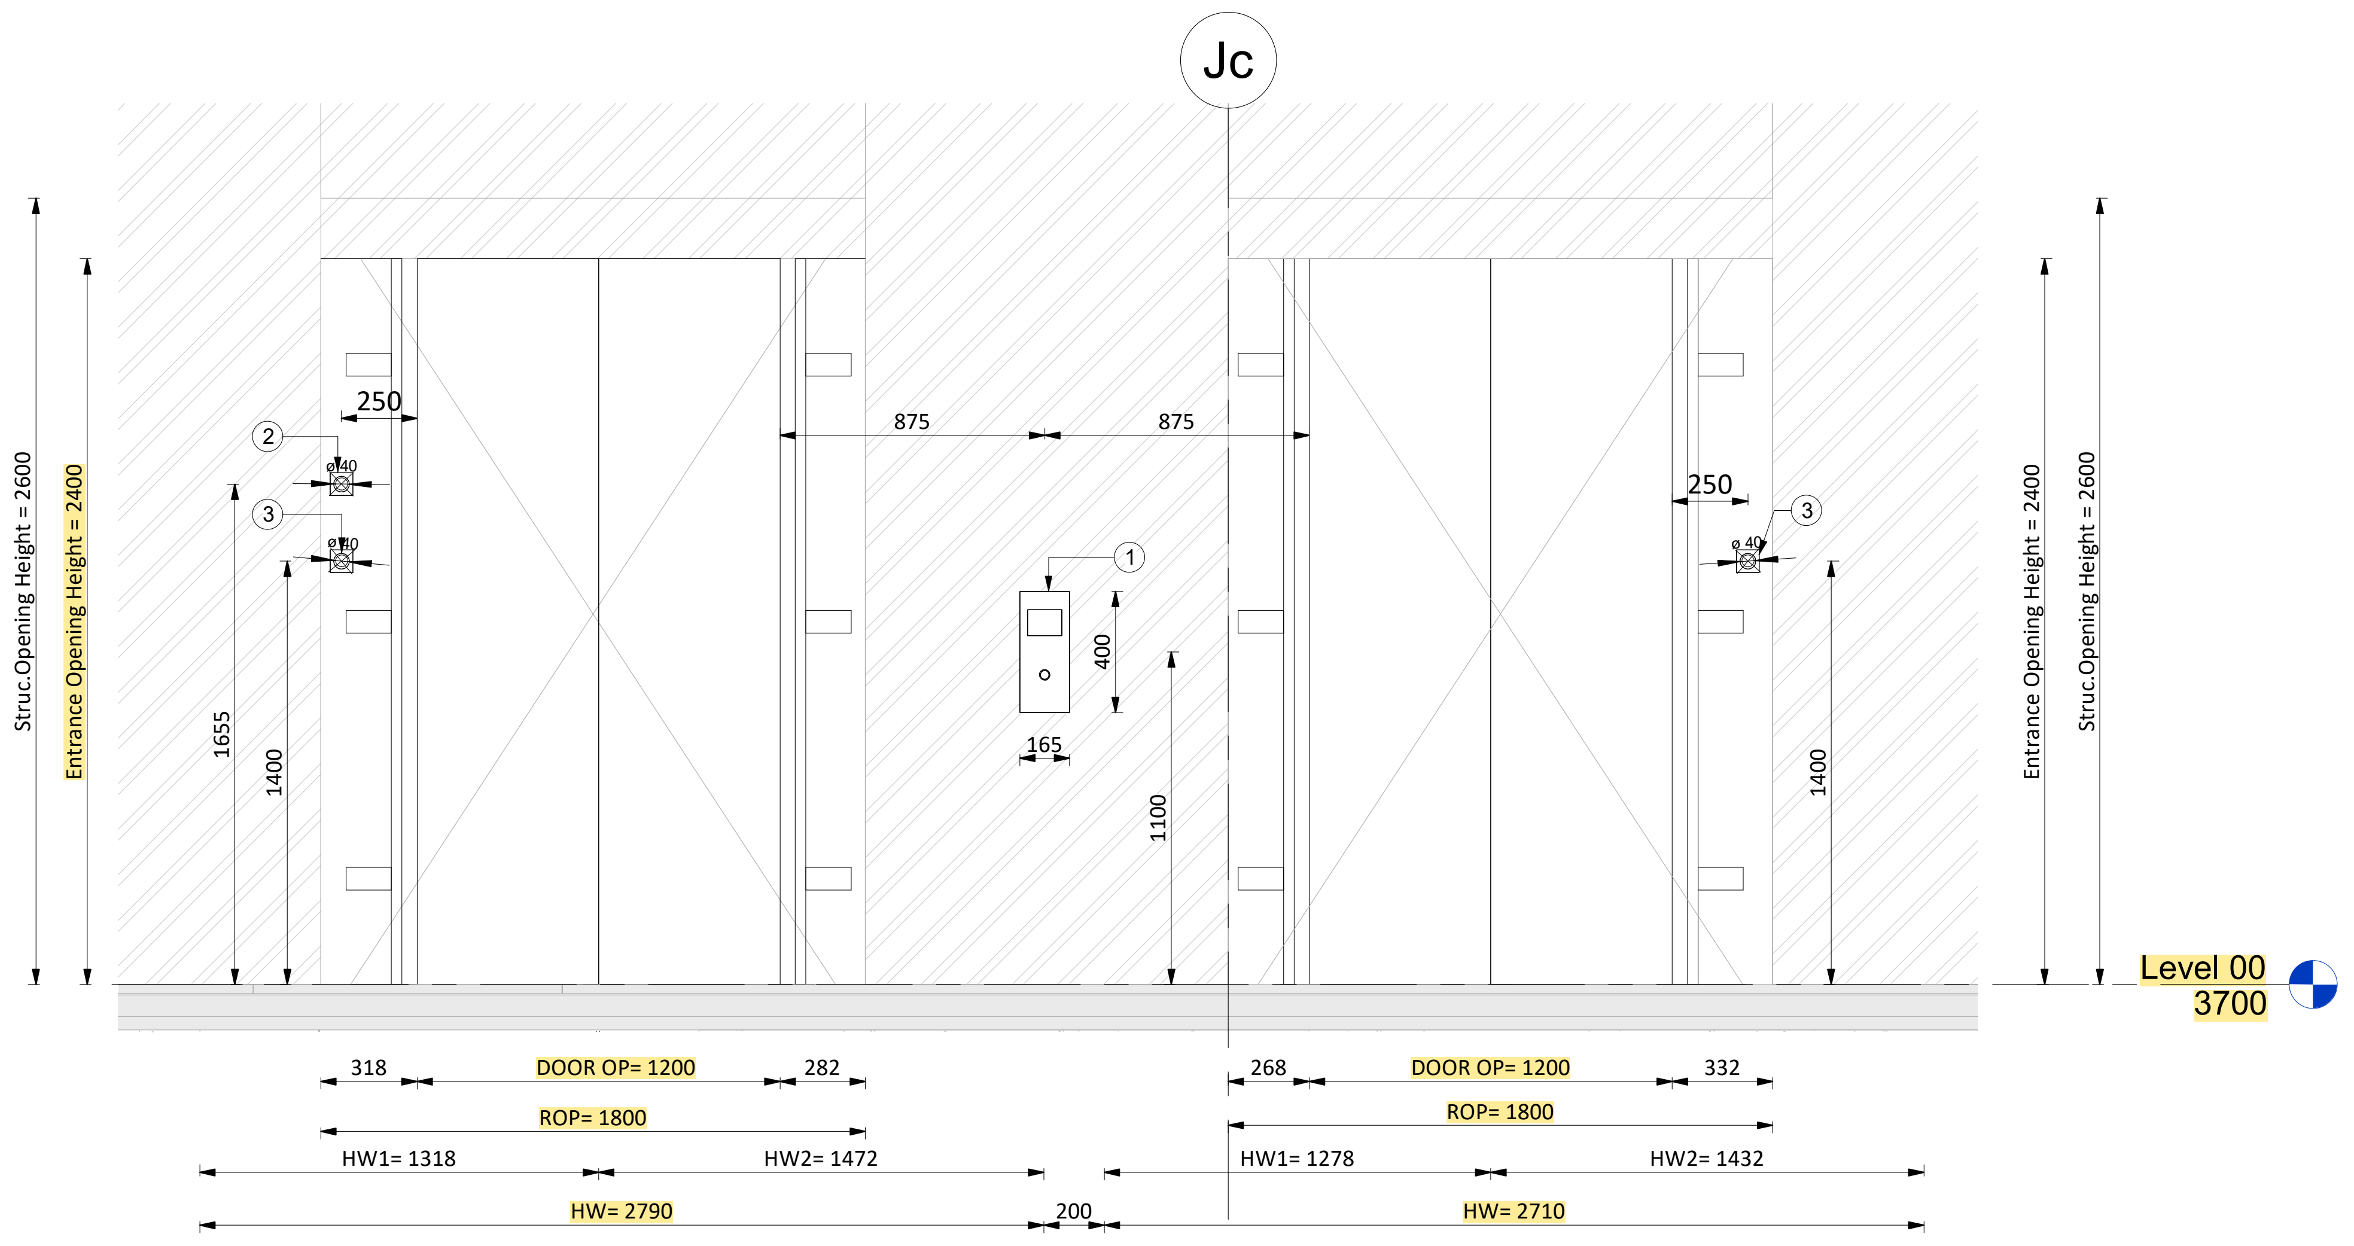

1 Door Elevation At "G" Floor - ELEV-L19 & L20
1 : 25

1.HALL BUTTON(HBP)
165 X 400 THROUGH HOLE ,IN THE DISCRETIONARY FLOOR
2.FIREMAN SERVICE (FSS)
Φ40mm THROUGH HOLE, IN THE MAIN FLOOR
3. PIT INSPECTION RESET SW
Φ40mm ONLY FOR PIT LANDING
4. E&I PANEL.

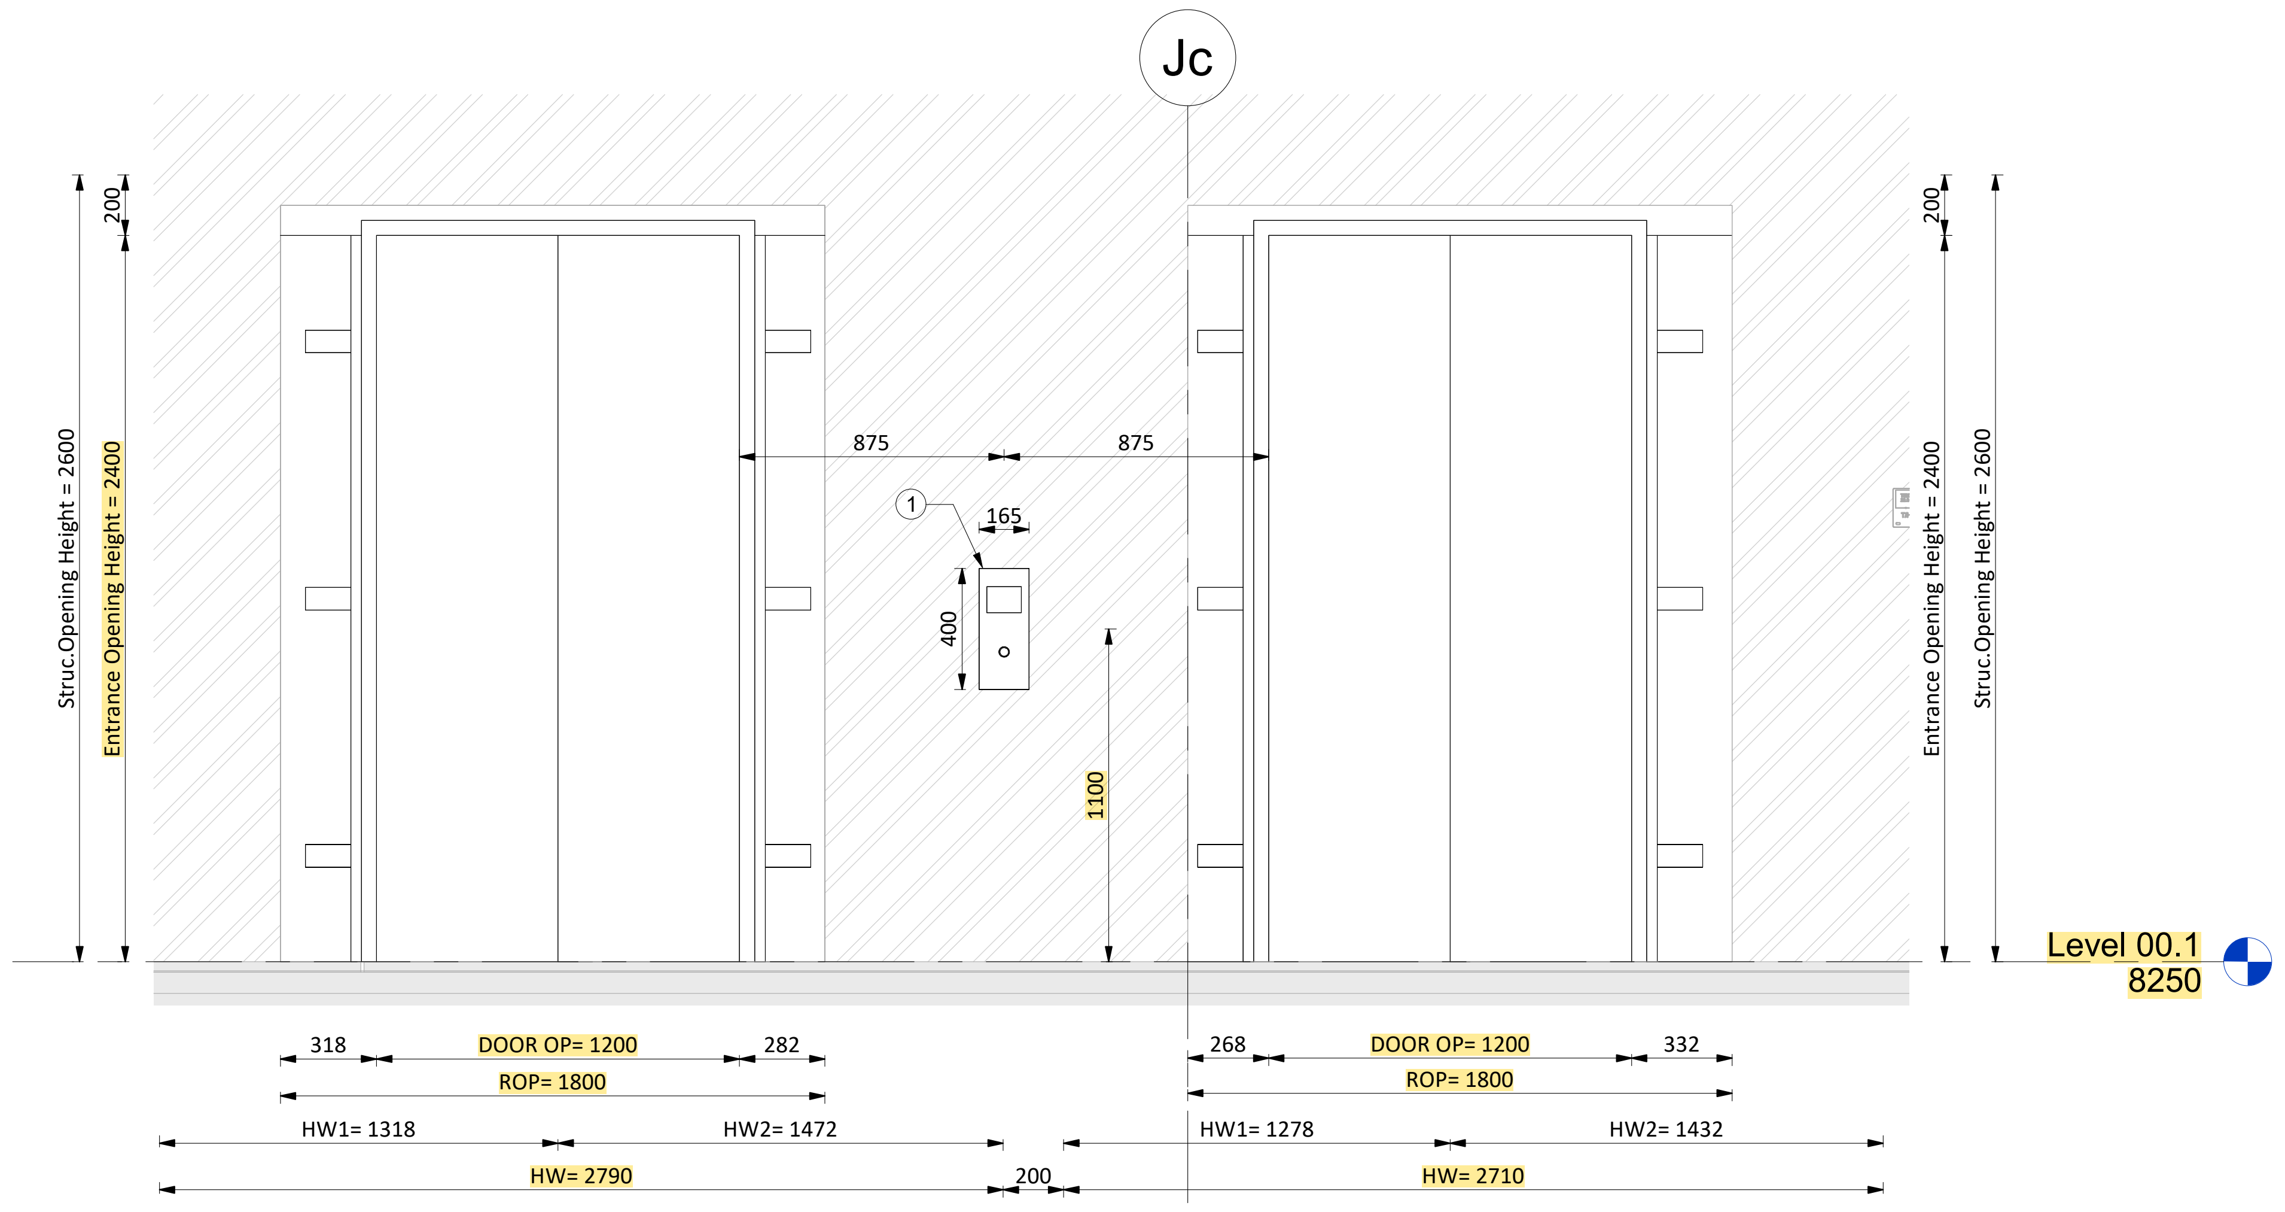

2 Door Elevation At "Typical" Floor - ELEV-L19 & L20
1 : 25

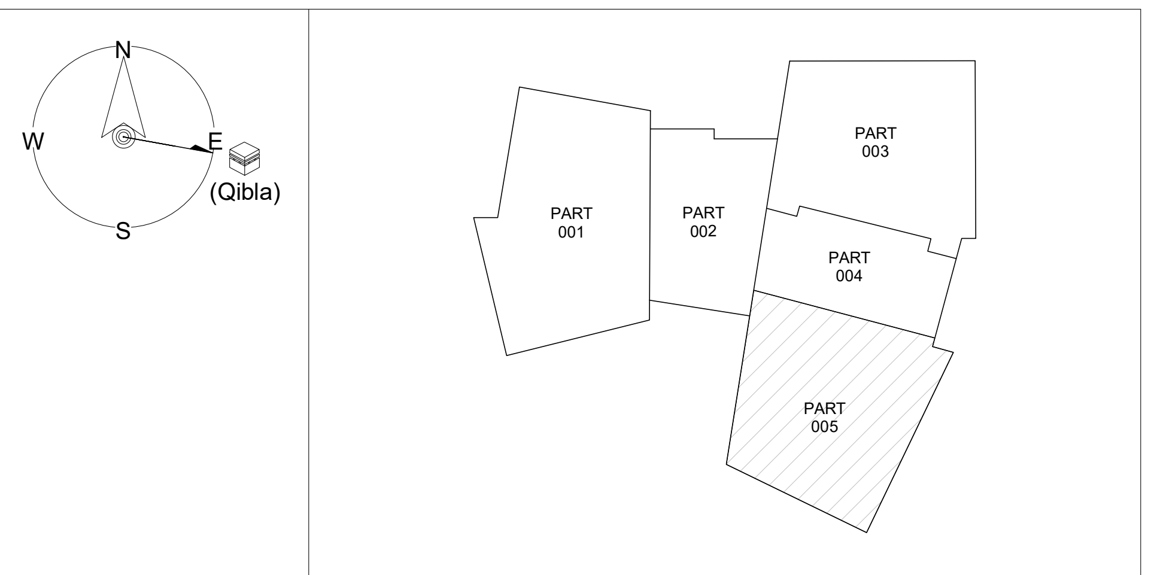

KEY PLAN

GENERAL NOTES: ALL LEVELS SHOWN ON THE DRAWING ARE CHART DATUM LEVELS PROJECT LEVEL+0.000 = +3.700 CHART DATUM.

Refer to :
LIFTS overhead steel hook beams structural
calculation and fixation details: TR-OPE-MBL-JCDC-05193-S01
CRS: SD-OPE-MBL-JCDC-01382 - CRS - version-(0_00)-L19,20
Electrical Panels distribution:
JOH-ICD-S5-01-056-005-02-SD-EL-011625
JOH-ICD-S5-01-056-XXX-03-SD-EL-011630_1
wiring diagram opera lift
Acoustic Letter: L-OTIS-MBL-OPE-26-0015

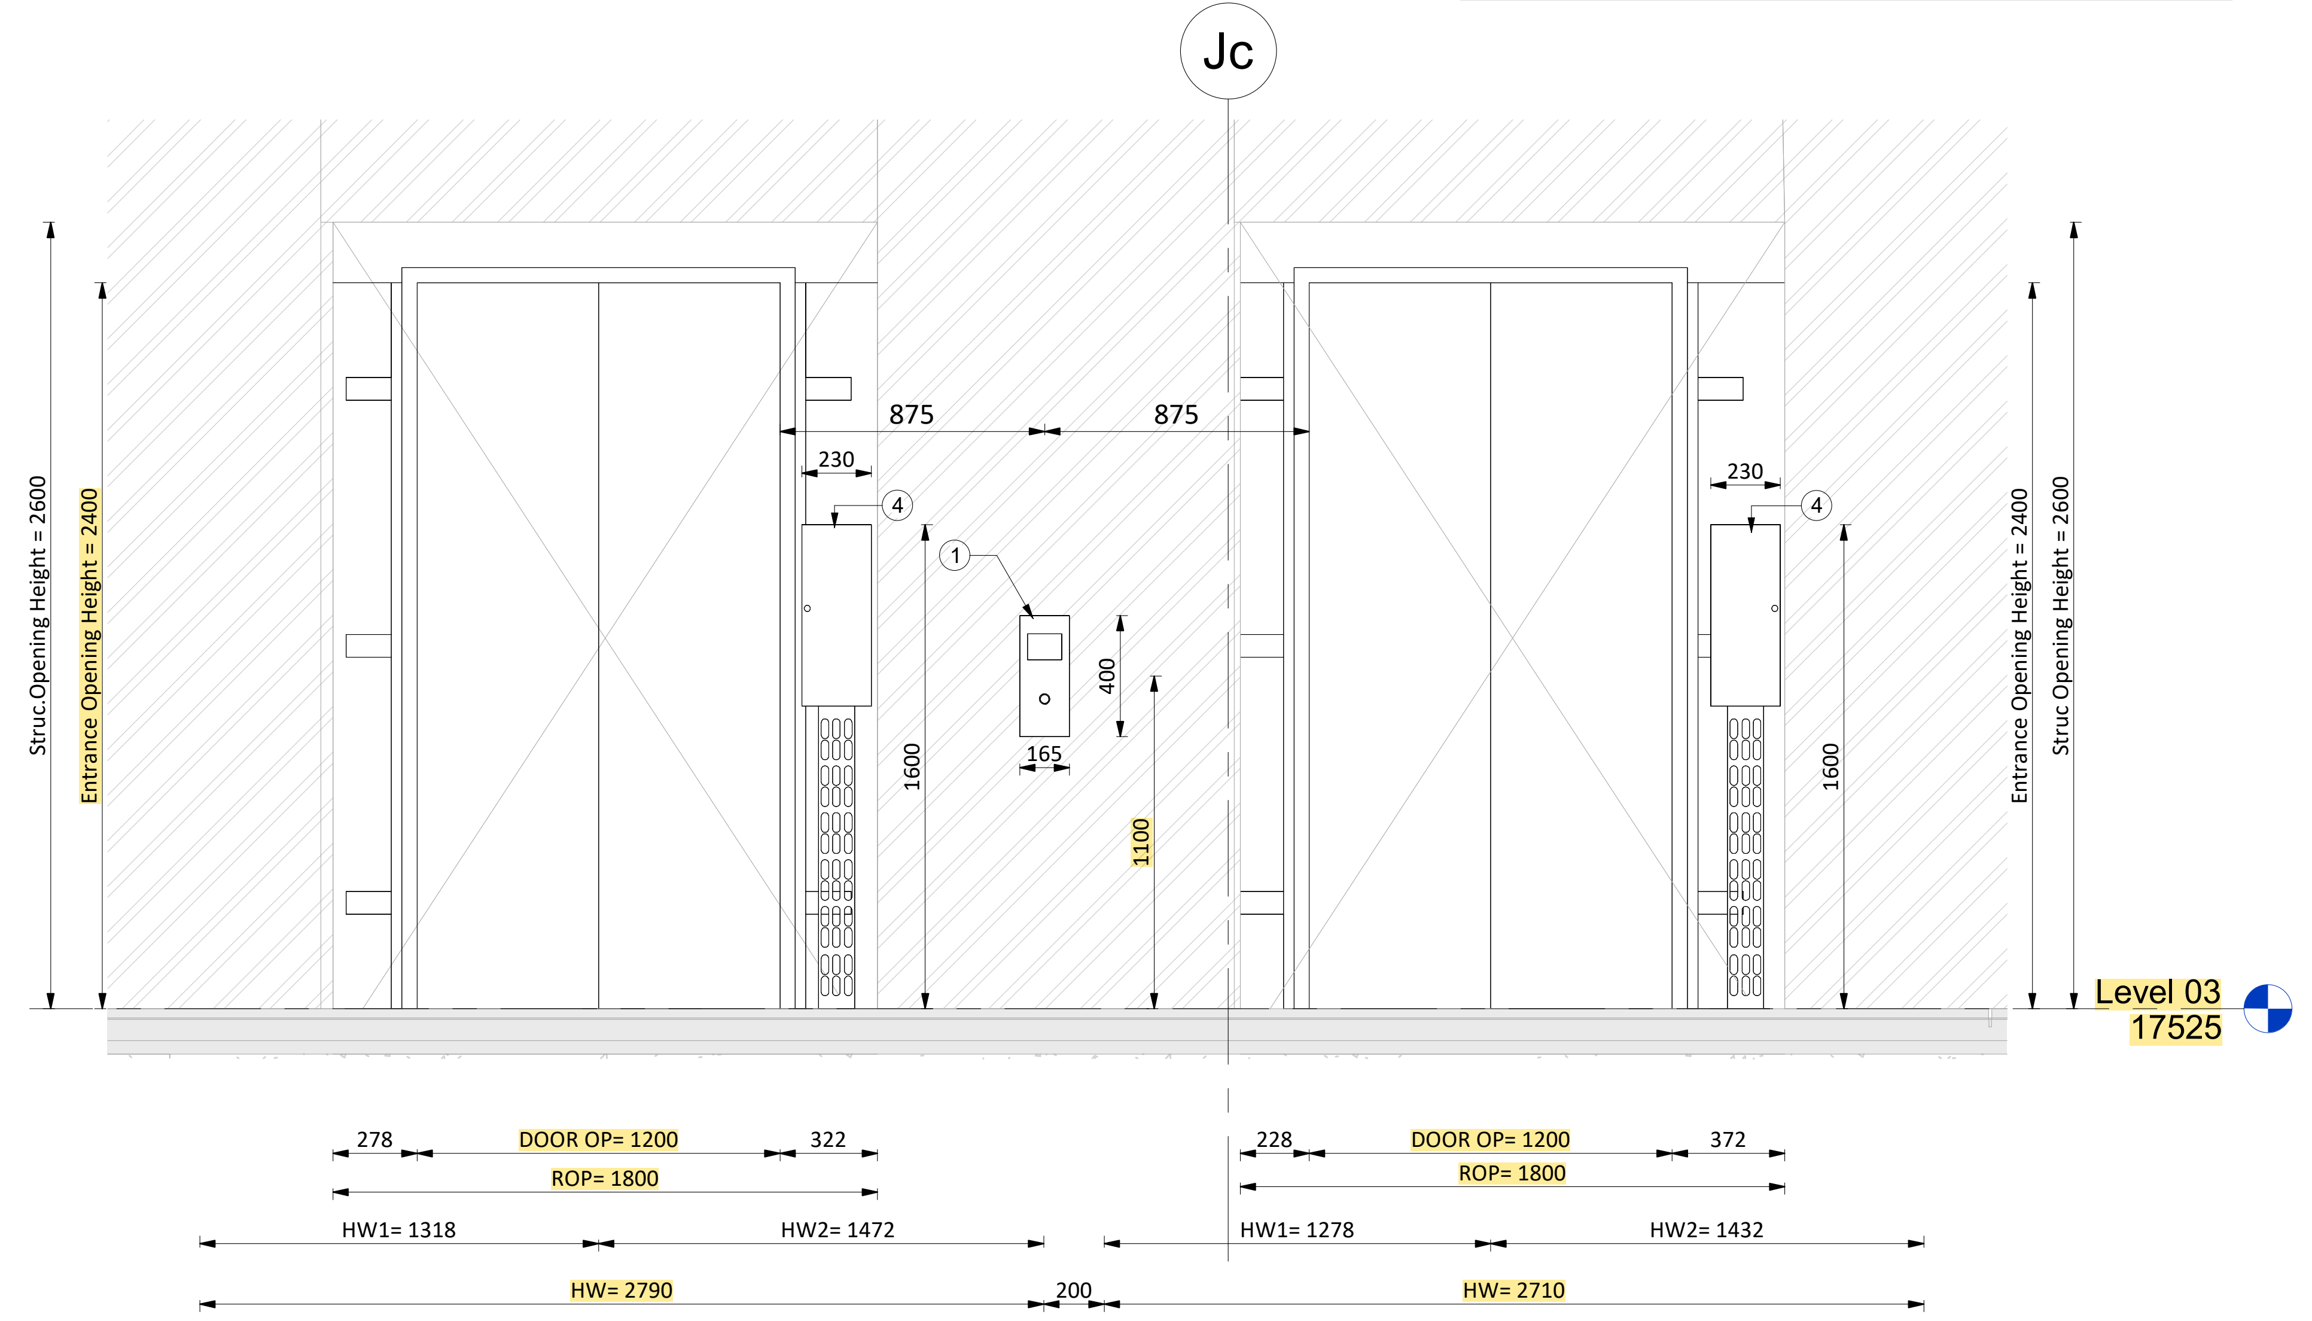

3 Door Elevation At "3" Floor - ELEV-L19 & L20
1 : 25

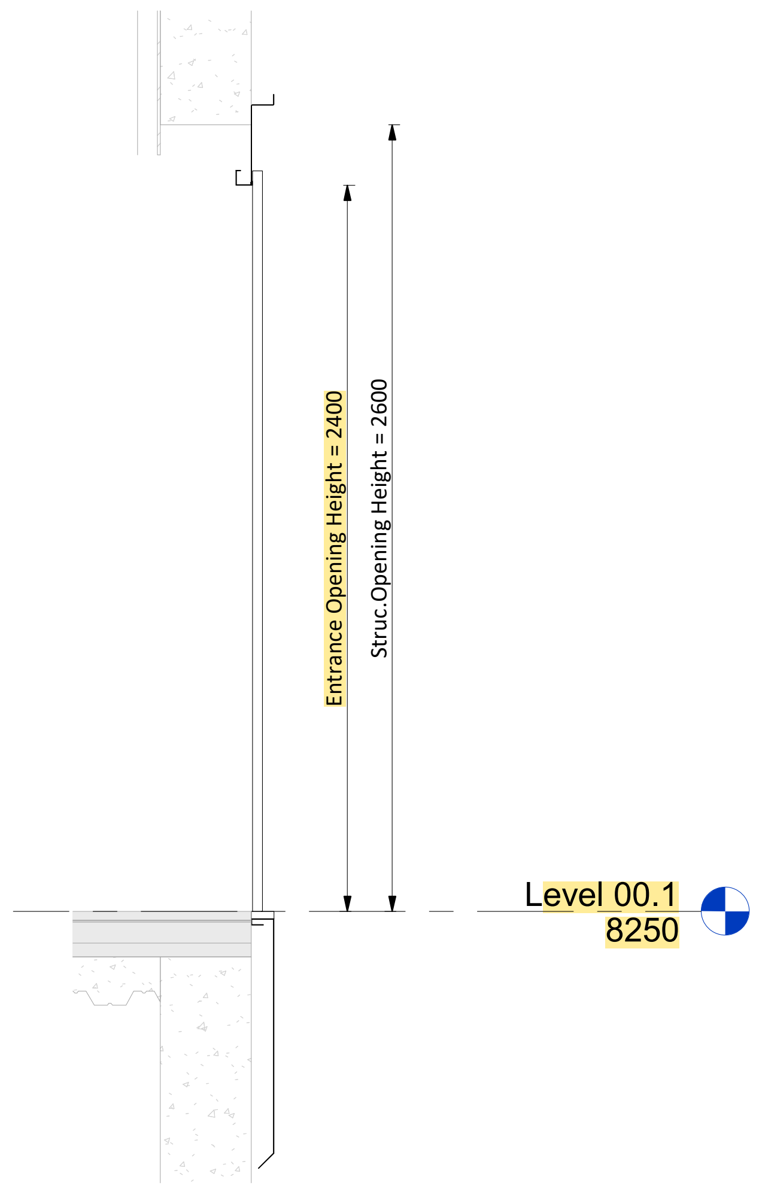

4 Cross-Section View A-A - ELEV-L19 & L20
1 : 25

Duplex Units

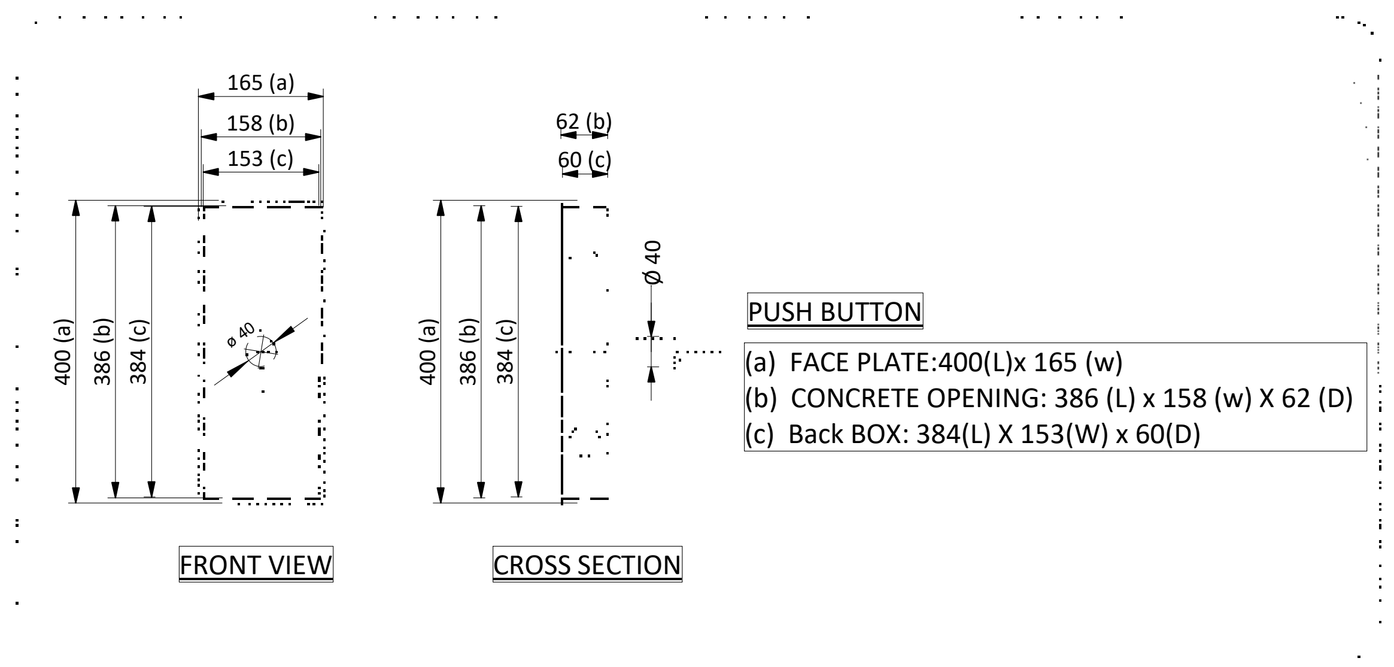

PUSH BUTTON
(a) FACE PLATE:400(L)x 165 (w)
(b) CONCRETE OPENING: 386 (L) x 158 (w) X 62 (D)
(c) Back BOX: 384(L) X 153(W) x 60(D)

SCEC – K&A Reviewed

Civil	Arch.	Elec.	ELV.	Mech.	Acoustic
☒	☒	☒	☐	☒	☒

CONTROLLED COPY
MBL IFC
JEDDAH OPERA HOUSE PROJECT
QA/QC Department
MBL QAM
Engr. Mudassar Altaf

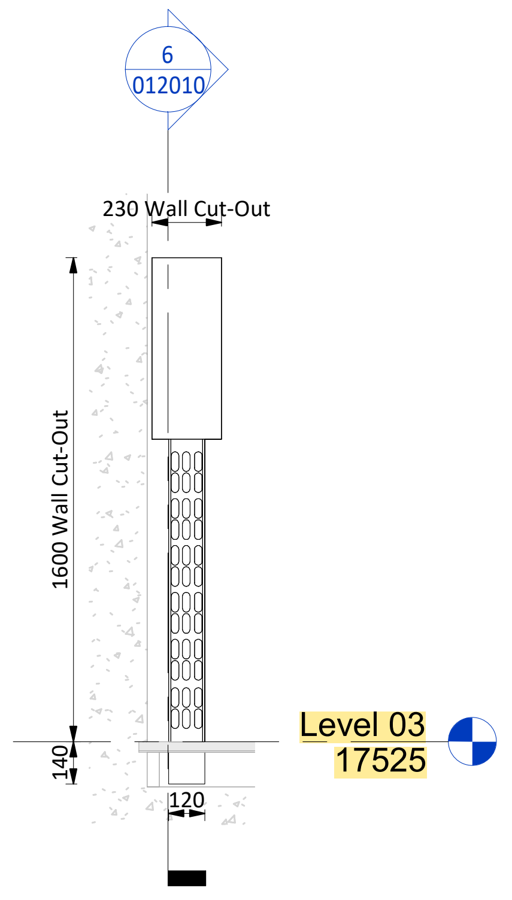

5 E&I SPOT DETAIL - ELEV-L19 & L20
1 : 25

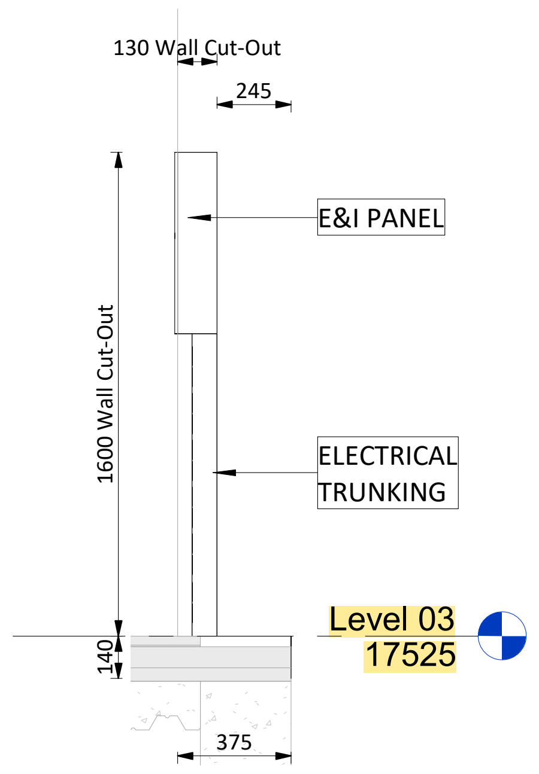

6 Cross-Section View B-B - ELEV-L19 & L20
1 : 25

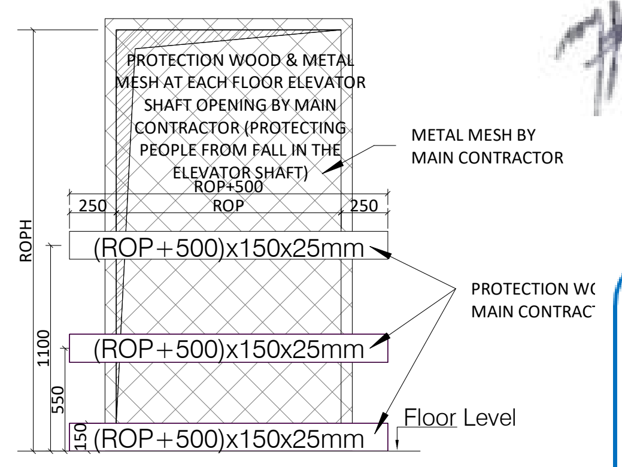
PROTECTION WOOD & METAL MESH AT EACH FLOOR ELEVATOR SHAFT OPENING BY MAIN CONTRACTOR (PROTECTING PEOPLE FROM FALL IN THE ELEVATOR SHAFT)
METAL MESH BY MAIN CONTRACTOR
ROP+500
ROP
250
250
ROPH
(ROP+500)x150x25mm
(ROP+500)x150x25mm
(ROP+500)x150x25mm
PROTECTION WO
MAIN CONTRAC
1100
550
150
Floor Level

Protection Elevation Detail
At Each Elevator Shaft Opening

SCEC – K&A
Reviewed
KHATIB & ALAMI
SAUDI CONSOLIDATED ENGINEERING COMPANY
Code B – Approved with Comments
(Do not Resubmit)

Dar Al-Handasah
consultants (Shair and Partners)
Checked and Reviewed

LEGEND

HW	HOIST WAY WIDTH
HD	HOIST WAY DEPTH
CRH	CAR ROUGH HEIGHT
DOOR OP	DOOR OPENING
ROP	ROUGH OPENING
CW	CAR WIDTH
CD	CAR DEPTH
CH	CAR HEIGHT
DBG	DISTANCE BETWEEN GUARDRAIL
CWT	COUNTERWEIGHT
E&I PANEL	EMERGENCY & INSPECTION PANEL
G.O.V	CAR GOVERNOR
COP	CAR OPERATING PANEL
HBP	HALL POSITION INDICATOR

DRAWING / DOCUMENT REFERENCE

NO.	NUMBER	TITLE	REV.
01	L-19 & L-20	JOH-HLA-S4-01-056-005-00-DR-AR-011105	F00
02		JOH-BHC-S4-01-056-XXX-XX-DR-VT-015001	
03		JOH-BHC-S4-01-056-XXX-XX-DR-VT-010001	
04		JOH-BHC-S4-01-056-005-ZZ-DR-VT-013001	
05		JOH-BHC-S4-01-056-005-ZZ-DR-VT-011001	
06		TQ-OPE-MBL-JCDC-00222	
07		TQ-OPE-MBL-JCDC-01258	
08		JCD-OPE-MBL-MR-003-NMR-601-03	
09		JCD-OPE-MBL-MR-003-NMR-602-01	
10		TR-OPE-MBL-JCDC-05193-01	

REVIEWED BY DISCIPLINE	SIGNATURE	DATE
ARCHITECTURAL	MT	[illegible]
STRUCTURAL	PC	[illegible]
MECHANICAL	Sh.A	[illegible]
PLUMBING	[illegible]	[illegible]
ELECTRICAL	Sh.A	2026-05-20
ICT	Sh.A	[illegible]
ADDITIONAL DISCIPLINES TO BE ADDED AS REQUIRED		

REV	DATE	BY	DESCRIPTION	CHK	APD
S01	07-MAY-2026	AK	Shop Drawing	SS	AB
S00	06-MAY-2026	AK	Issued for Approval	SS	AB

DRAWING STATUS:
CONSTRUCTION SHOPDRAWING

CLIENT:
شركة وسط جدة للتطوير
Jeddah Central Development Co.

LEAD DESIGN CONSULTANTS: Henning Larsen
LEAD ENGINEERING CONSULTANT: BURO HAPPOLD
PROJECT SUPERVISION CONSULTANT: KHATIB & ALAMI
GENERAL CONTRACTOR: MBL
REVIEWER: dar
SUB CONTRACTOR: OTIS ELEVATOR COMPANY SAUDI ARABIA LIMITED OTIS

PROJECT
JEDDAH OPERA HOUSE

TITLE:
OPERA BUILDING
VERTICAL TRANSPORTATION
PART 005
ELEVATIONS - LIFT SHAFT (L19 & L20)

SCALE @ A1: As Indicated	CHECKED: SS		APPROVED: AB
PROJECT No: 440014	DESIGNED: AK	DRAWN: PR	DATE: 07-MAY-2026

DRAWING No: JOH-OTS-S5-01-056-005-ZZ-SD-VT-012010
REV: S01

MODEL FILE REF: JOH-OTS-S5-01-056-XXX-ZZ-M3-VT-010001

© JCDC

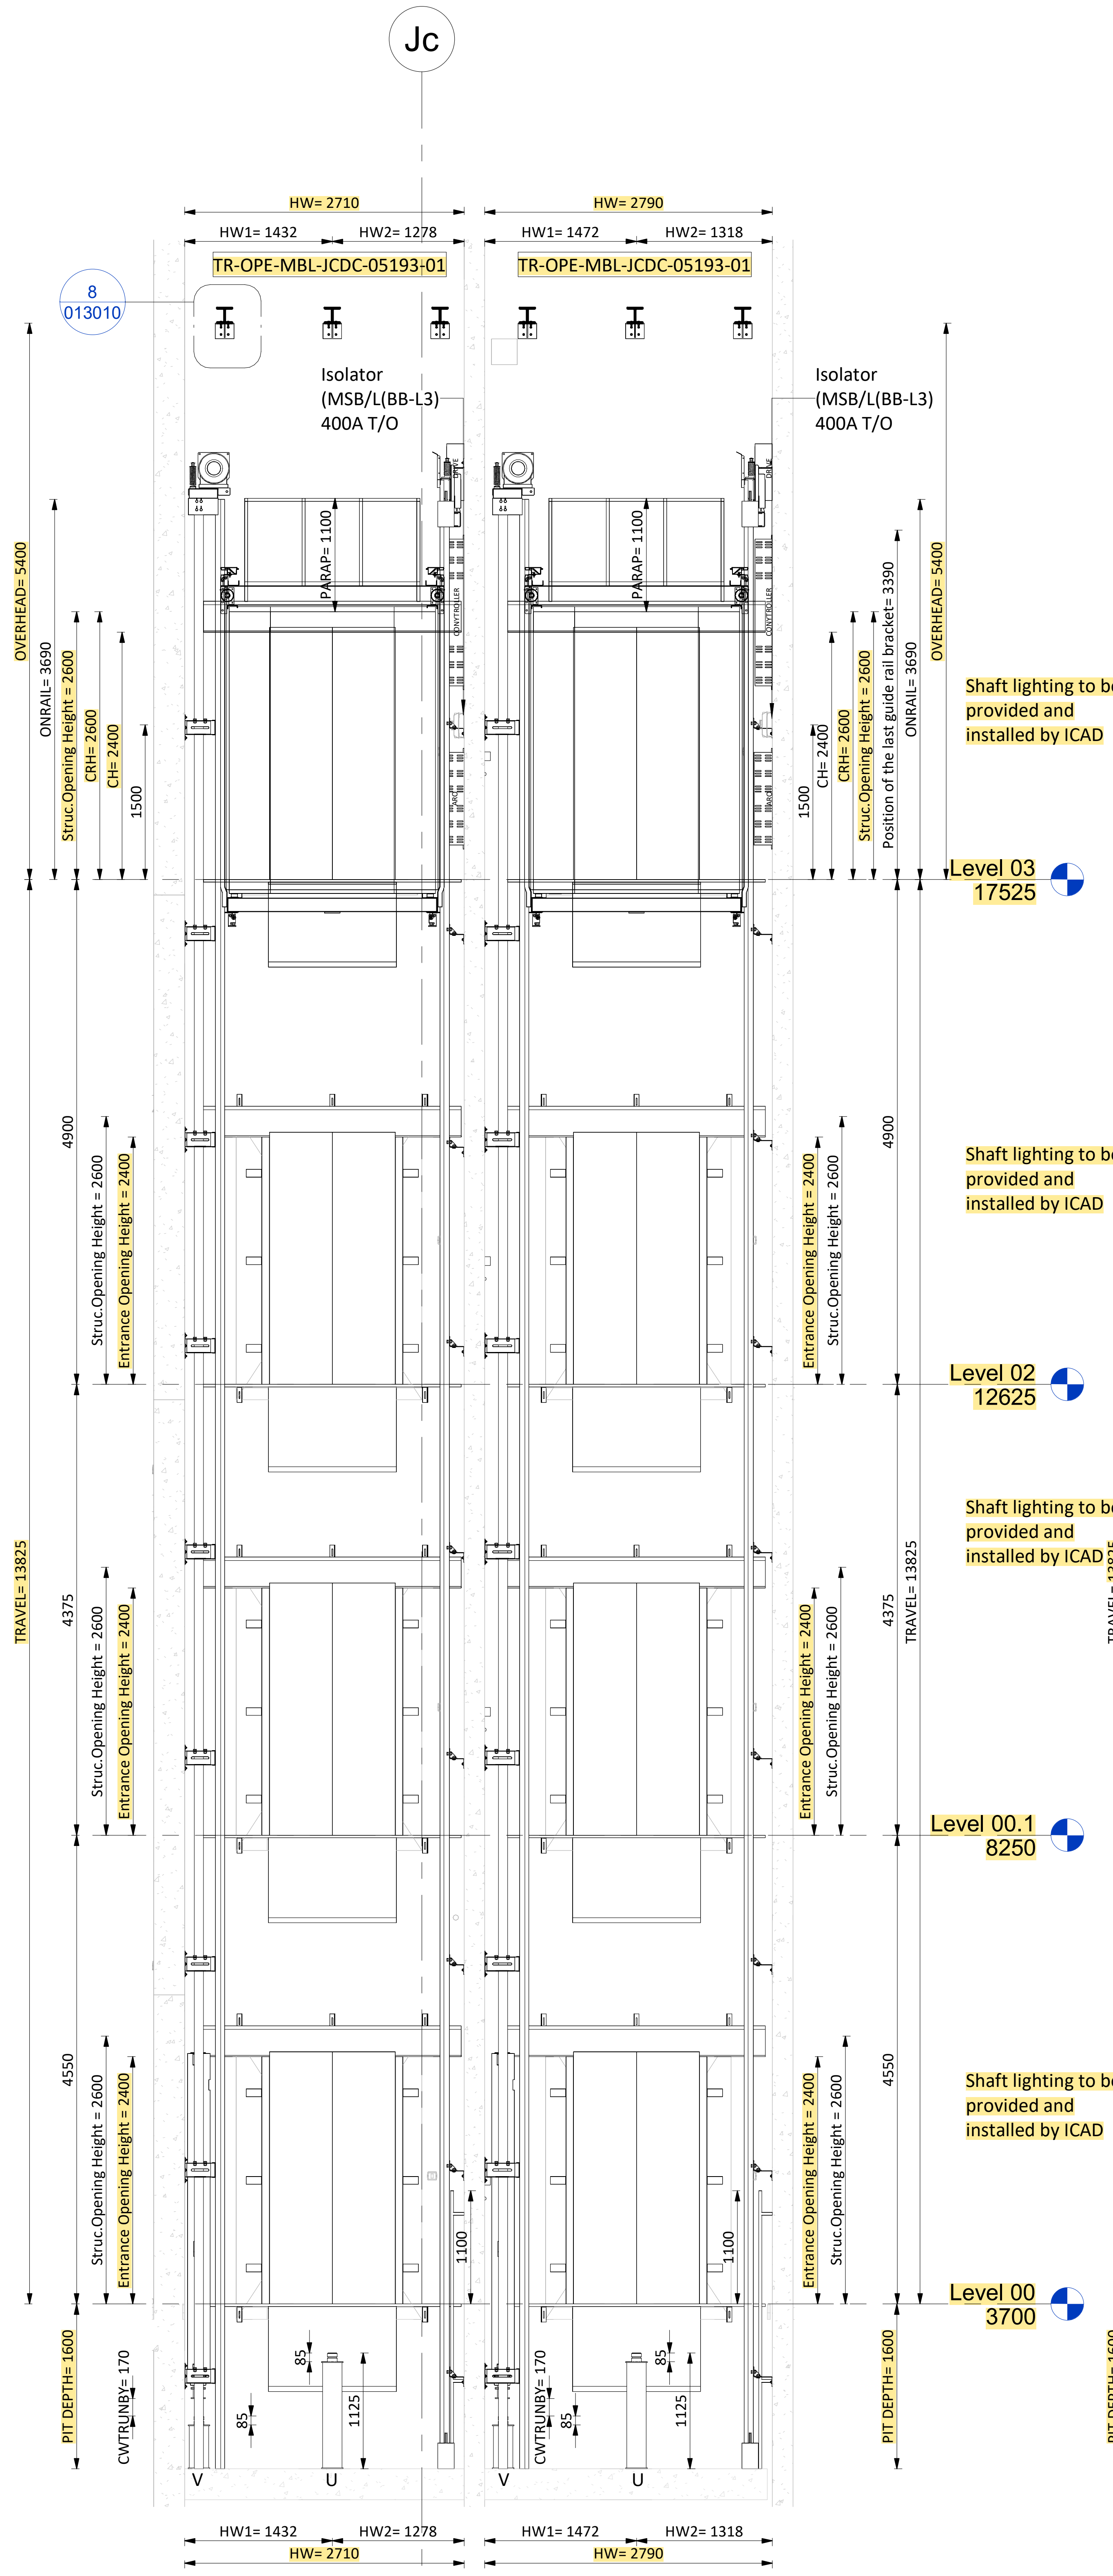

1 Section "A" - ELEV-L19 & L20

1 : 50

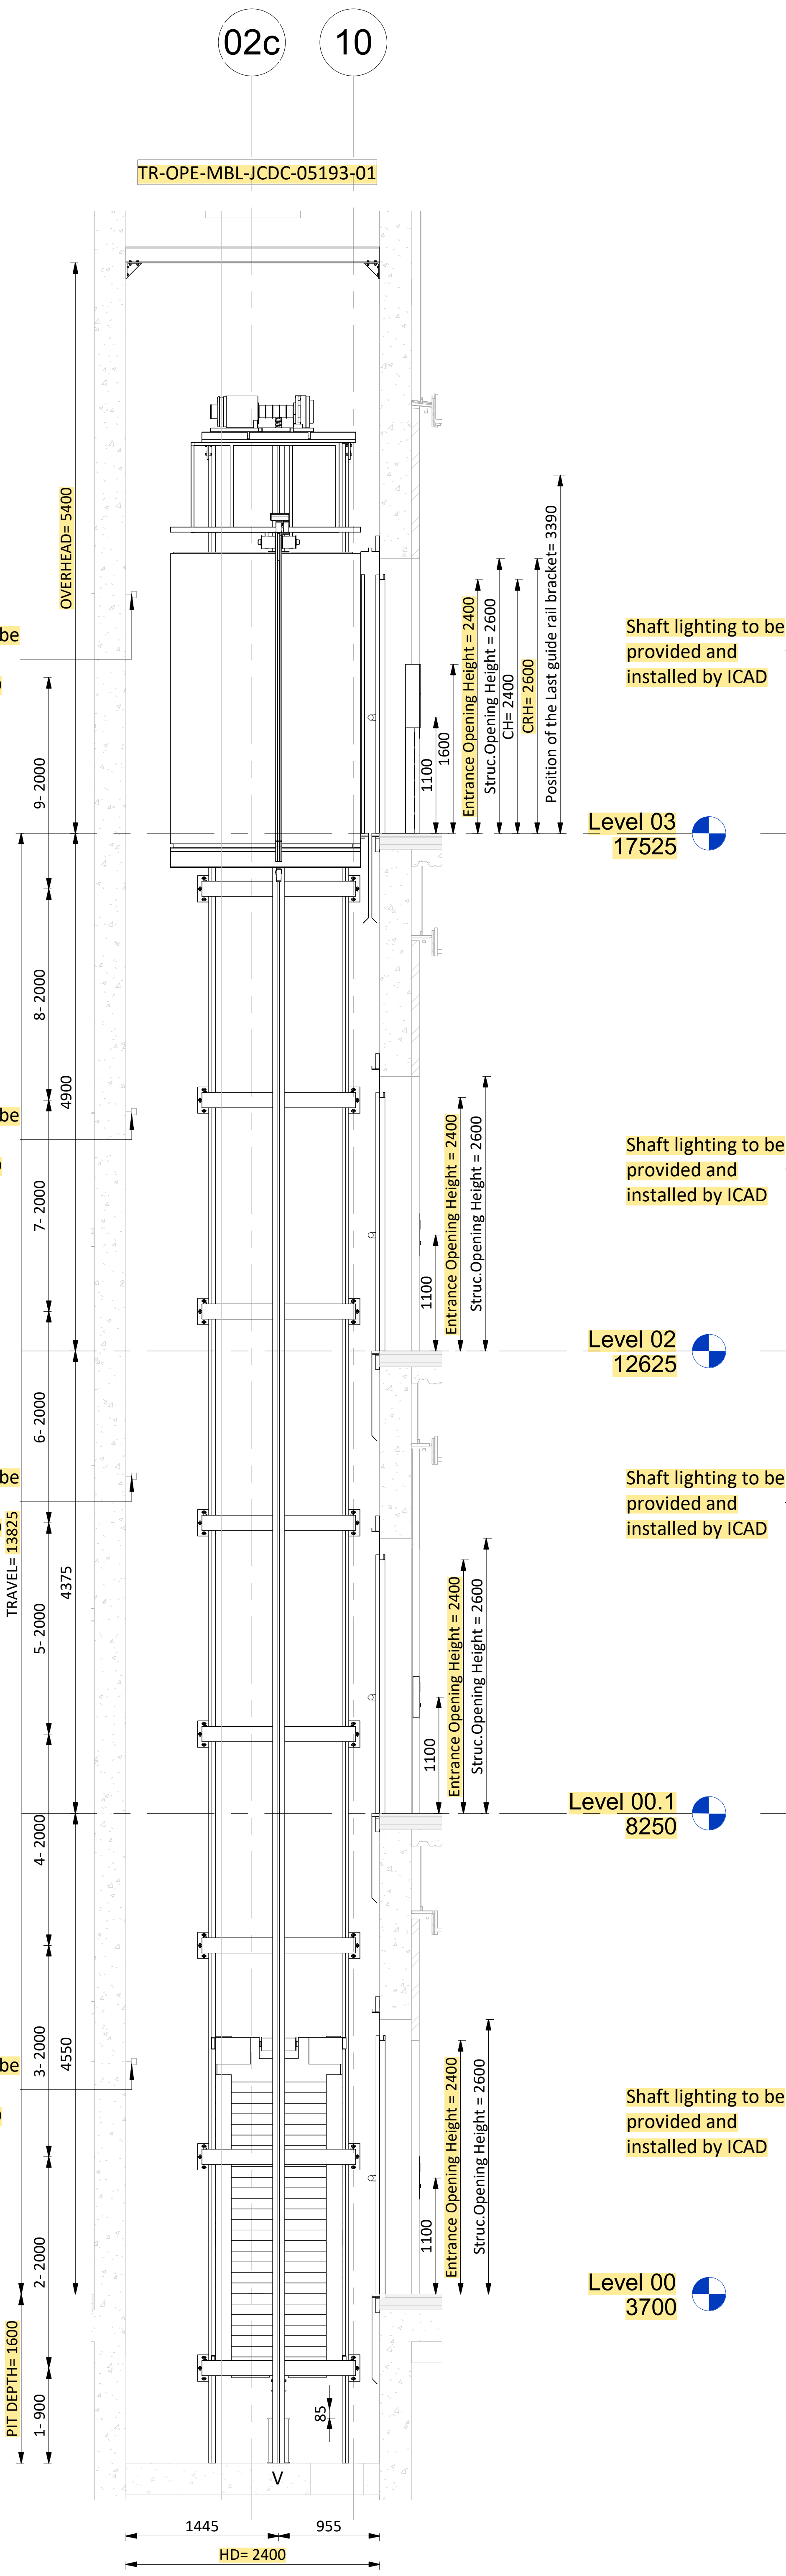

2 Section "B" - ELEV-L19

1 : 50

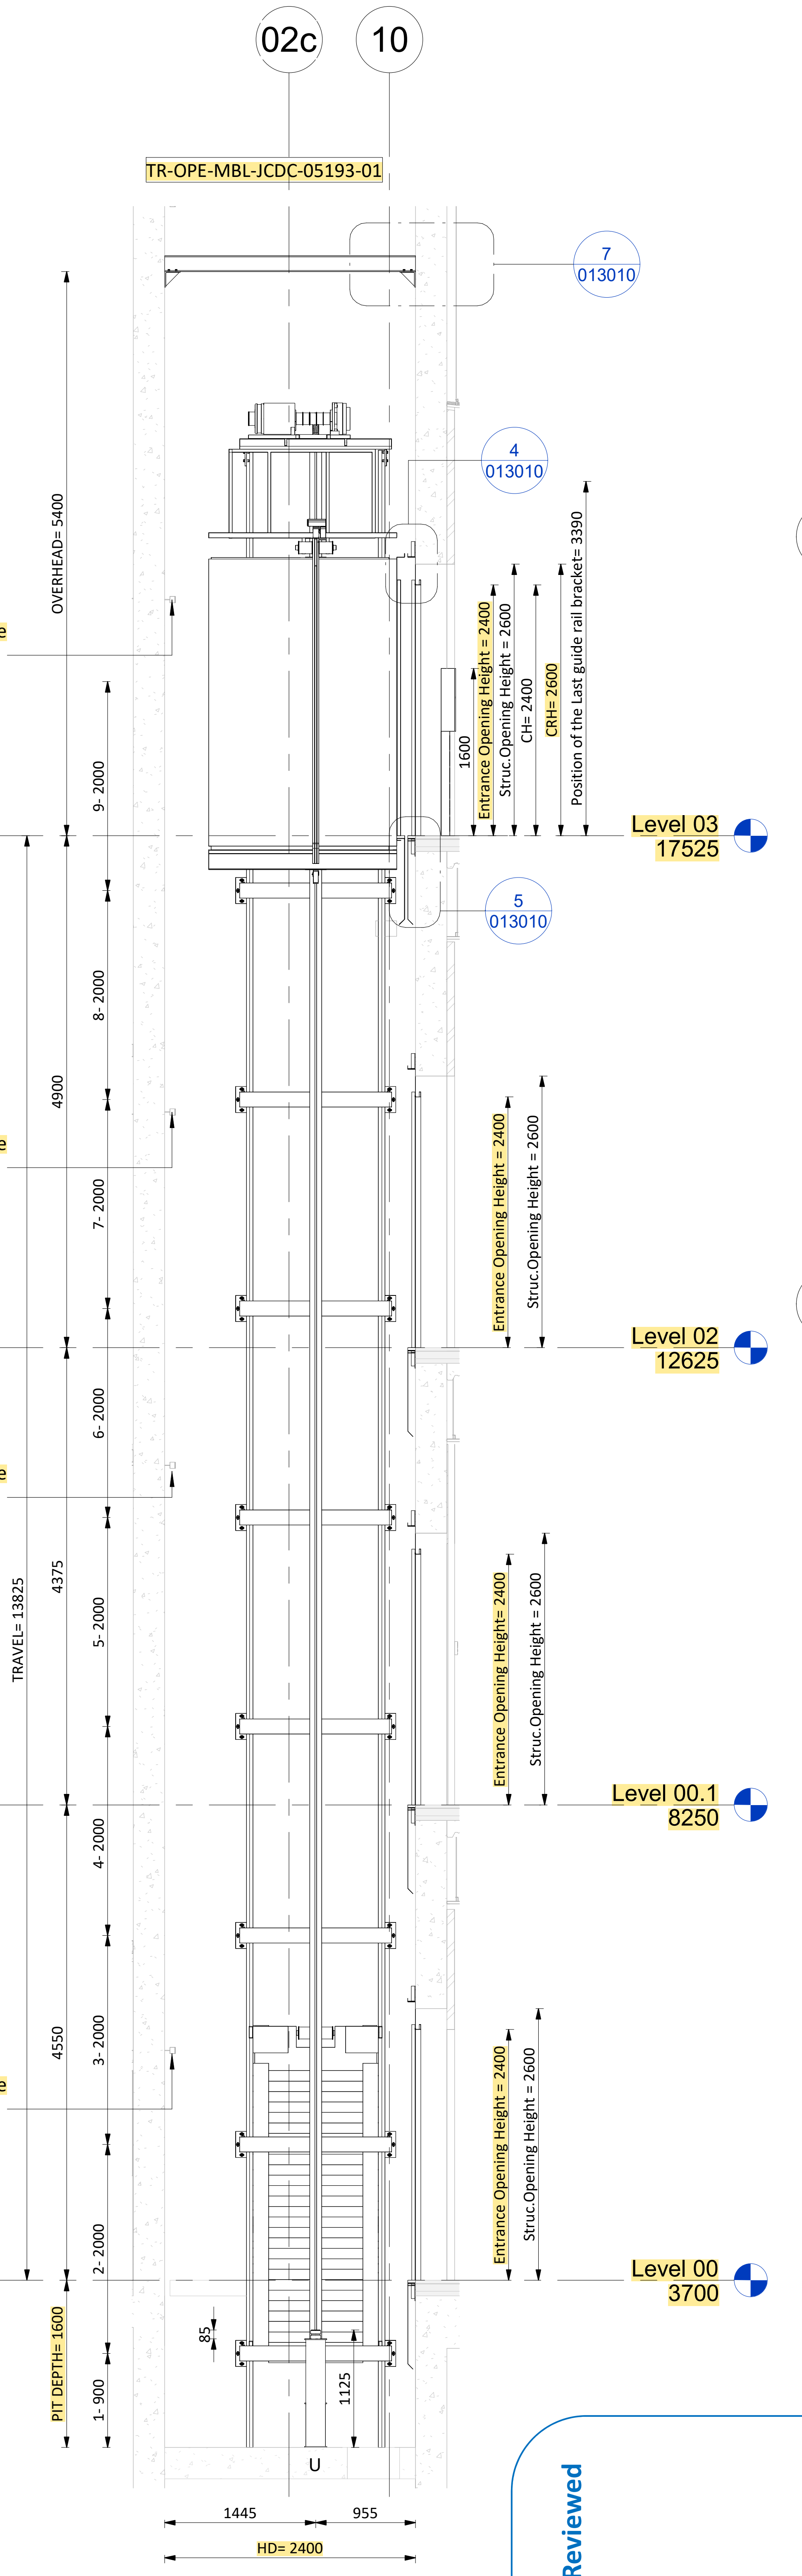

3 Section "C" - ELEV-L2(

1 : 50

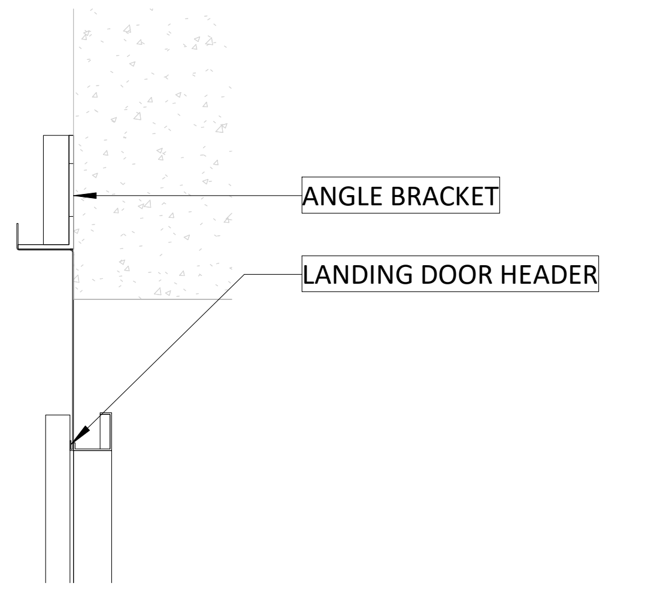

4 Landing Door Header Detail - ELEV-L19 & 20

1 : 10

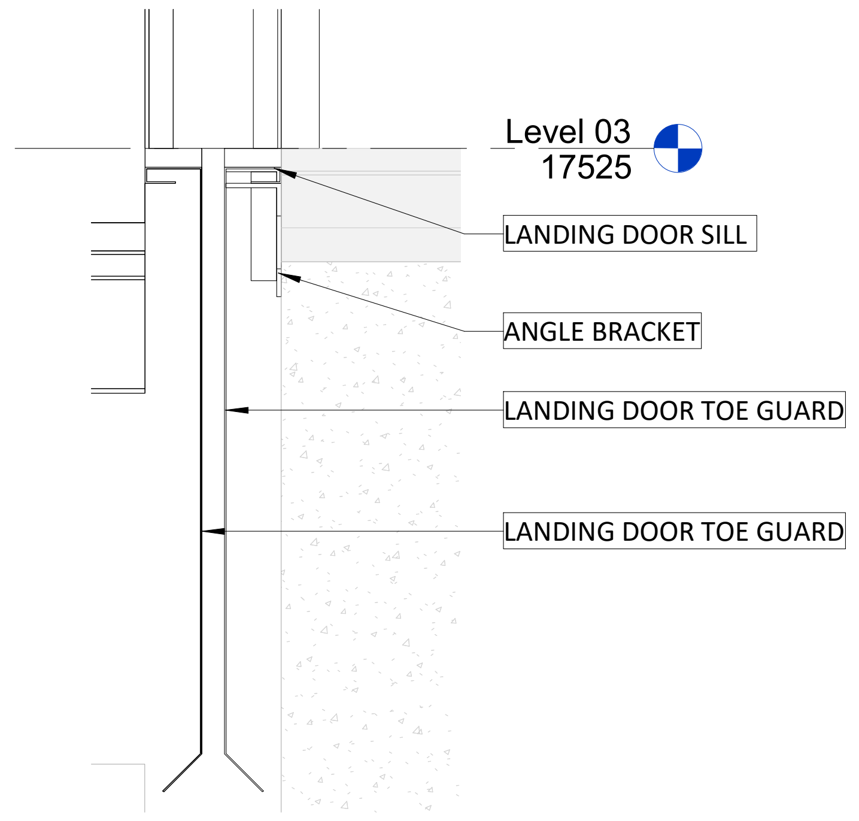

5 Landing Door Bottom Detail - ELEV-L19 & 20

1 : 10

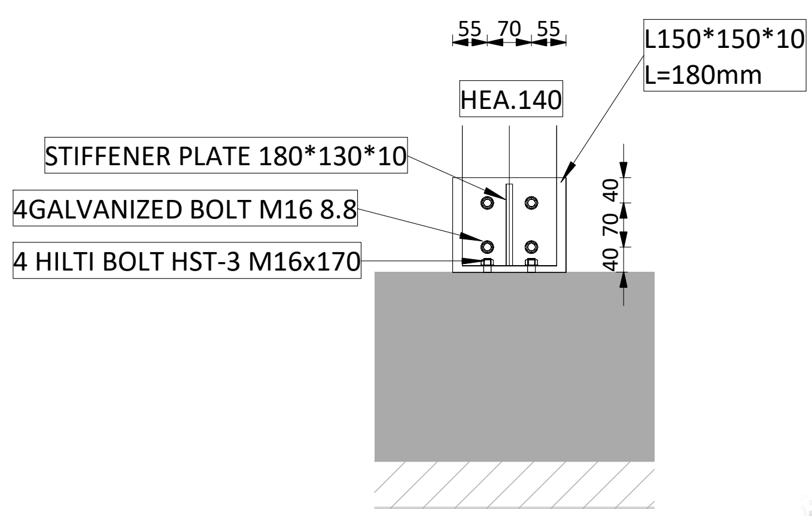

6 DETAIL (A)

1 : 12

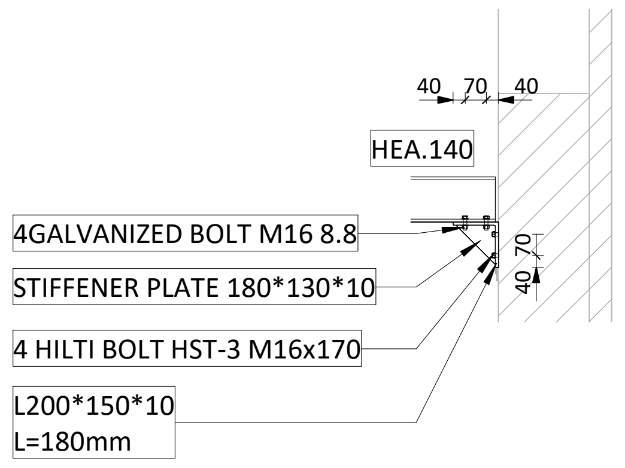

7 DETAIL (A1-A1)

1 : 25

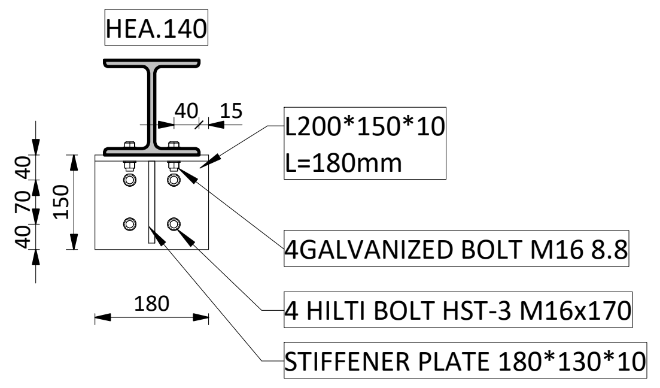

8 DETAIL (B1-B1)

1 : 12

CONTROLLED COPY
MBL IFC
JEDDAH OPERA HOUSE PROJECT
QA/QC Department
MBL QAM
Engr. Mudassar Altaf

SCEC – K&A Reviewed
Code B – Approved with Comments
(Do not Resubmit)

SCEC – K&A Reviewed

Civil	Arch.	Elec.	ELV.	Mech.	Acoustic
☒	☒	☒	☐	☒	☒

Dar Al-Handasah consultants (Shair and Partners)
Checked and Reviewed

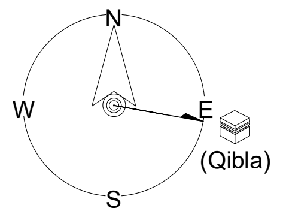

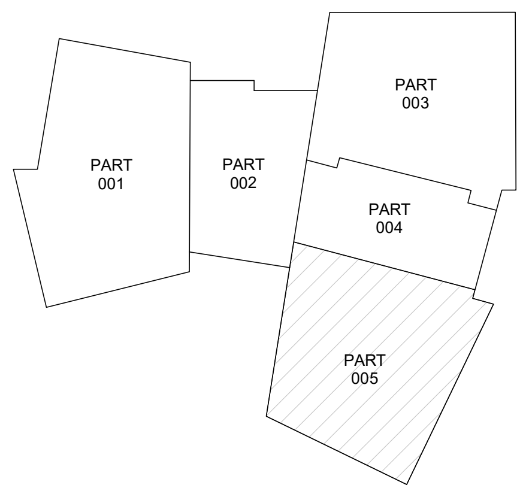

KEY PLAN

GENERAL NOTES: ALL LEVELS SHOWN ON THE DRAWING ARE CHART DATUM LEVELS PROJECT LEVEL+0.000 = +3.700 CHART DATUM.

Refer to :
LIFTS overhead steel hook beams structural
calculation and fixation details: TR-OPE-MBL-JCDC-05193-S01
CRS: SD-OPE-MBL-JCDC-01382 - CRS - version-(0_00)-L19,20
Electrical Panels distribution:
JOH-ICD-S5-01-056-005-02-SD-EL-011625
JOH-ICD-S5-01-056-XXX-03-SD-EL-011630_1
wiring diagram opera lift
Acoustic Letter: L-OTIS-MBL-OPE-26-0015

DRAWING / DOCUMENT REFERENCE

NO.	NUMBER	TITLE	REV.
01	L-19 & L-20	JOH-HLA-S4-01-056-005-00-DR-AR-011105	F00
02		JOH-BHC-S4-01-056-XXX-XX-DR-VT-015001	
03		JOH-BHC-S4-01-056-XXX-XX-DR-VT-010001	
04		JOH-BHC-S4-01-056-005-ZZ-DR-VT-013001	
05		JOH-BHC-S4-01-056-005-ZZ-DR-VT-011001	
06		TQ-OPE-MBL-JCDC-00222	
07		TQ-OPE-MBL-JCDC-01258	
08		JCD-OPE-MBL-MR-003-NMR-601-03	
09		JCD-OPE-MBL-MR-003-NMR-602-01	
10		TR-OPE-MBL-JCDC-05193-01	

REVIEWED BY DISCIPLINE	SIGNATURE	DATE
ARCHITECTURAL	MT	[illegible]
STRUCTURAL	PC	[illegible]
MECHANICAL	ShA	[illegible]-05-20
PLUMBING	[illegible]	[illegible]
ELECTRICAL	ShA	2026-05-20
ICT	ShA	[illegible]
ADDITIONAL DISCIPLINES TO BE ADDED AS REQUIRED		

REV	DATE	BY	DESCRIPTION	CHK	APD
S01	07-MAY-2026	AK	Shop Drawing	SS	AB
S00	06-MAY-2026	AK	Issued for Approval	SS	AB

DRAWING STATUS:
CONSTRUCTION SHOPDRAWING

CLIENT:
شركة وسط جدة للتطوير
Jeddah Central Development Co.

LEAD DESIGN CONSULTANTS:
Henning Larsen

LEAD ENGINEERING CONSULTANT:
BURO HAPPOLD

PROJECT SUPERVISION CONSULTANT:
KHATIB & ALAMI

GENERAL CONTRACTOR:
MBL

REVIEWER:
dar

SUB CONTRACTOR:
OTIS ELEVATOR COMPANY SAUDI ARABIA LIMITED
OTIS

PROJECT
JEDDAH OPERA HOUSE

TITLE:
OPERA BUILDING
VERTICAL TRANSPORTATION
PART 005
SECTIONS - LIFT SHAFT (L19 & L20)

SCALE @ A1: As indicated
CHECKED: SS
APPROVED: AB
PROJECT No: 440014
DESIGNED: AK
DRAWN: Pranoti
DATE: 07-MAY-2026
DRAWING No: JOH-OTS-S5-01-056-005-ZZ-SD-VT-013010
REV: S01
MODEL FILE REF: JOH-OTS-S5-01-056-XXX-ZZ-M3-VT-010001

ⓒ JCDC